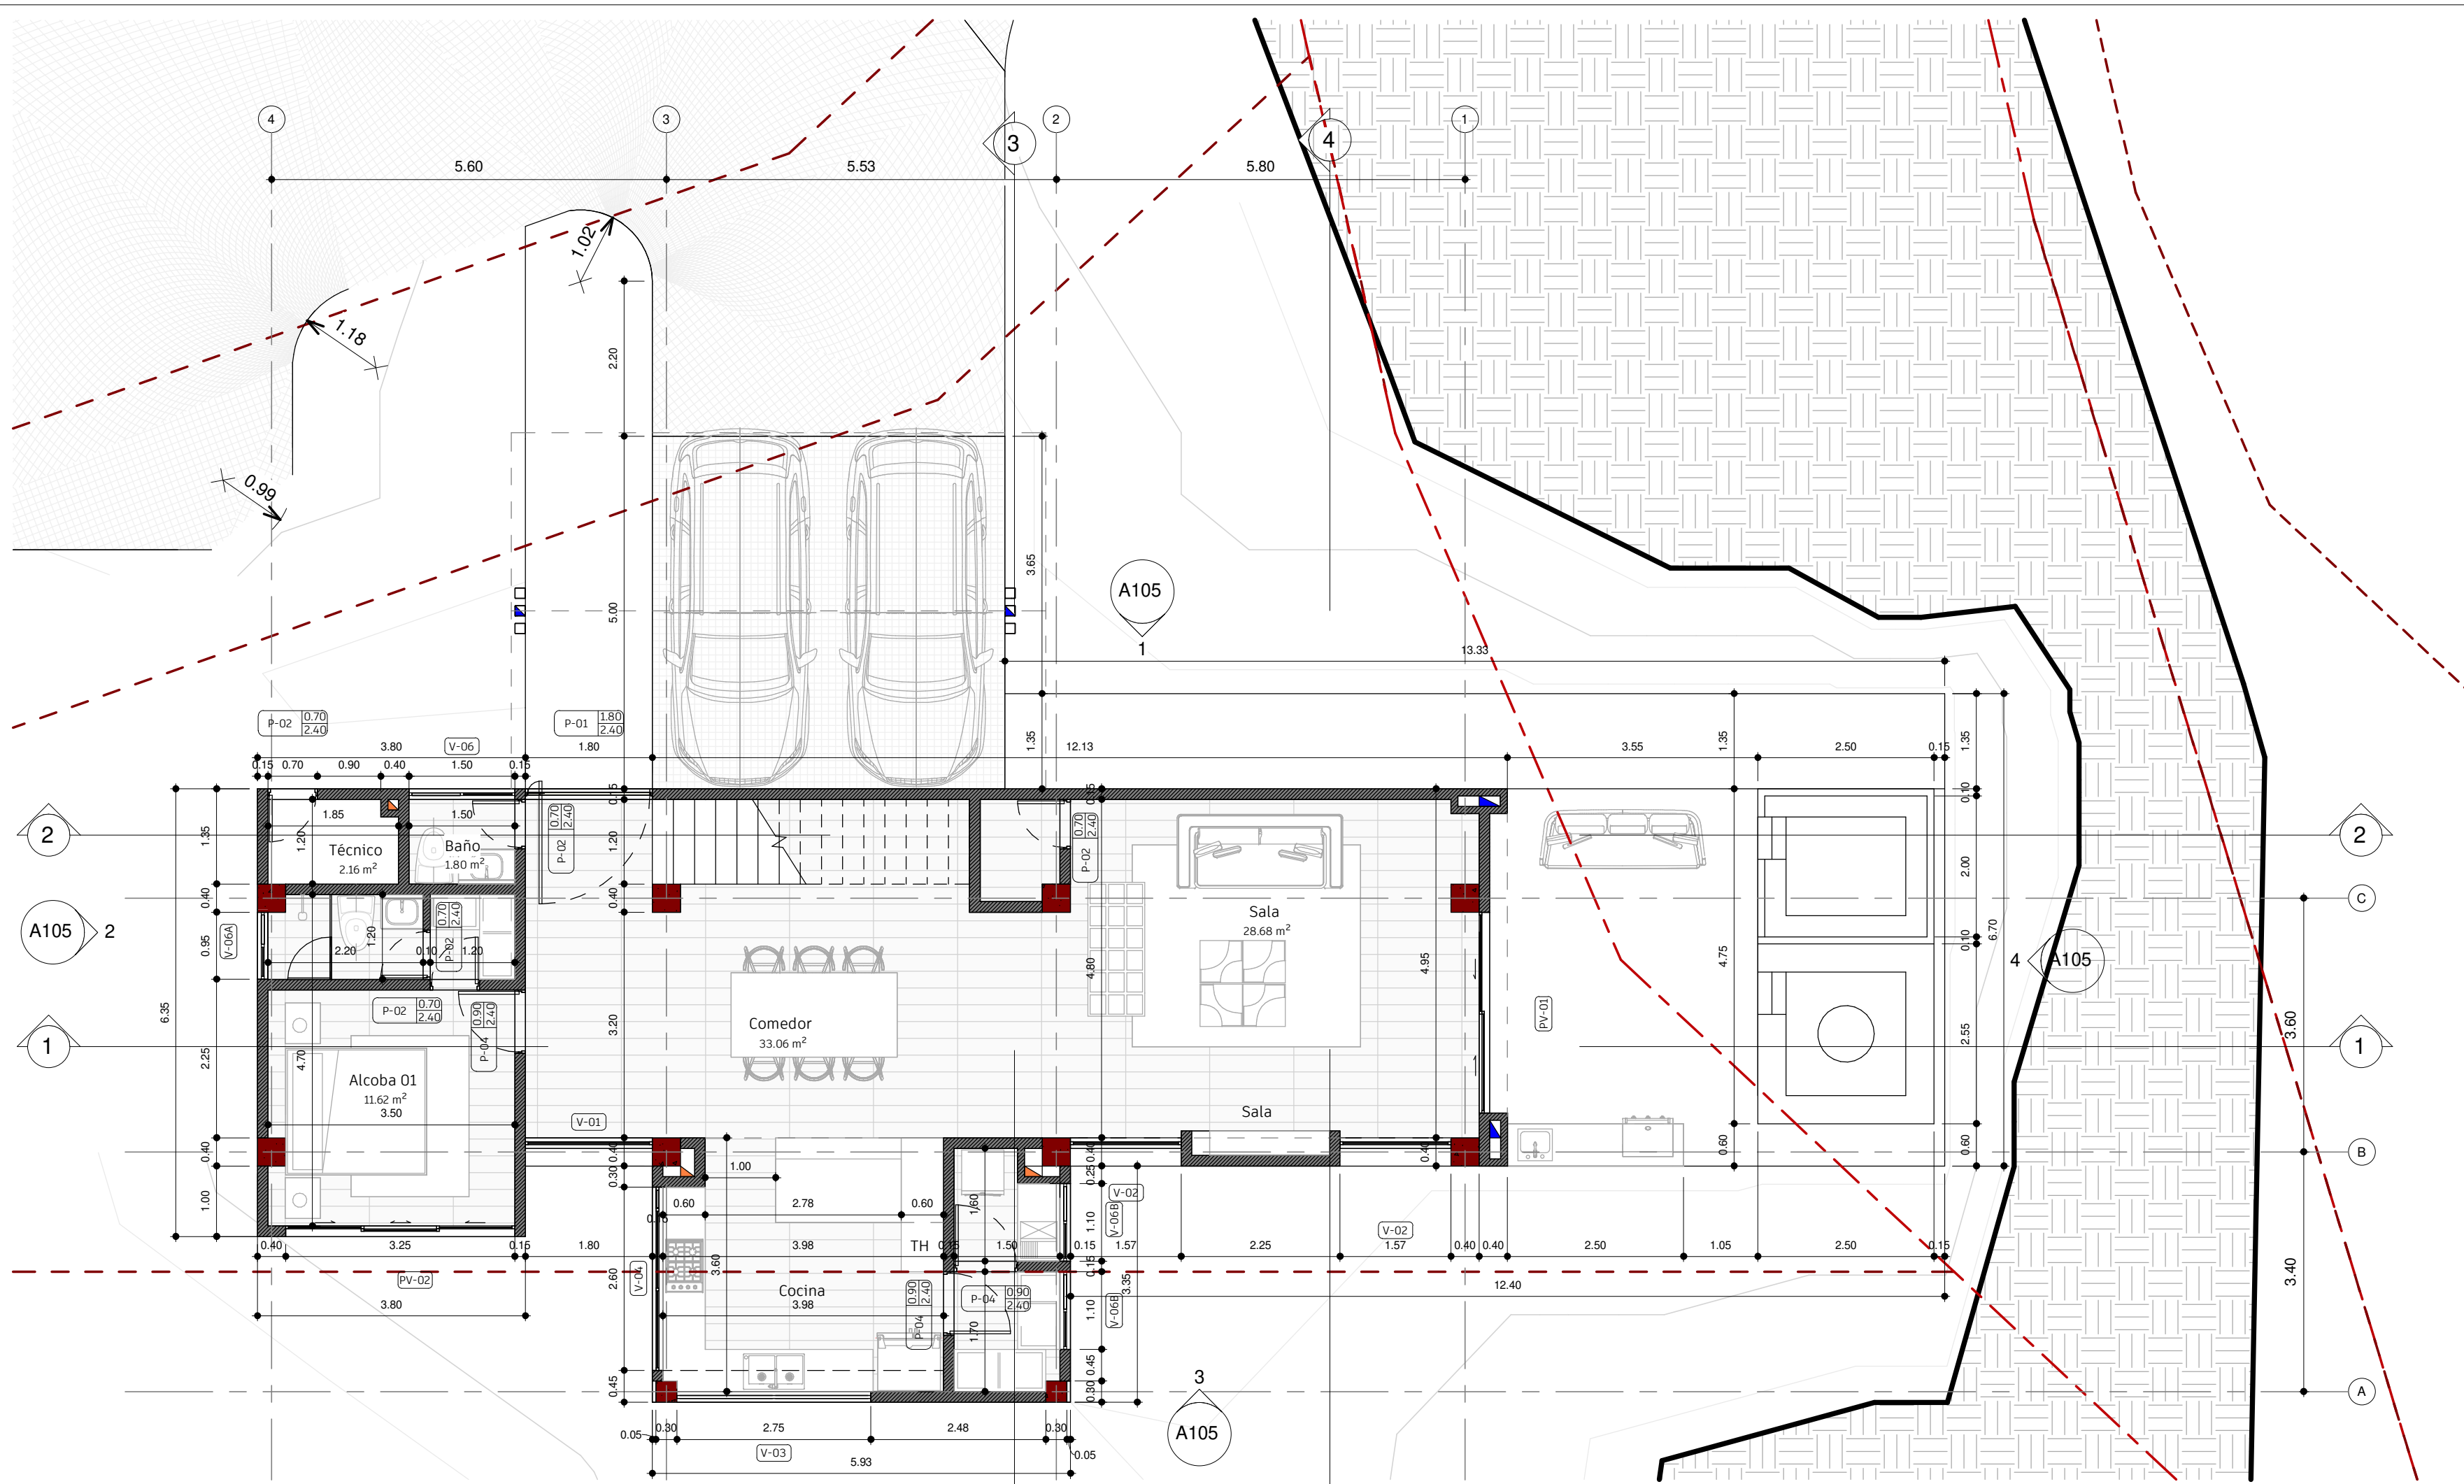
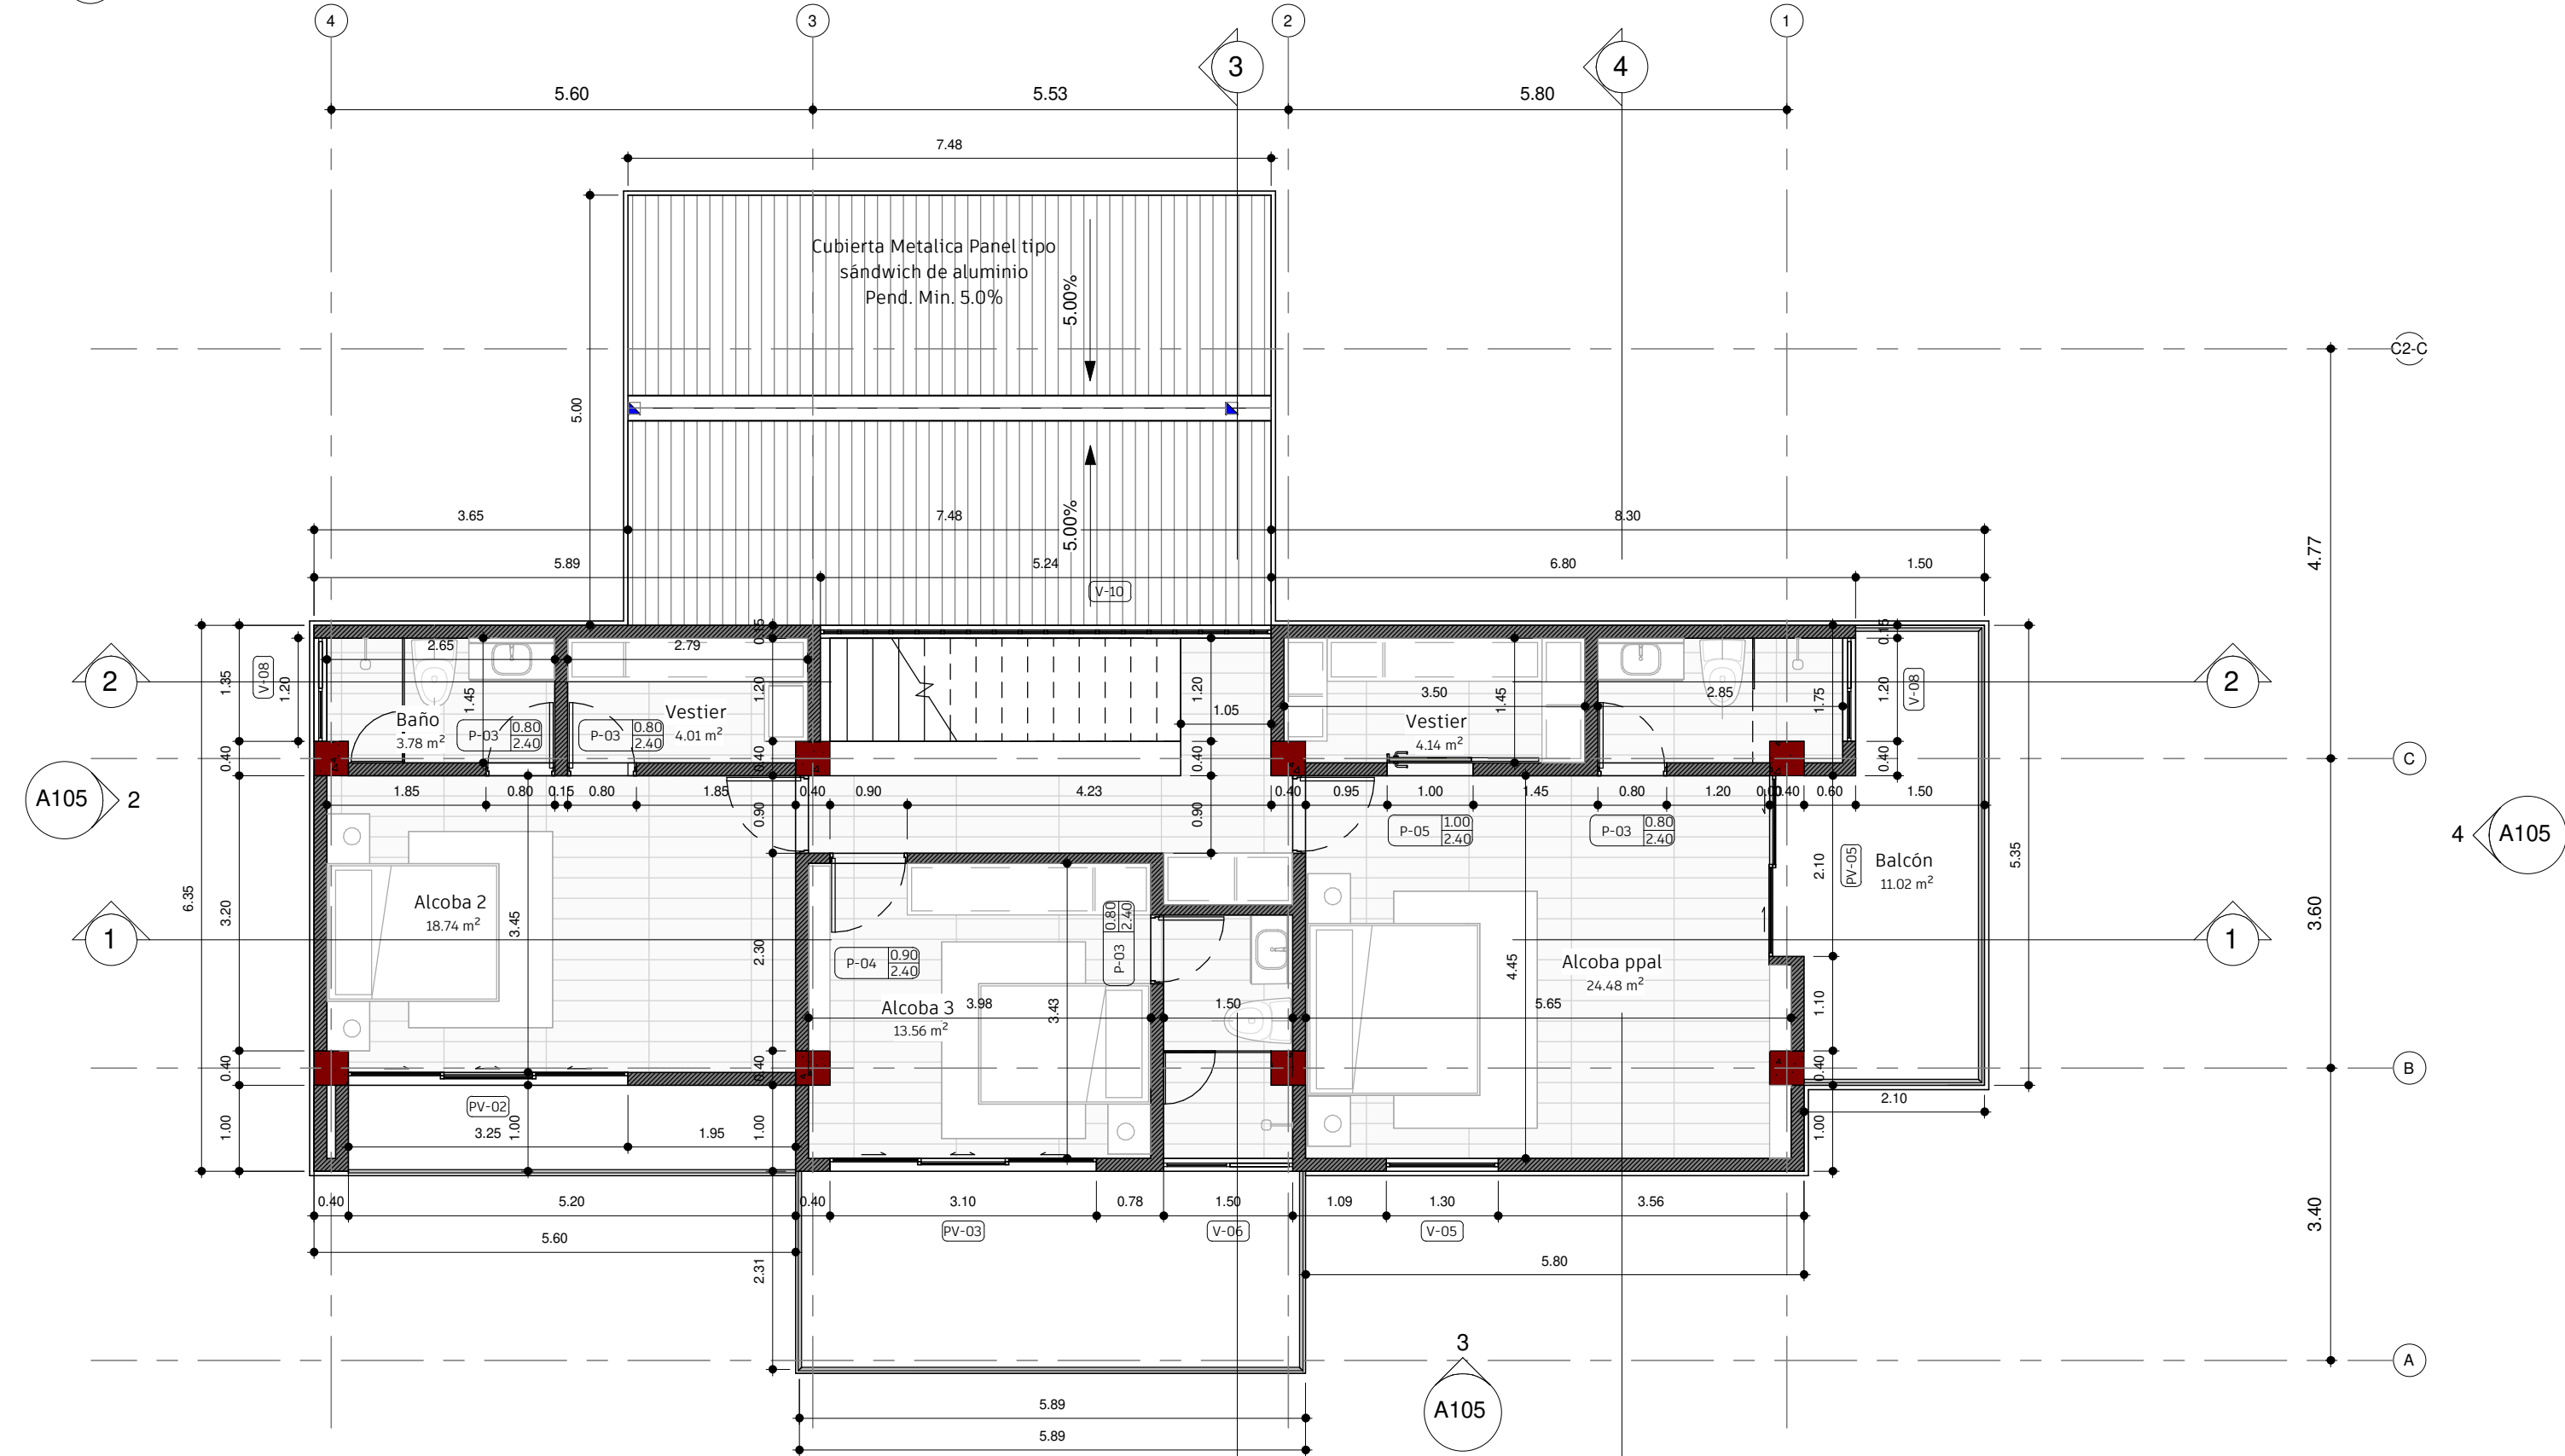
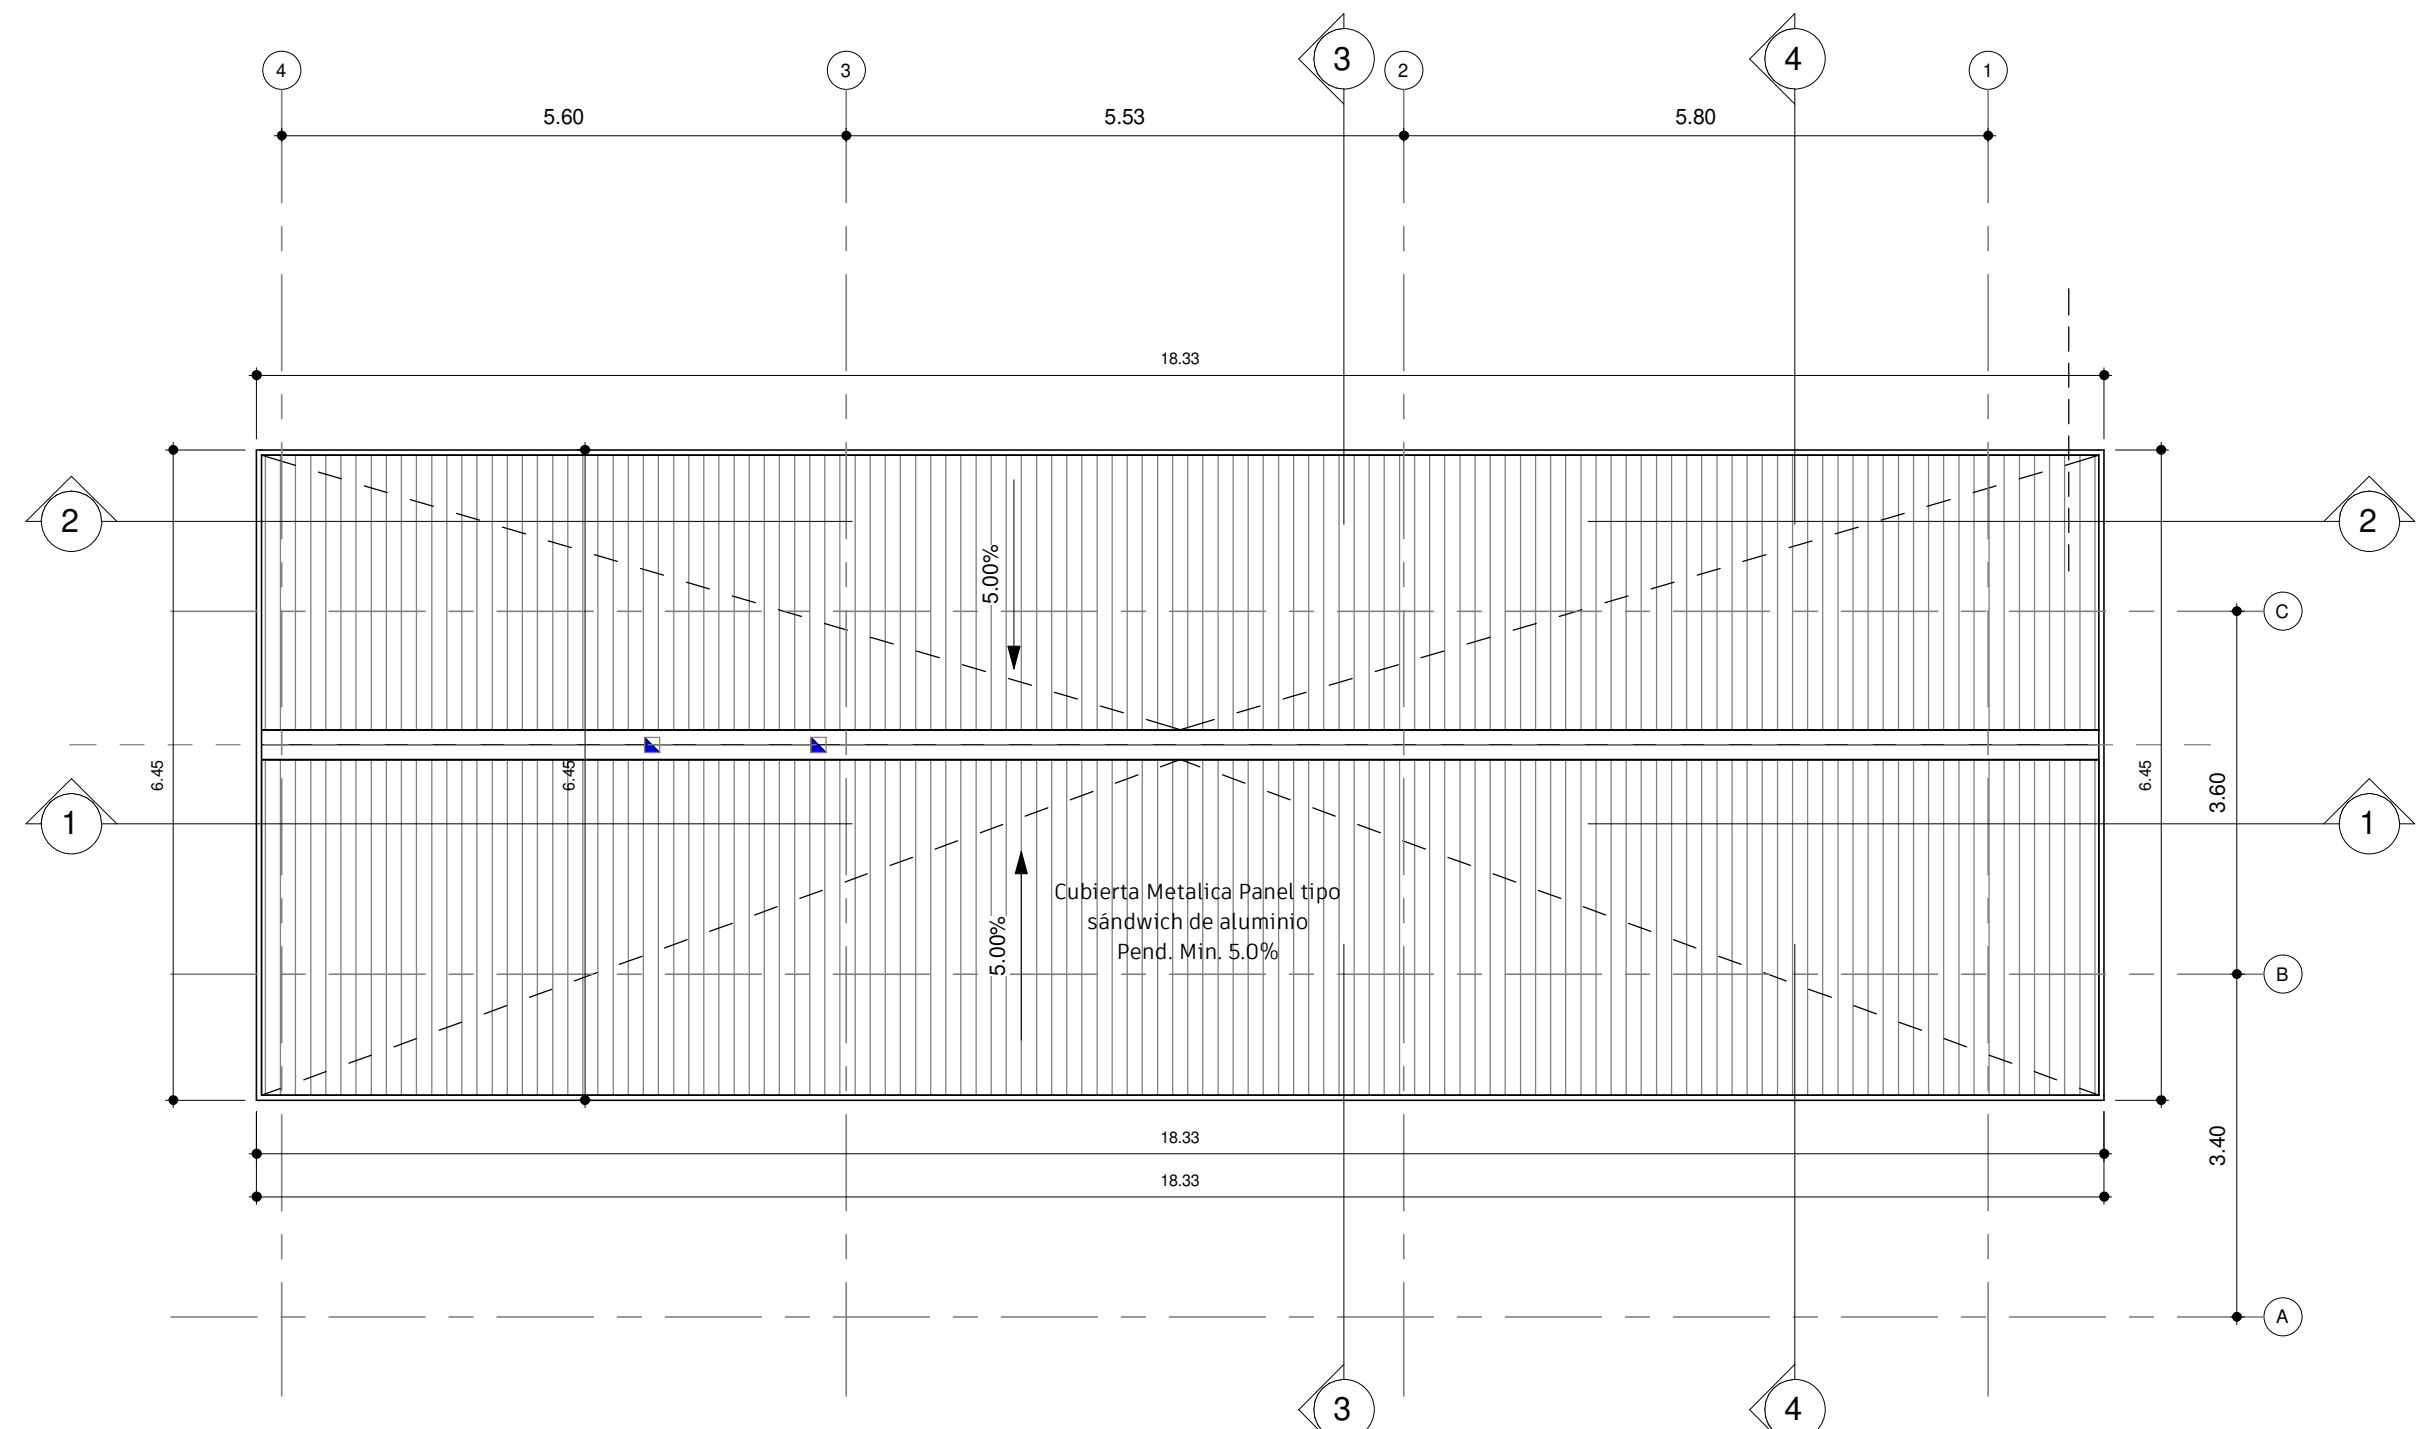




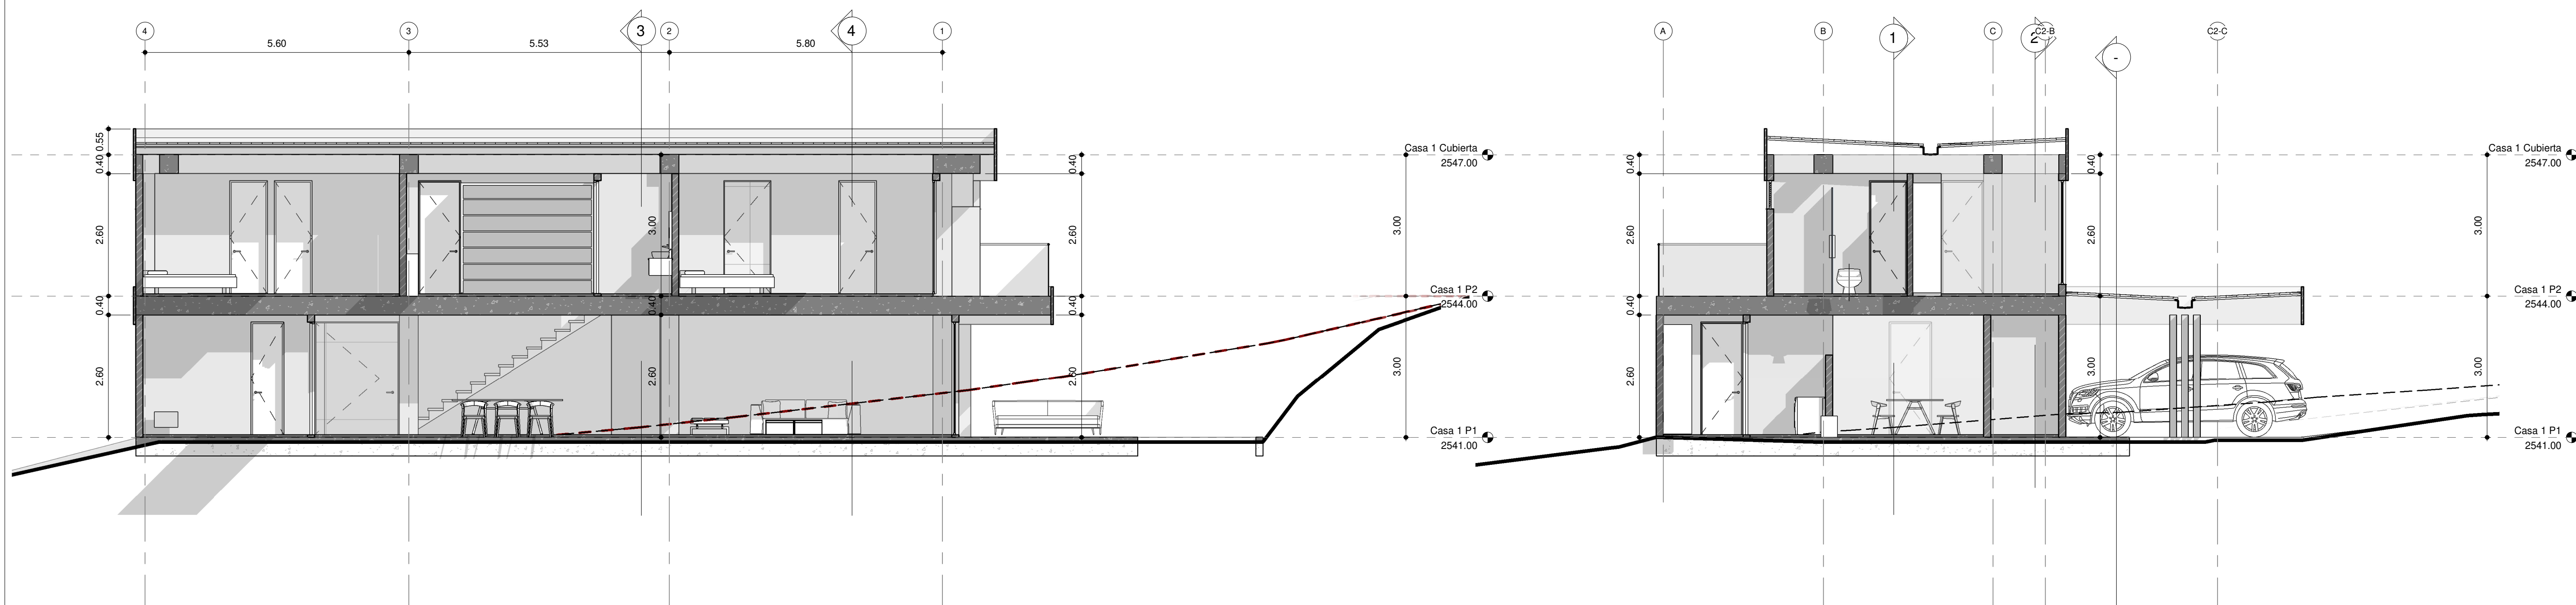
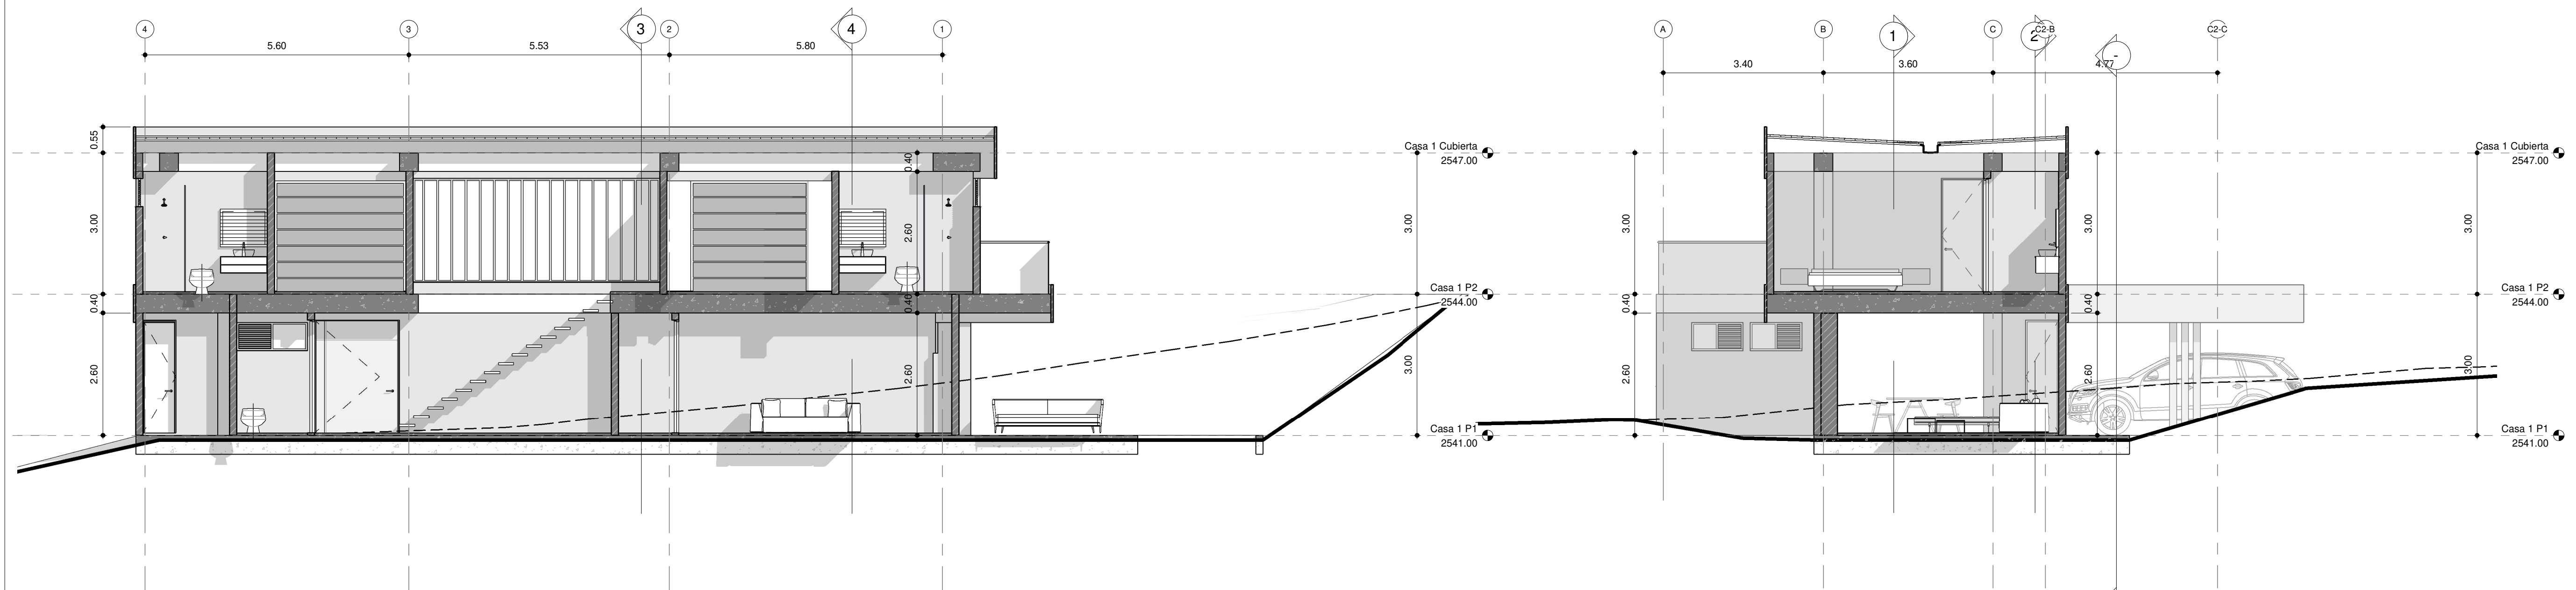
1 Casa 1 P1
1:75

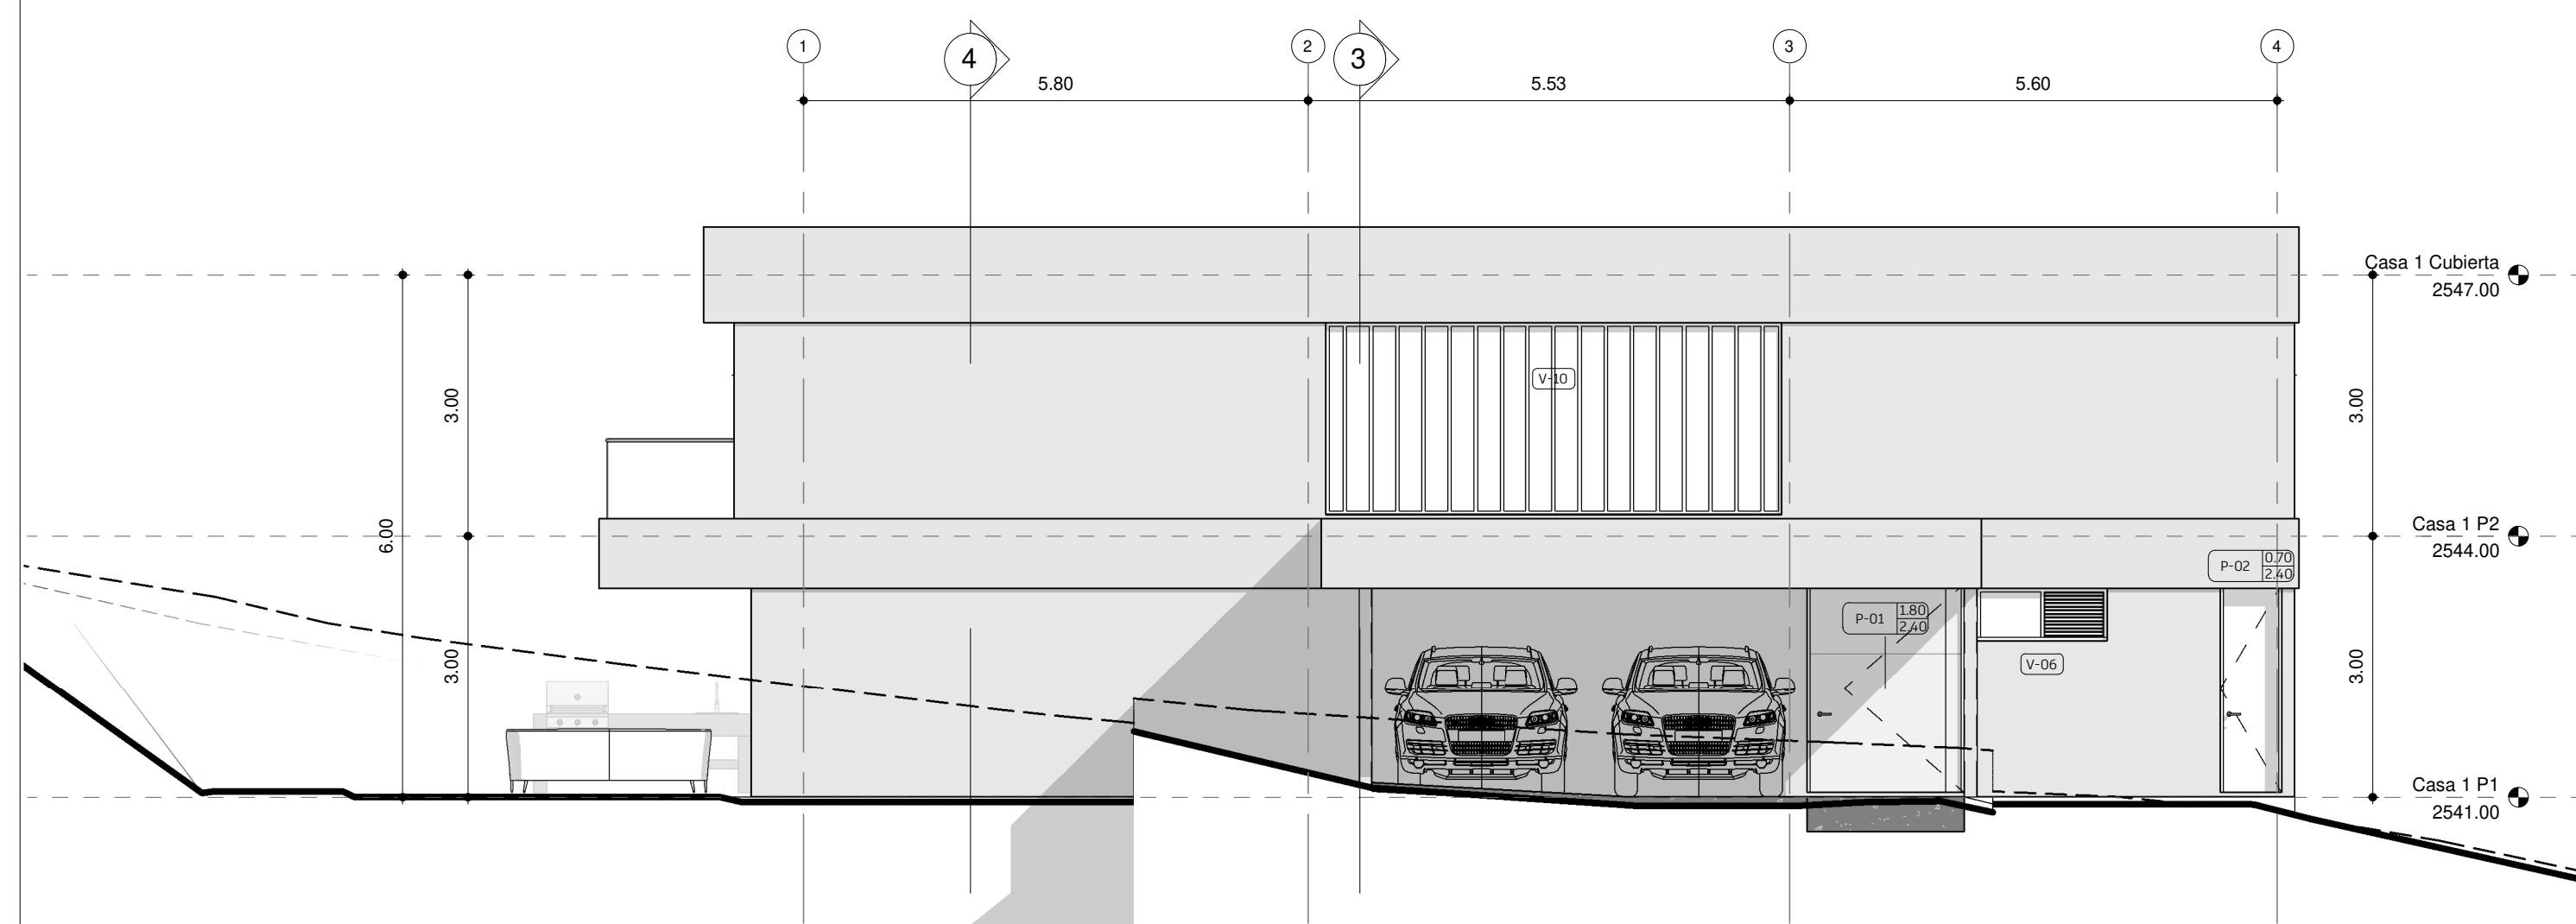
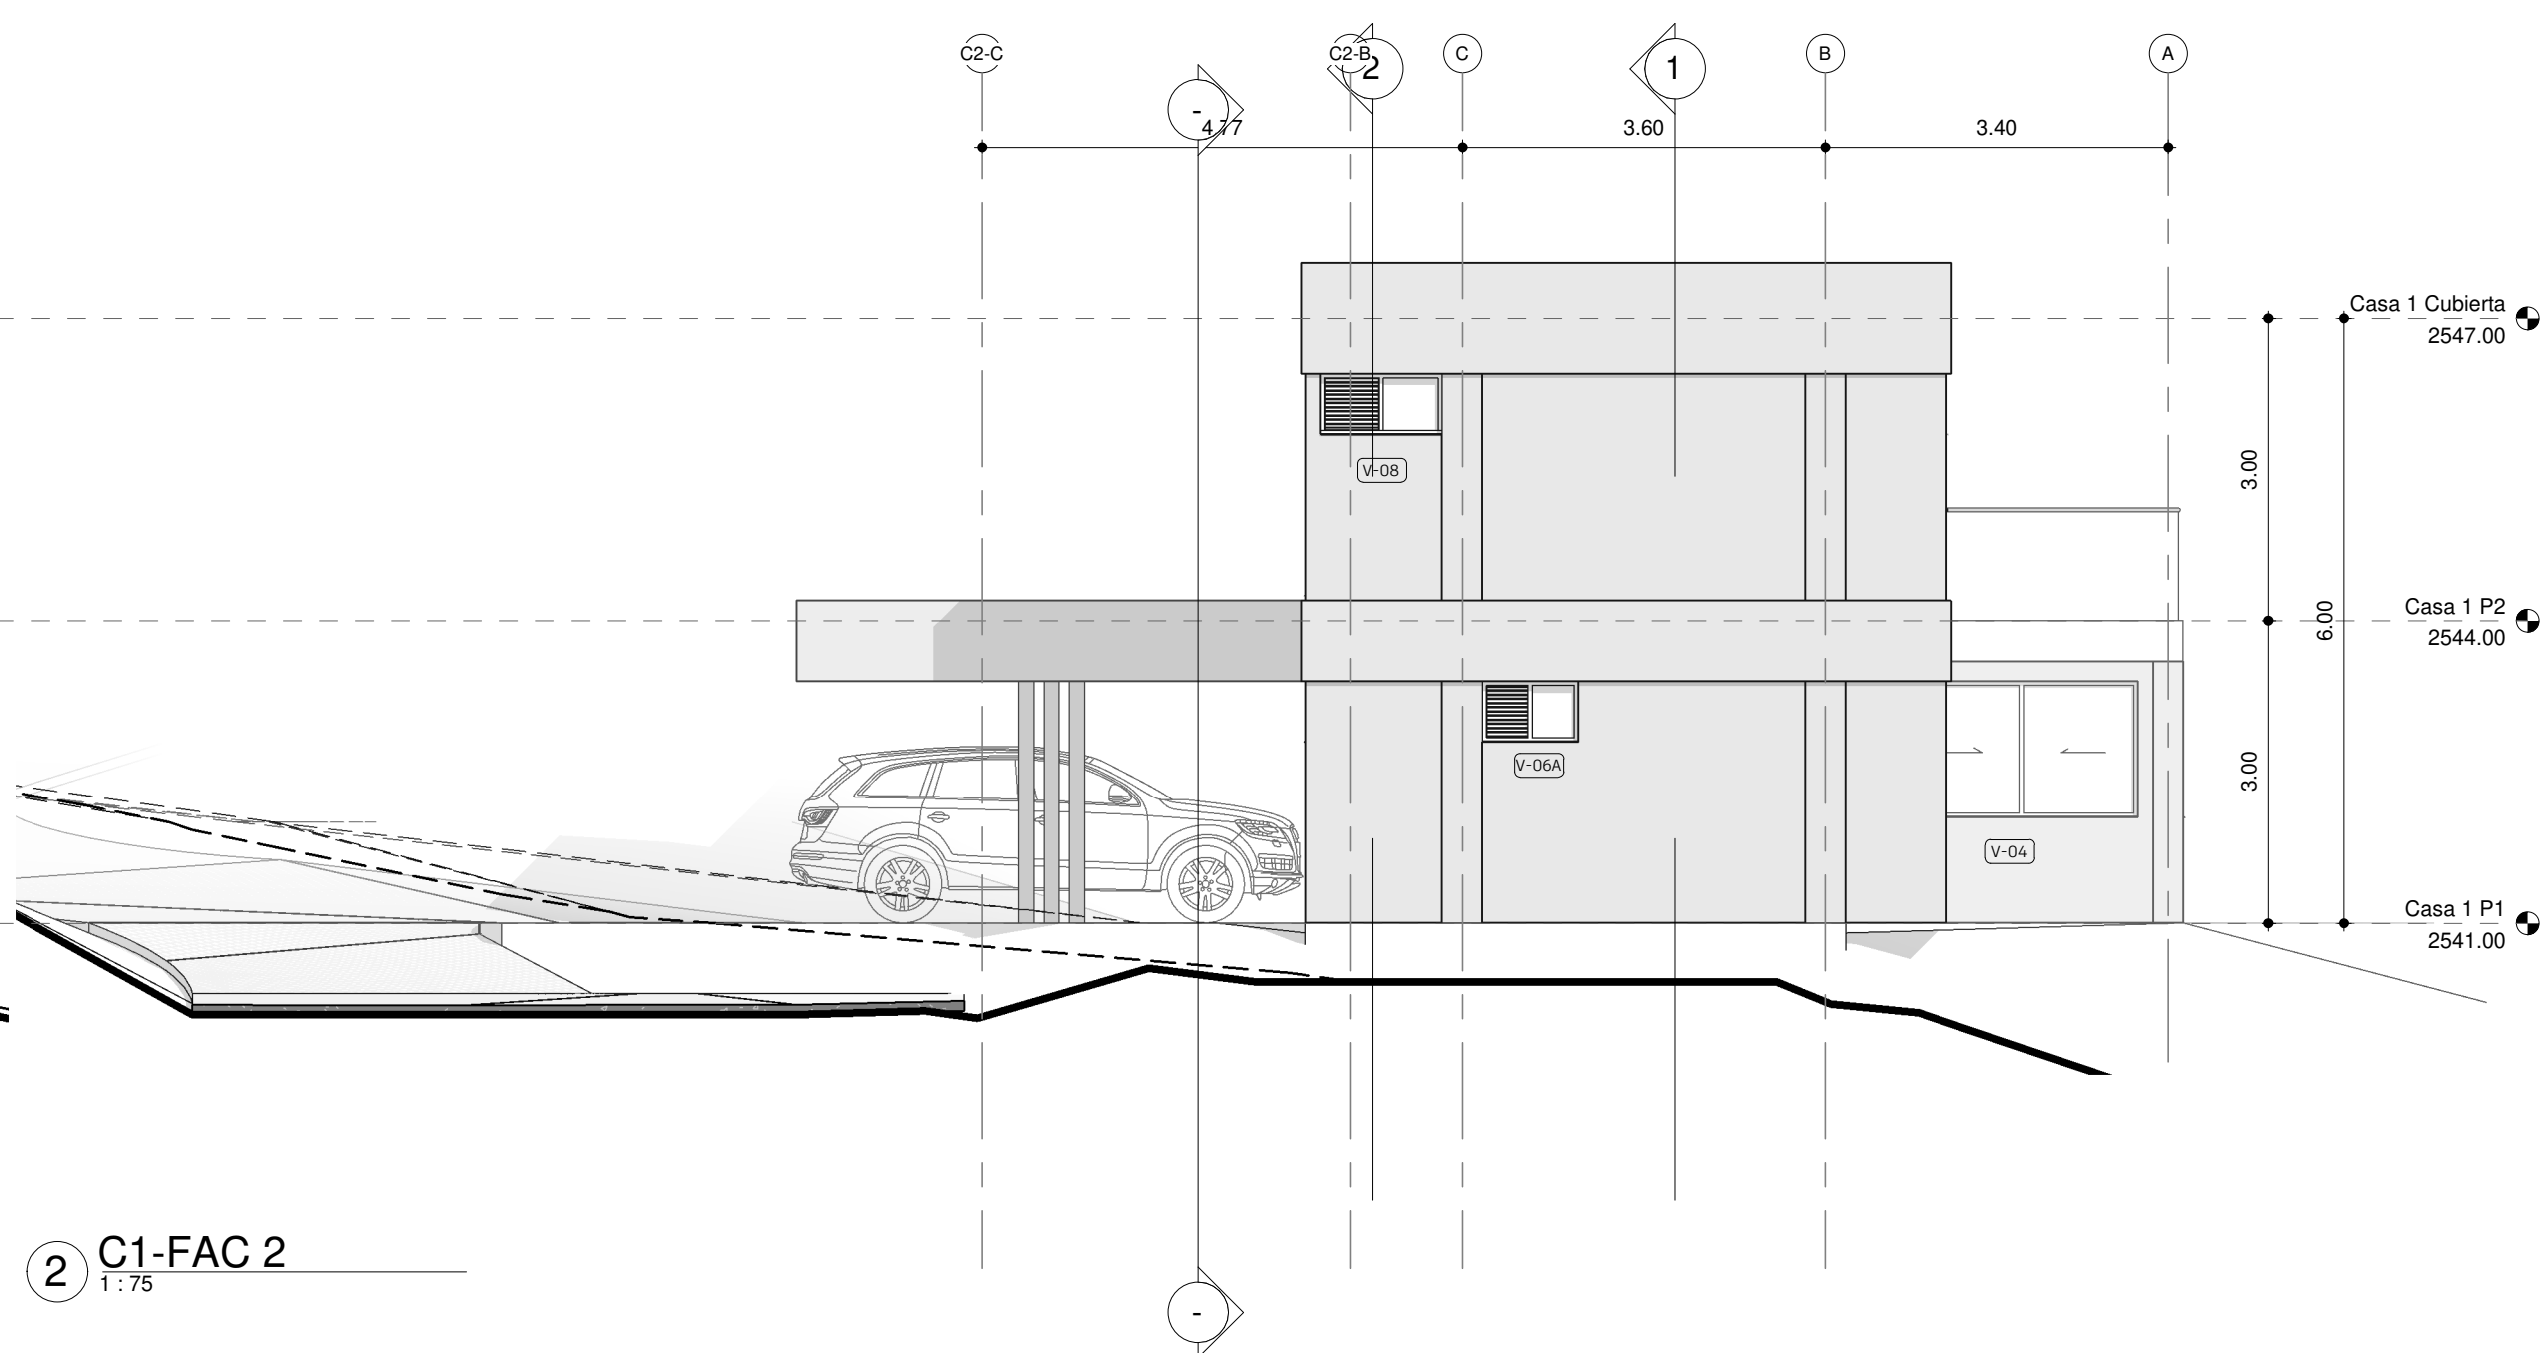
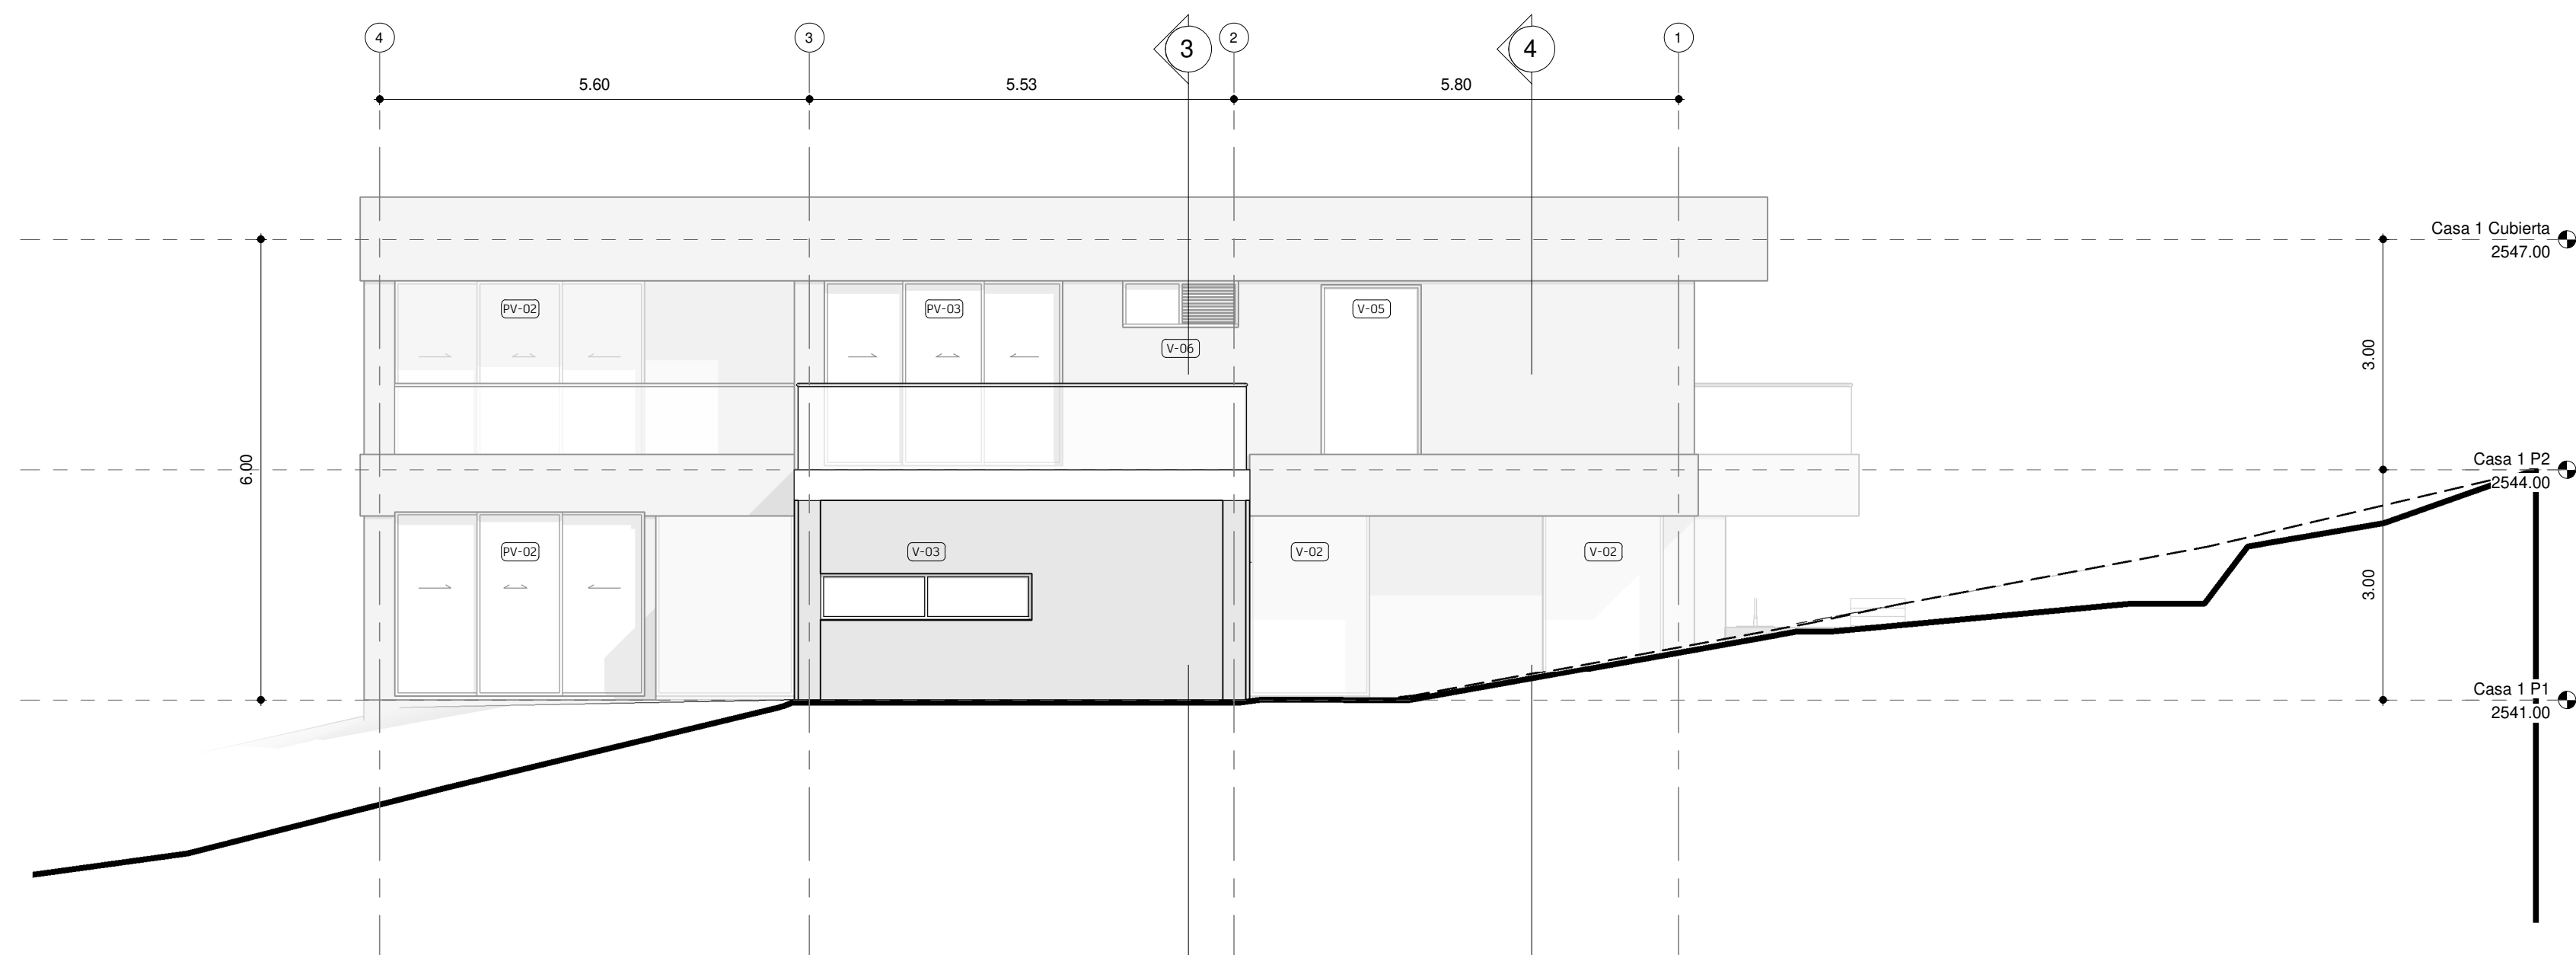
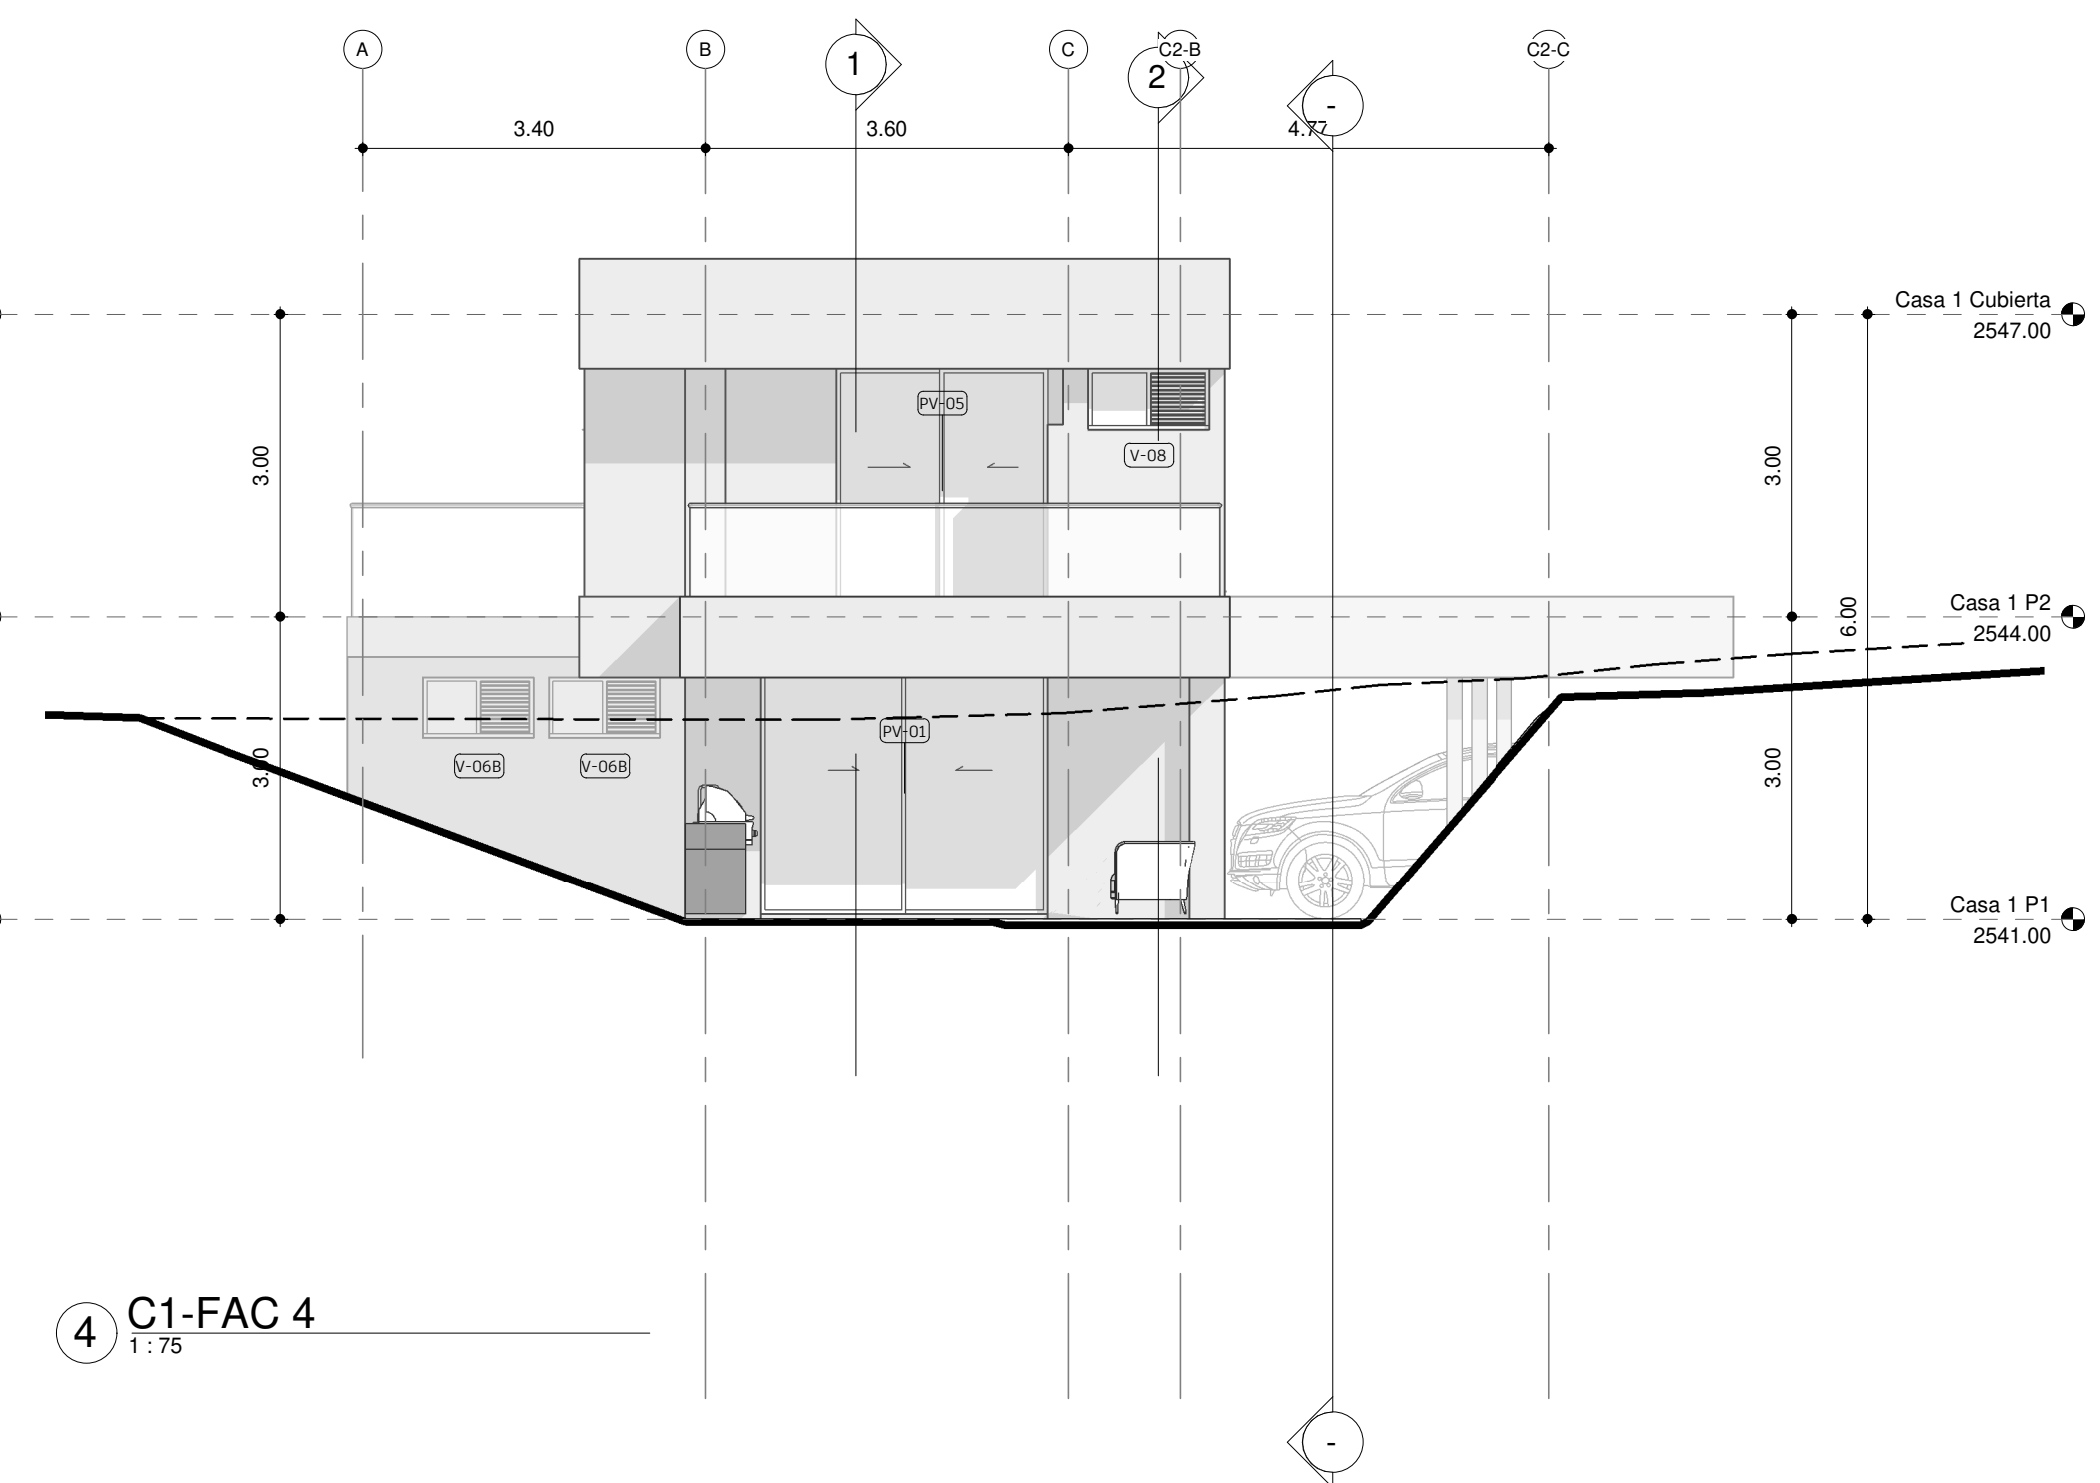


2 Casa 1 P2
1:75



3 Casa 1 Cubierta
1:75

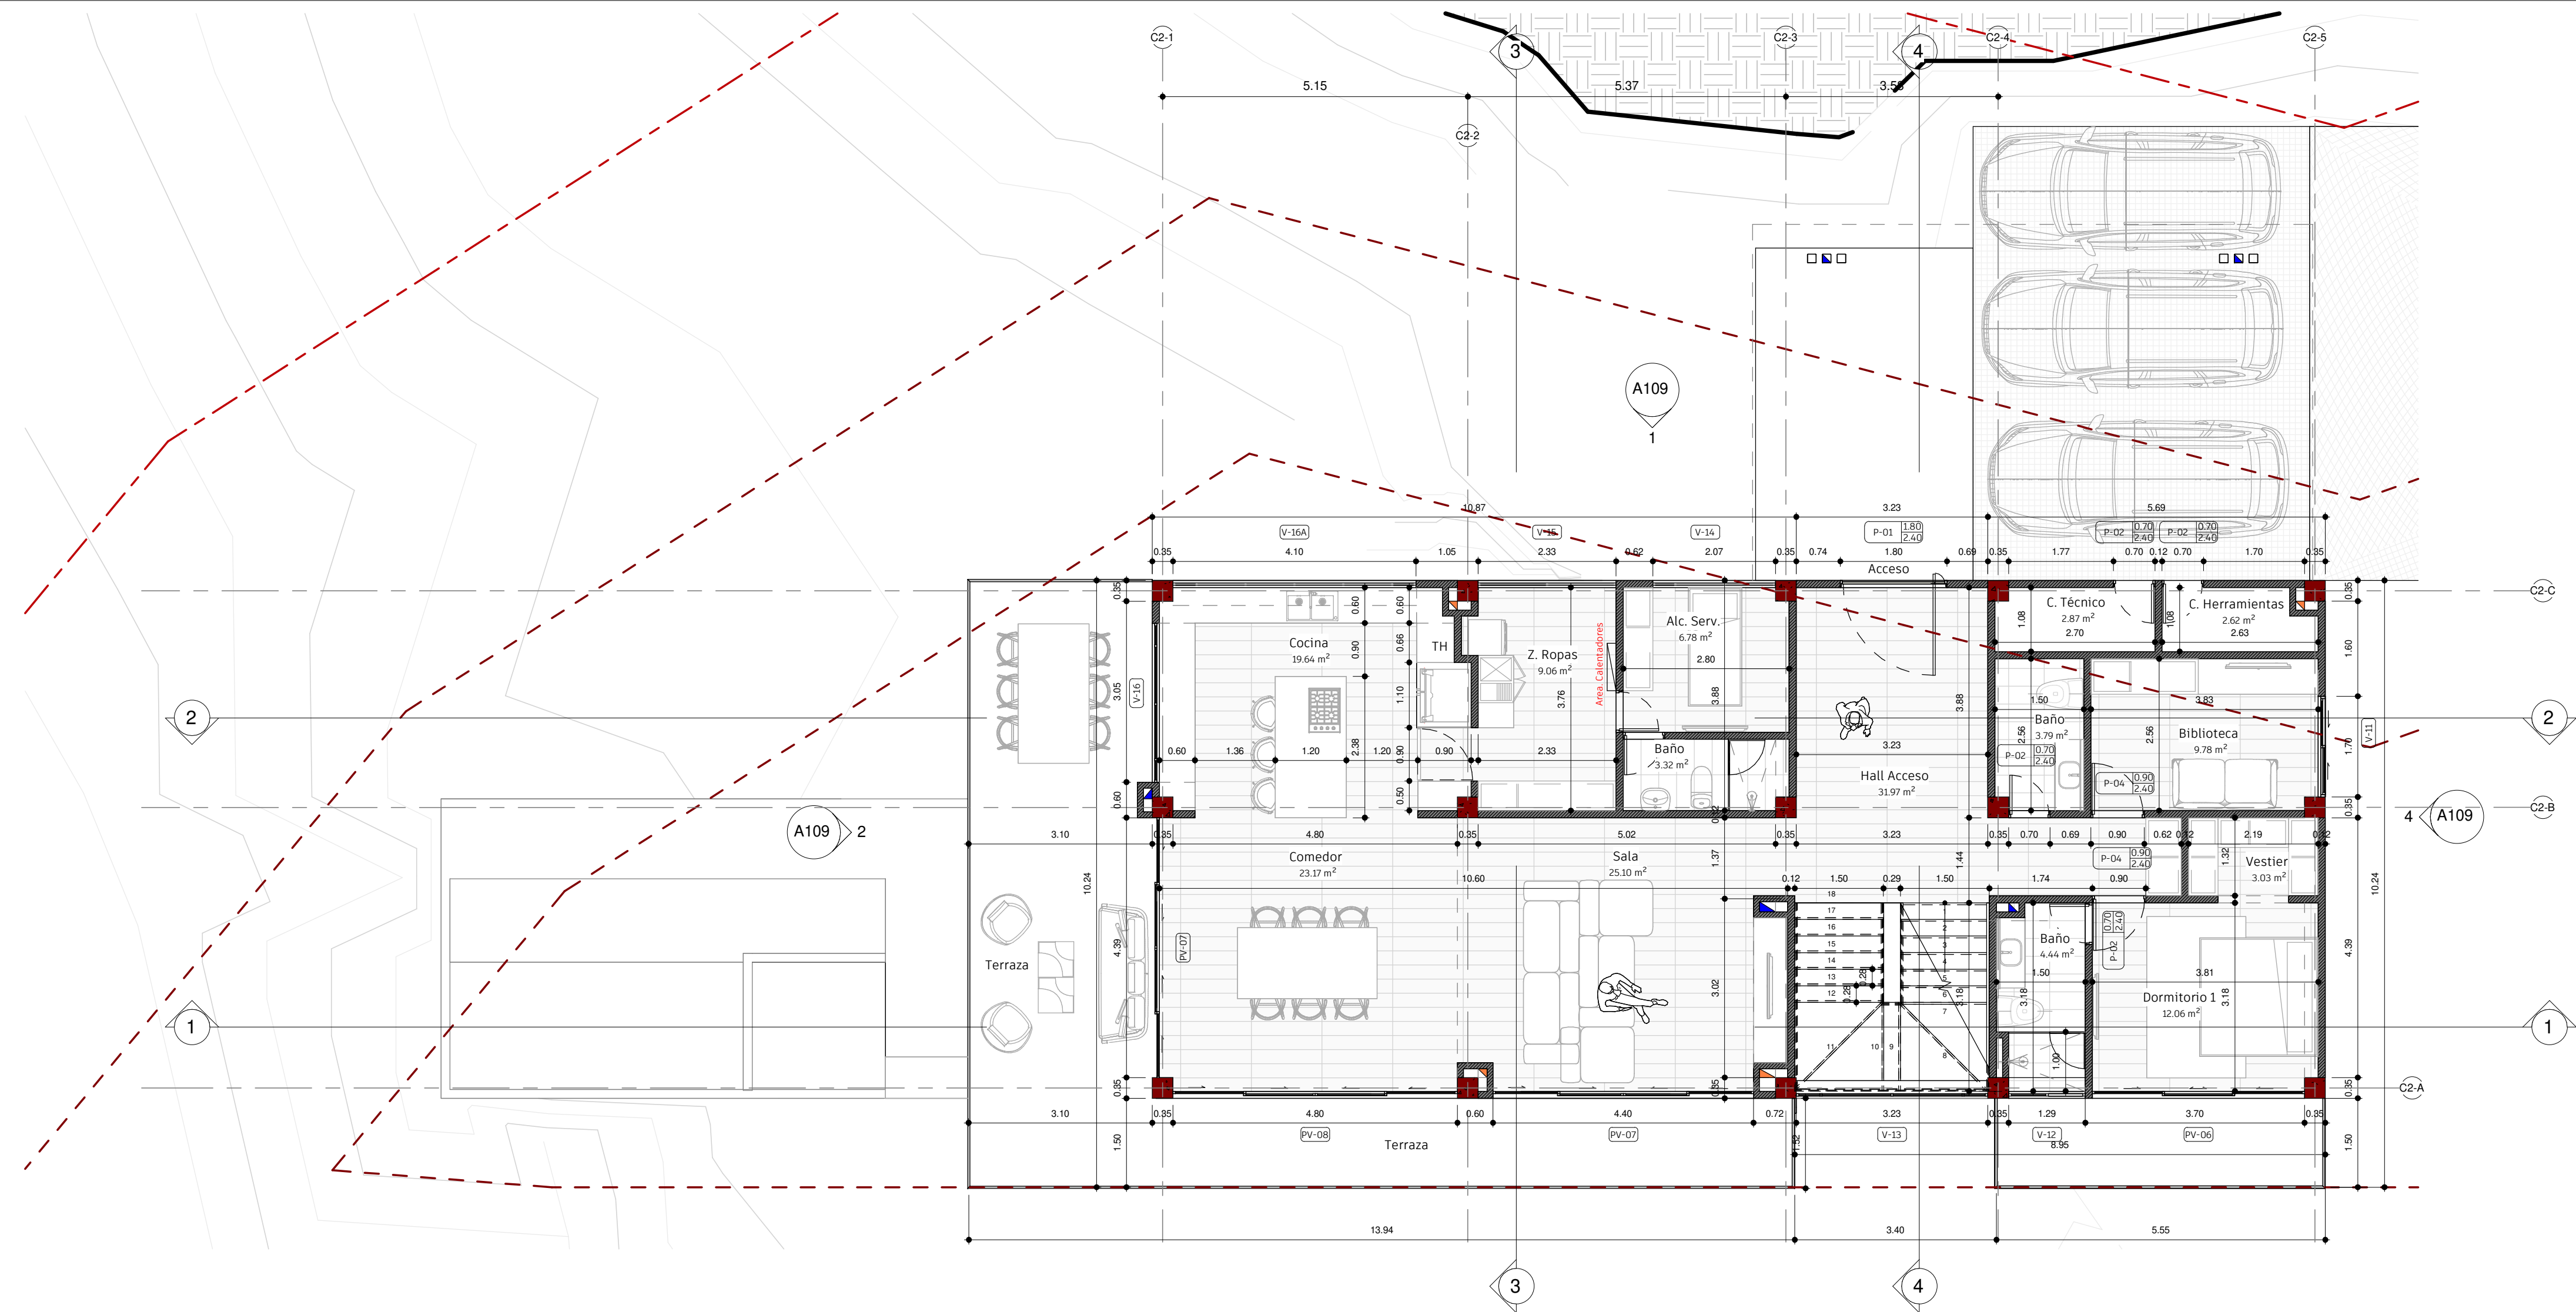
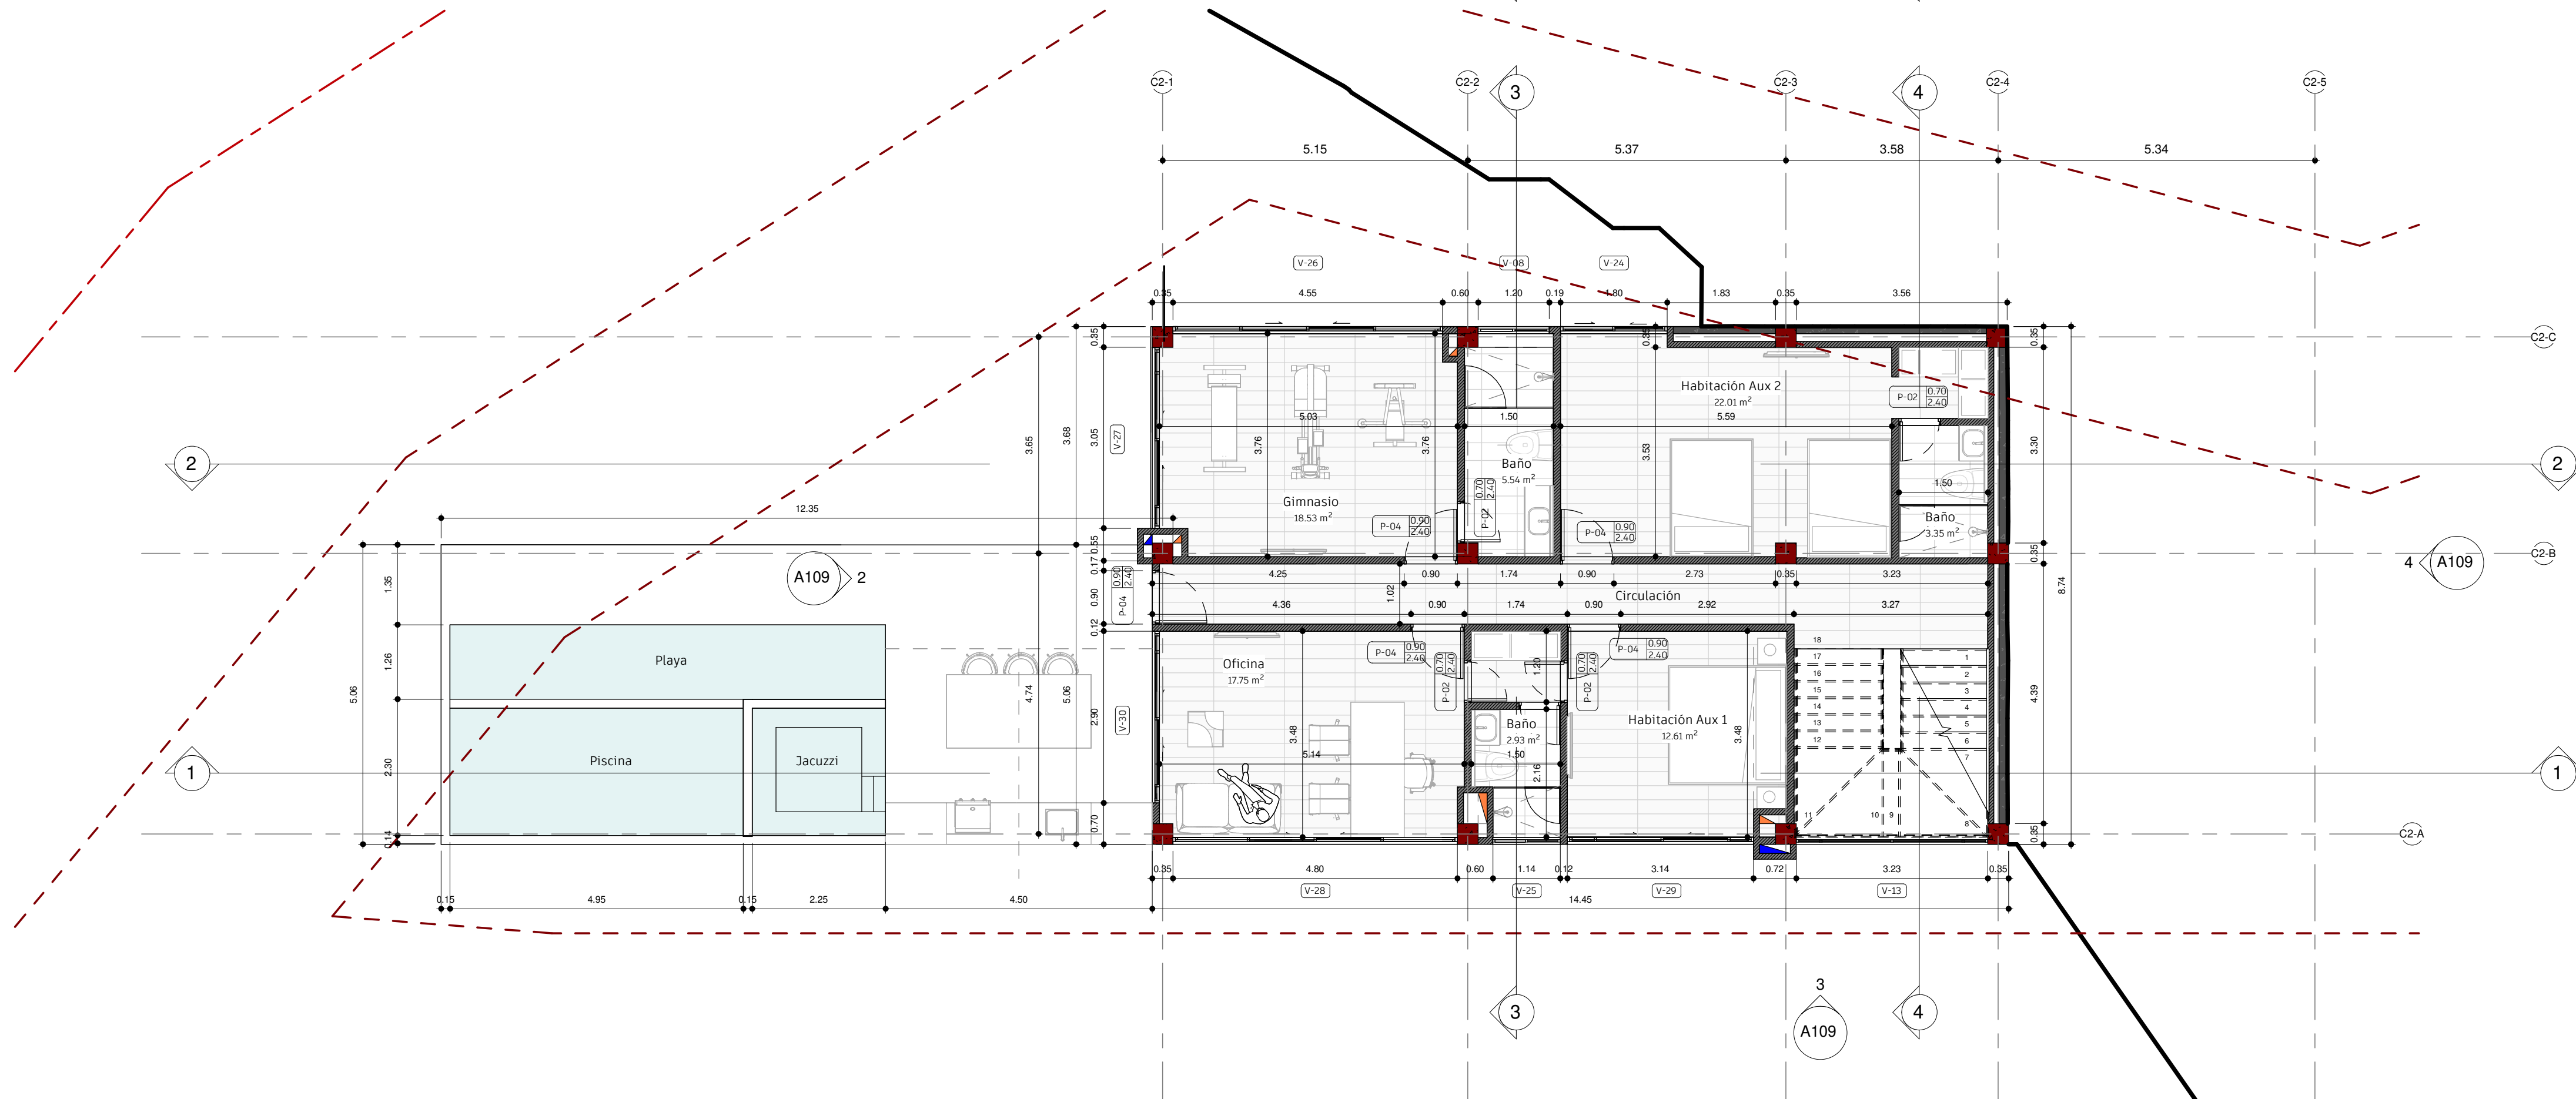
1 C1-S1
1:753 C1-S3
1:752 C1-S2
1:754 C1-S4
1:75

1 C1-FAC 1
1:752 C1-FAC 2
1:753 C1-FAC 3
1:754 C1-FAC 4
1:75

Casa Campestre
Plancha No. **A105**
LOTE No. 1 El Espigal-Envigado-Ant
Mat. 001-1416040
ARQUITECTO:

ALEJANDRO GONZÁLEZ JARAMILLO
MAT. A05402007-8359284
CONTIENE:
Casa 1 - Fachadas
ESCALA:
1:75

Este plano y su contenido, están protegidos por la ley de derechos de autor. Si el poseedor de este plano lo diseña, distribuye, copia o usa sin autorización escrita, formal y legal de STUDIO AREA S.A.S., estará violando las disposiciones de la Ley 23 de 1982, sobre derechos de autor.

1 Casa 2 P1
1:752 Casa 2 Sotano
1:75

Casa Campestre

No. 001-1416040

ARQUITECTO:

ALEJANDRO GONZÁLEZ JARAMILLO
MAT. A05402007-8359284

CONTIENE:

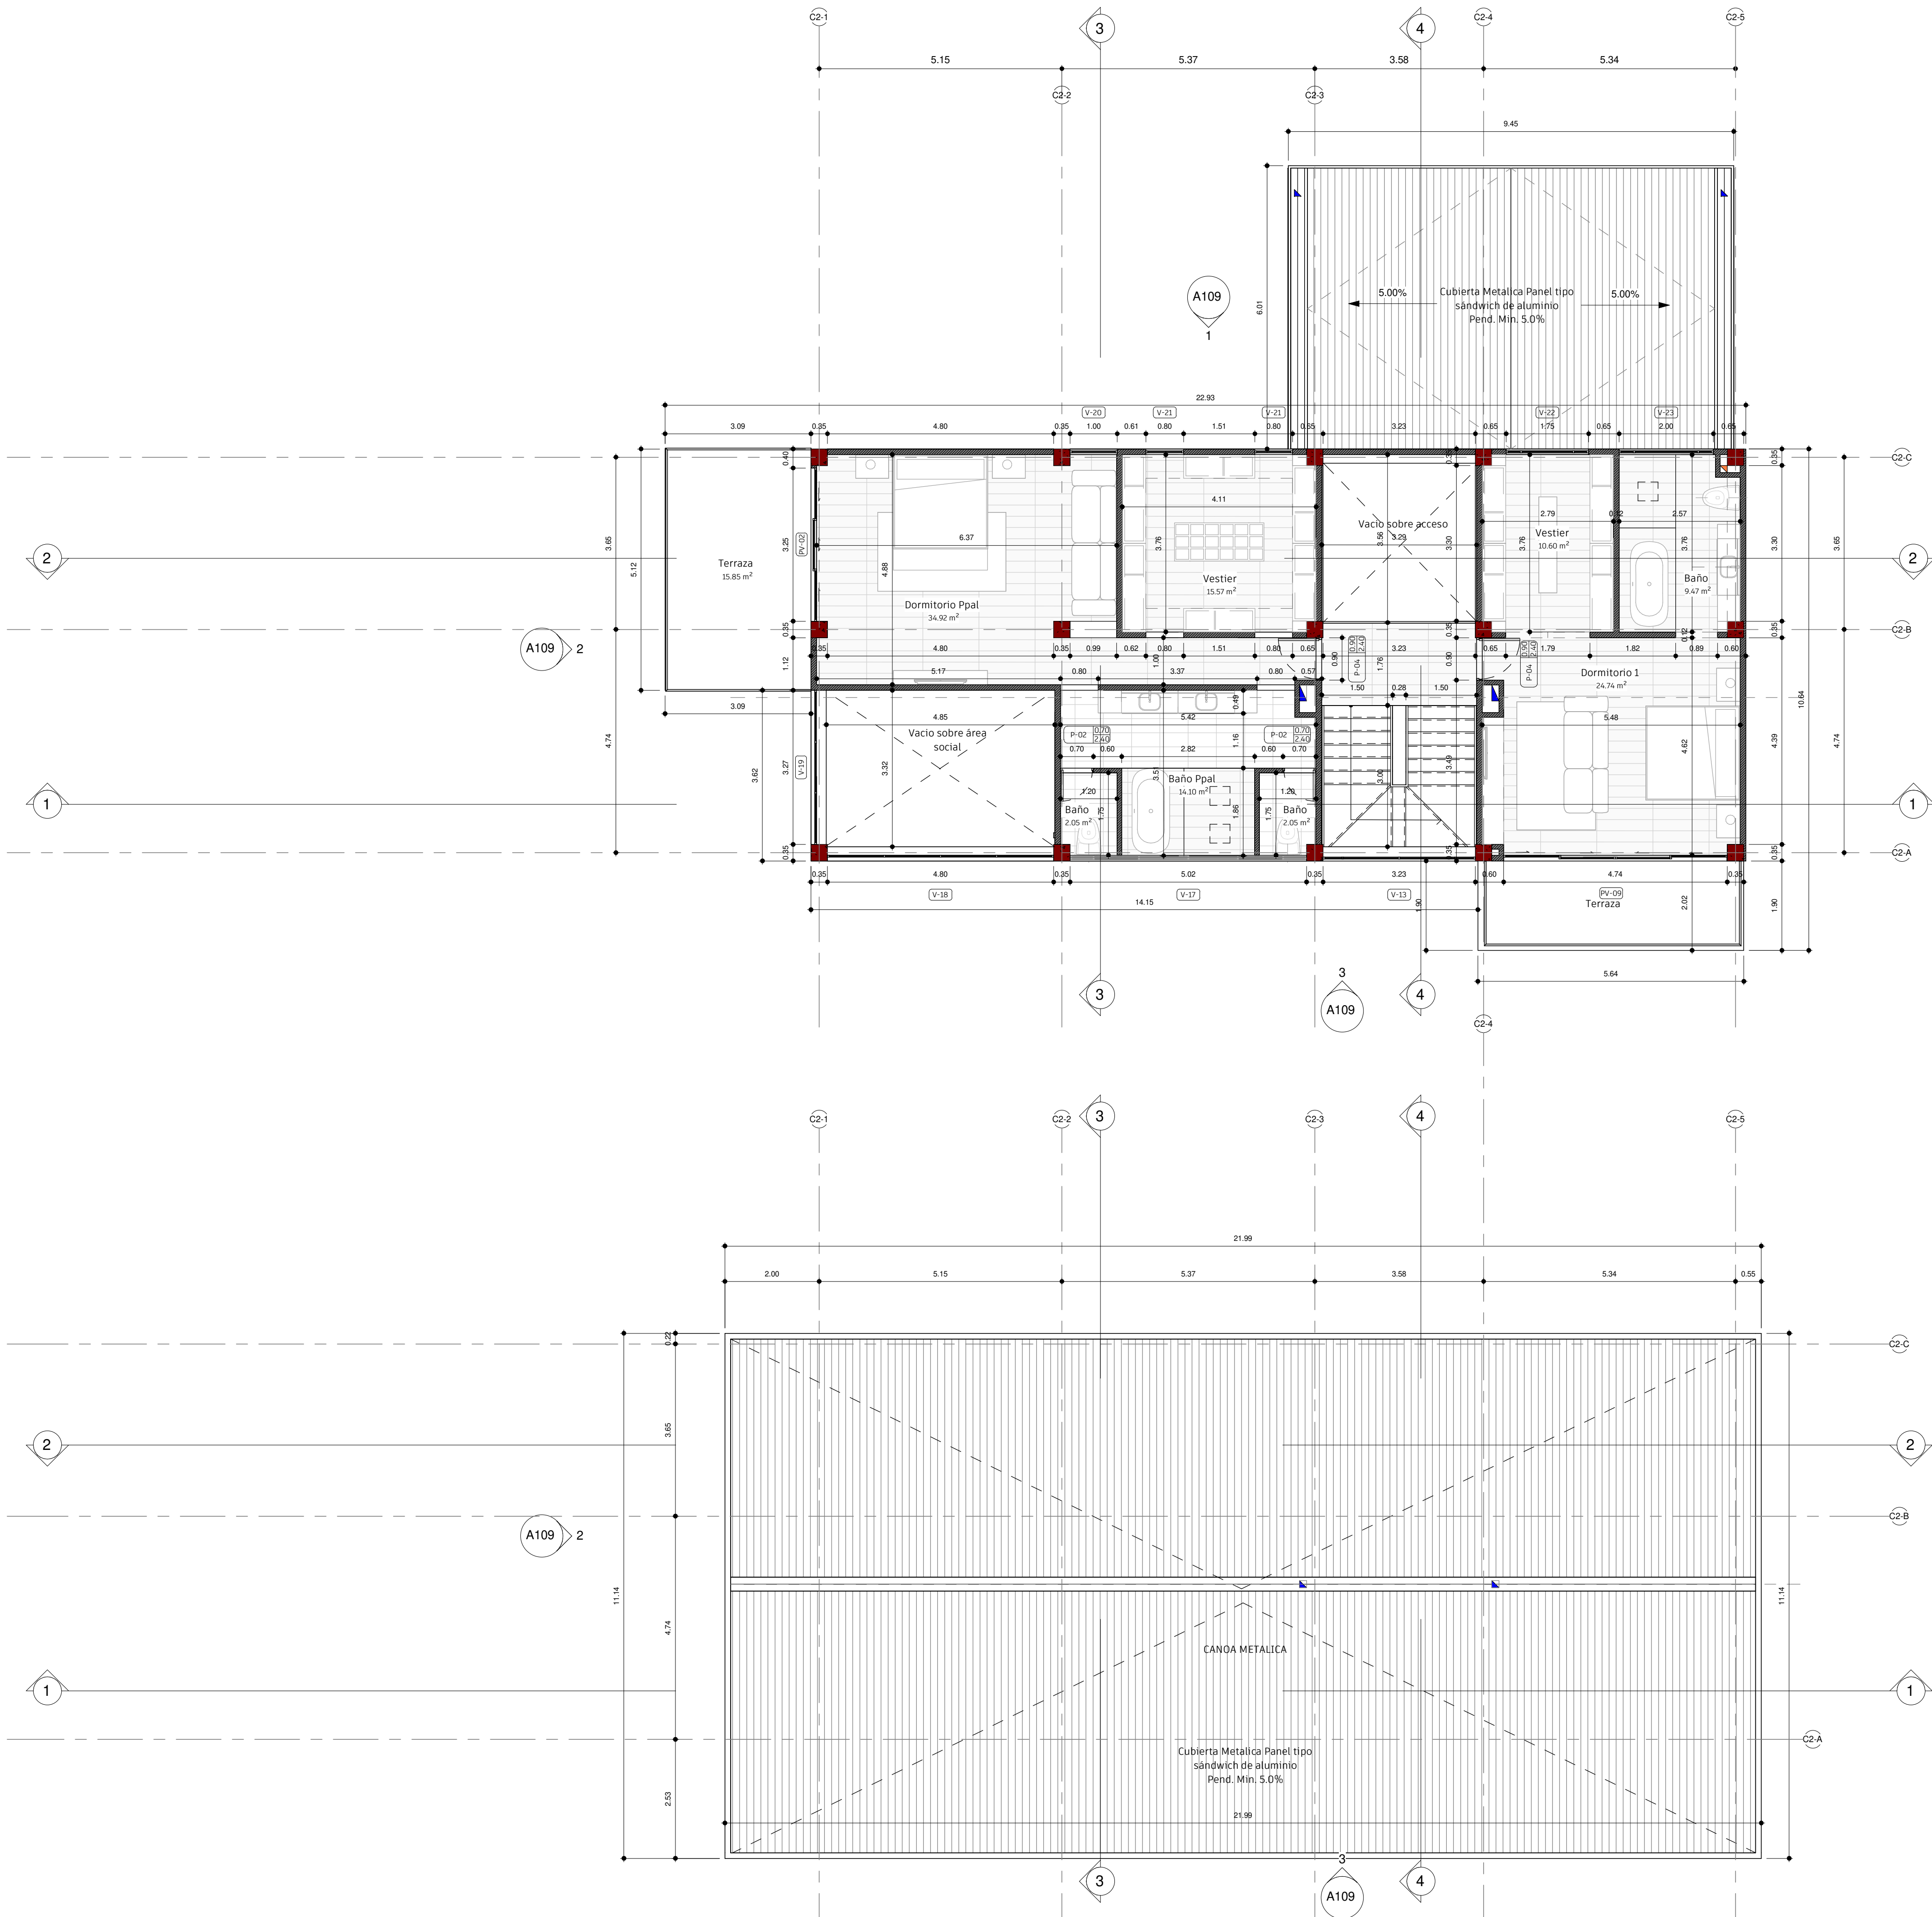
Casa 2 - Plantas

Plancha

No. A106

ESCALA:
1:75

Este plano y su contenido, están protegidos por la ley de derechos de autor. Si el poseedor de este plano lo diseña, distribuye, copia o usa sin autorización escrita, formal y legal de STUDIO AREA S.A.S., estará violando las disposiciones de la Ley 23 de 1982, sobre derechos de autor.



1 Casa 2 P2

1 : 75

2 Casa 2 Cubierta

1 : 75

Casa Campestre

Plancha No. A107

LOTE No. 1 El Espigal-Envigado-Ant

Mat. 001-1416040

ARQUITECTO:

ALEJANDRO GONZÁLEZ JARAMILLO

MAT. A05402007-8359284

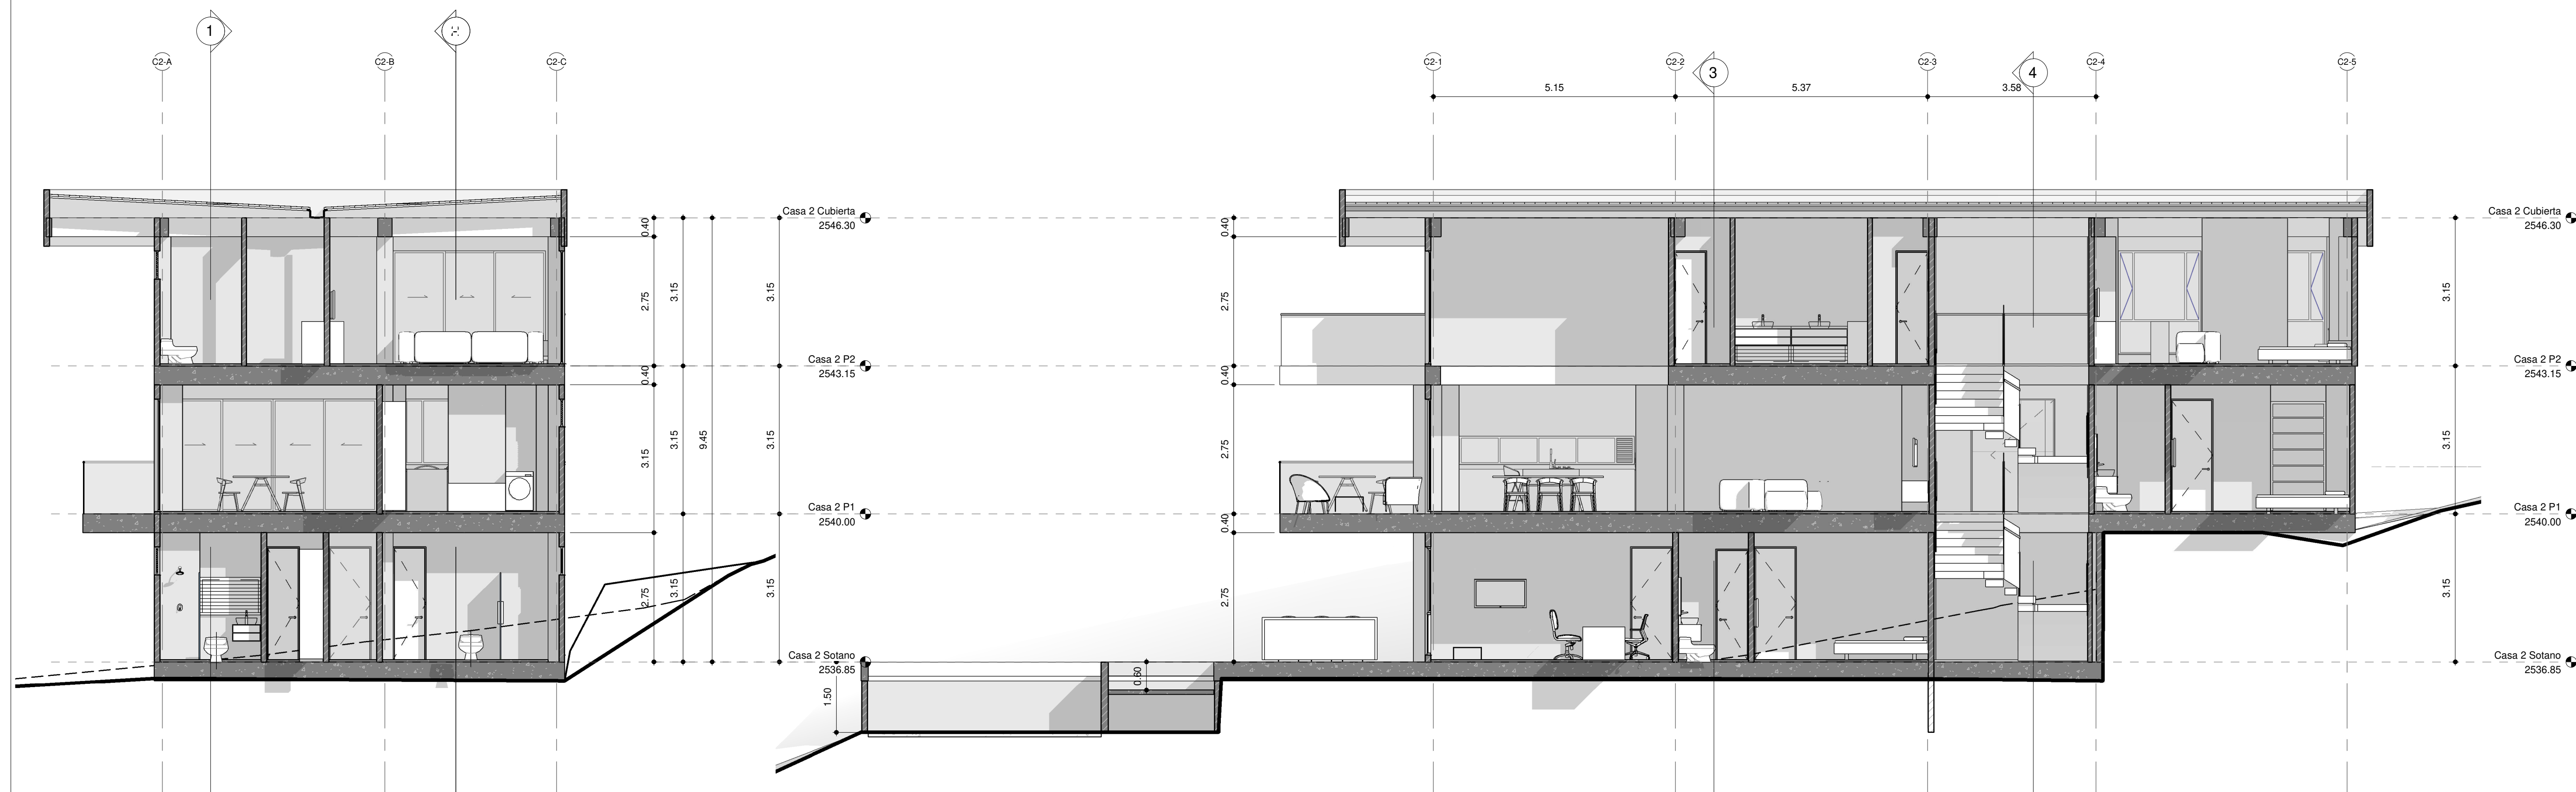
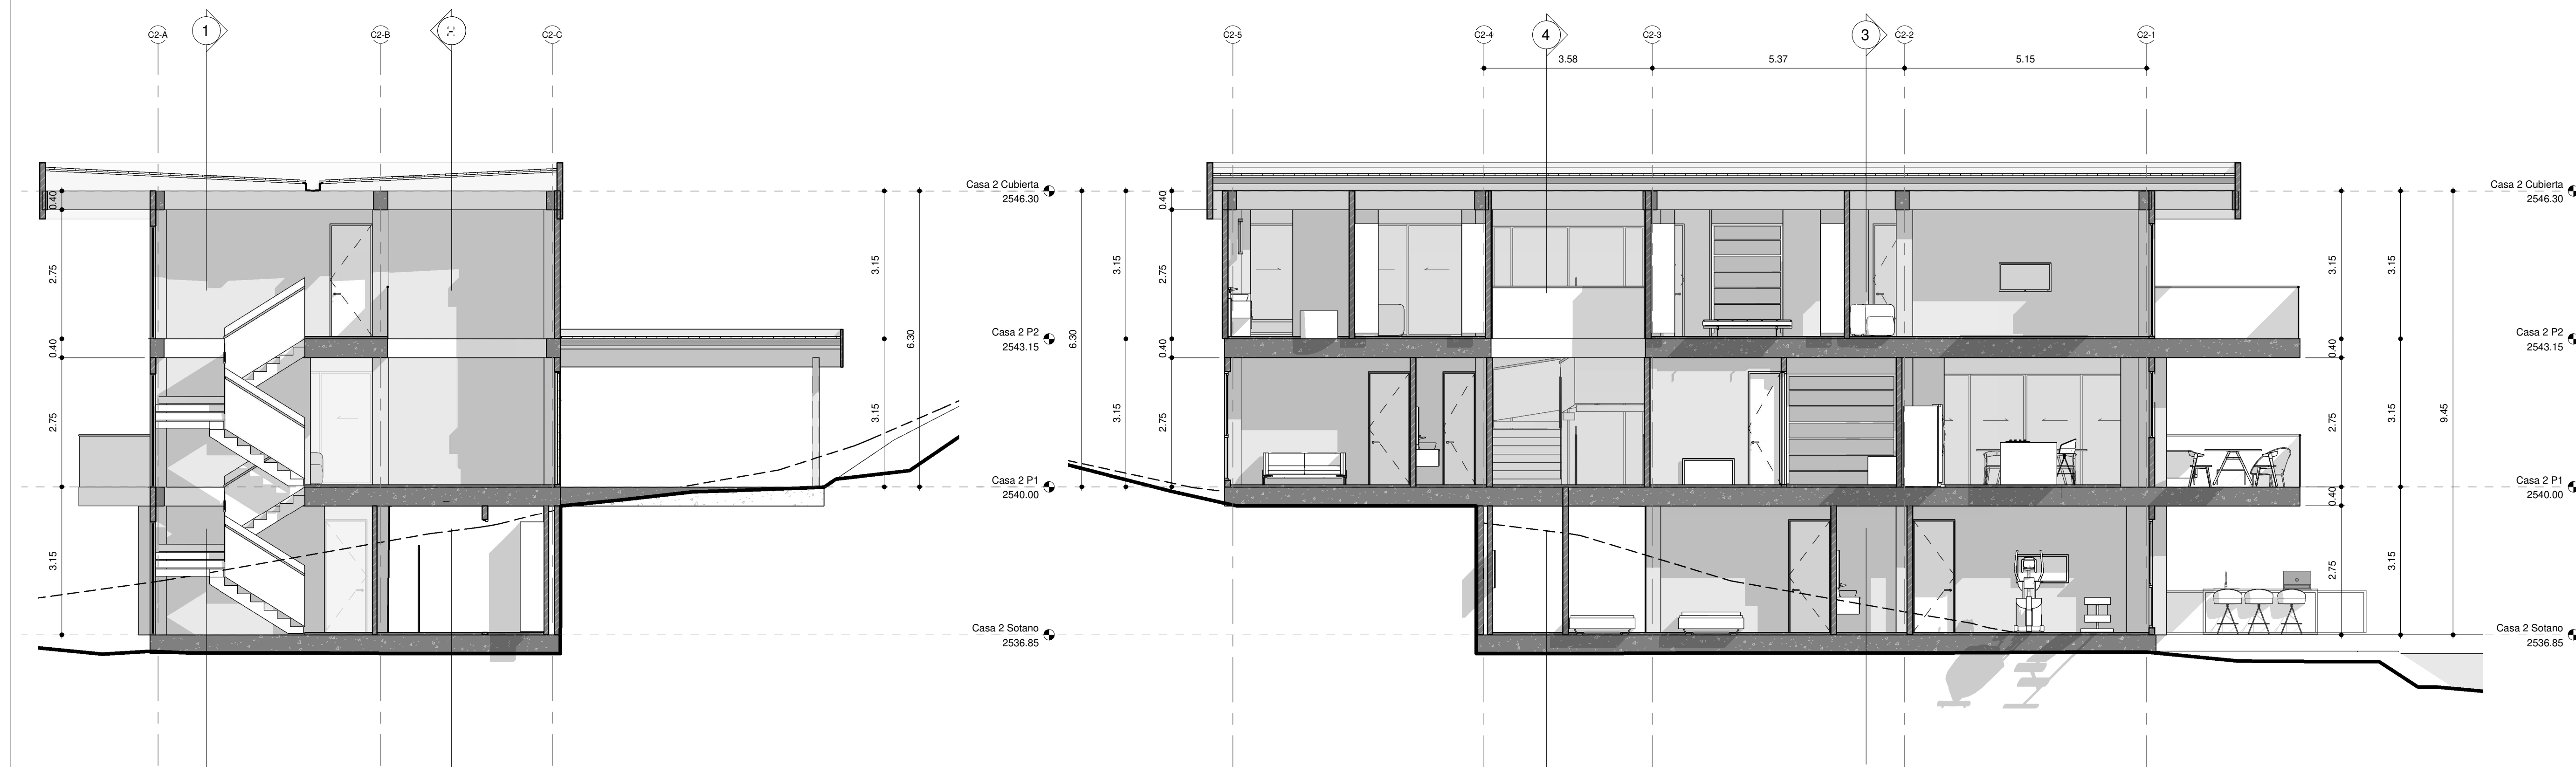
CONTIENE:

Casa 2 - Plantas

ESCALA:

1 : 75

Este plano y su contenido, están protegidos por la ley de derechos de autor. Si el poseedor de este plano lo diseña, distribuye, copia o usa sin autorización escrita, formal y legal de STUDIO AREA S.A.S., estará violando las disposiciones de la Ley 23 de 1982, sobre derechos de autor.

3 C2-S3
1:751 C2-S1
1:754 C2-S4
1:752 C2-S2
1:75

Casa Campestre

Plancha No.
LOTE No. 1 El Espigal-Envigado-Ant
Mat. 001-1416040

A108

ARQUITECTO:

ALEJANDRO GONZÁLEZ JARAMILLO
MAT. A05402007-8359284

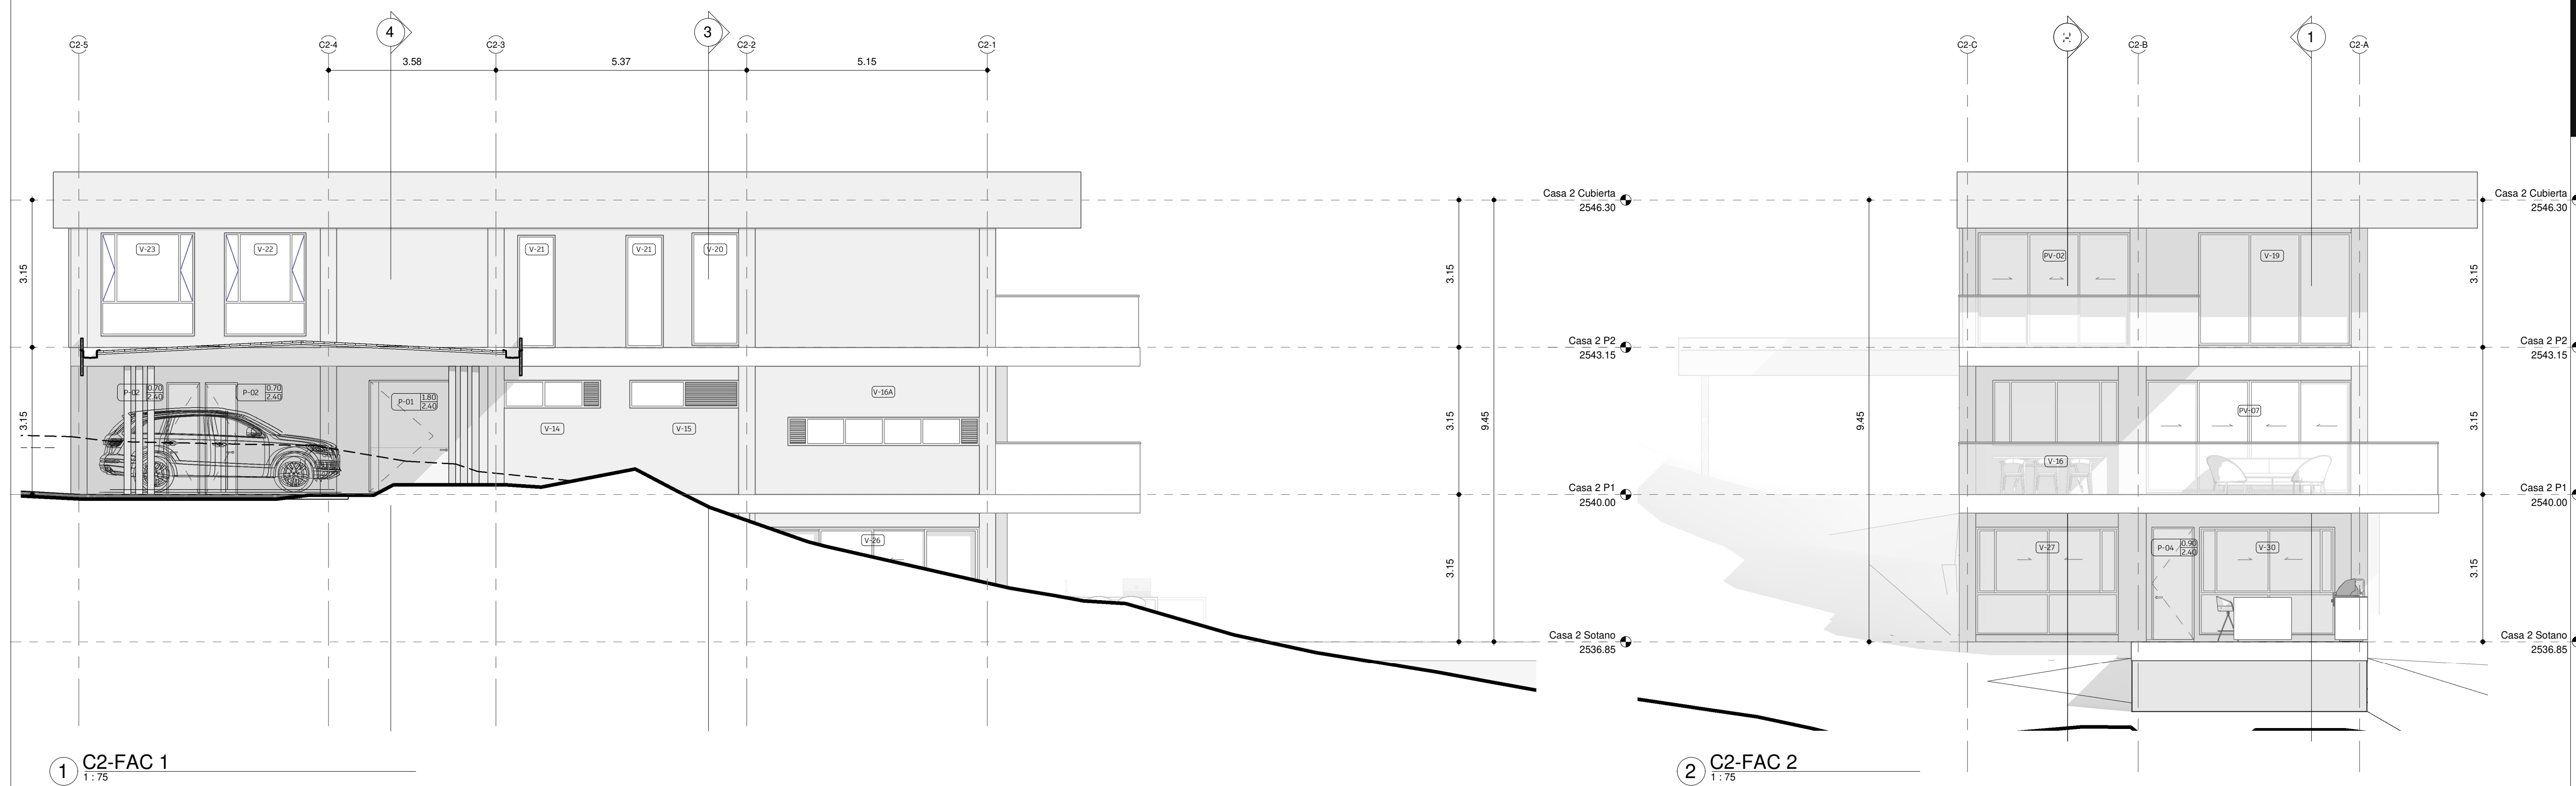
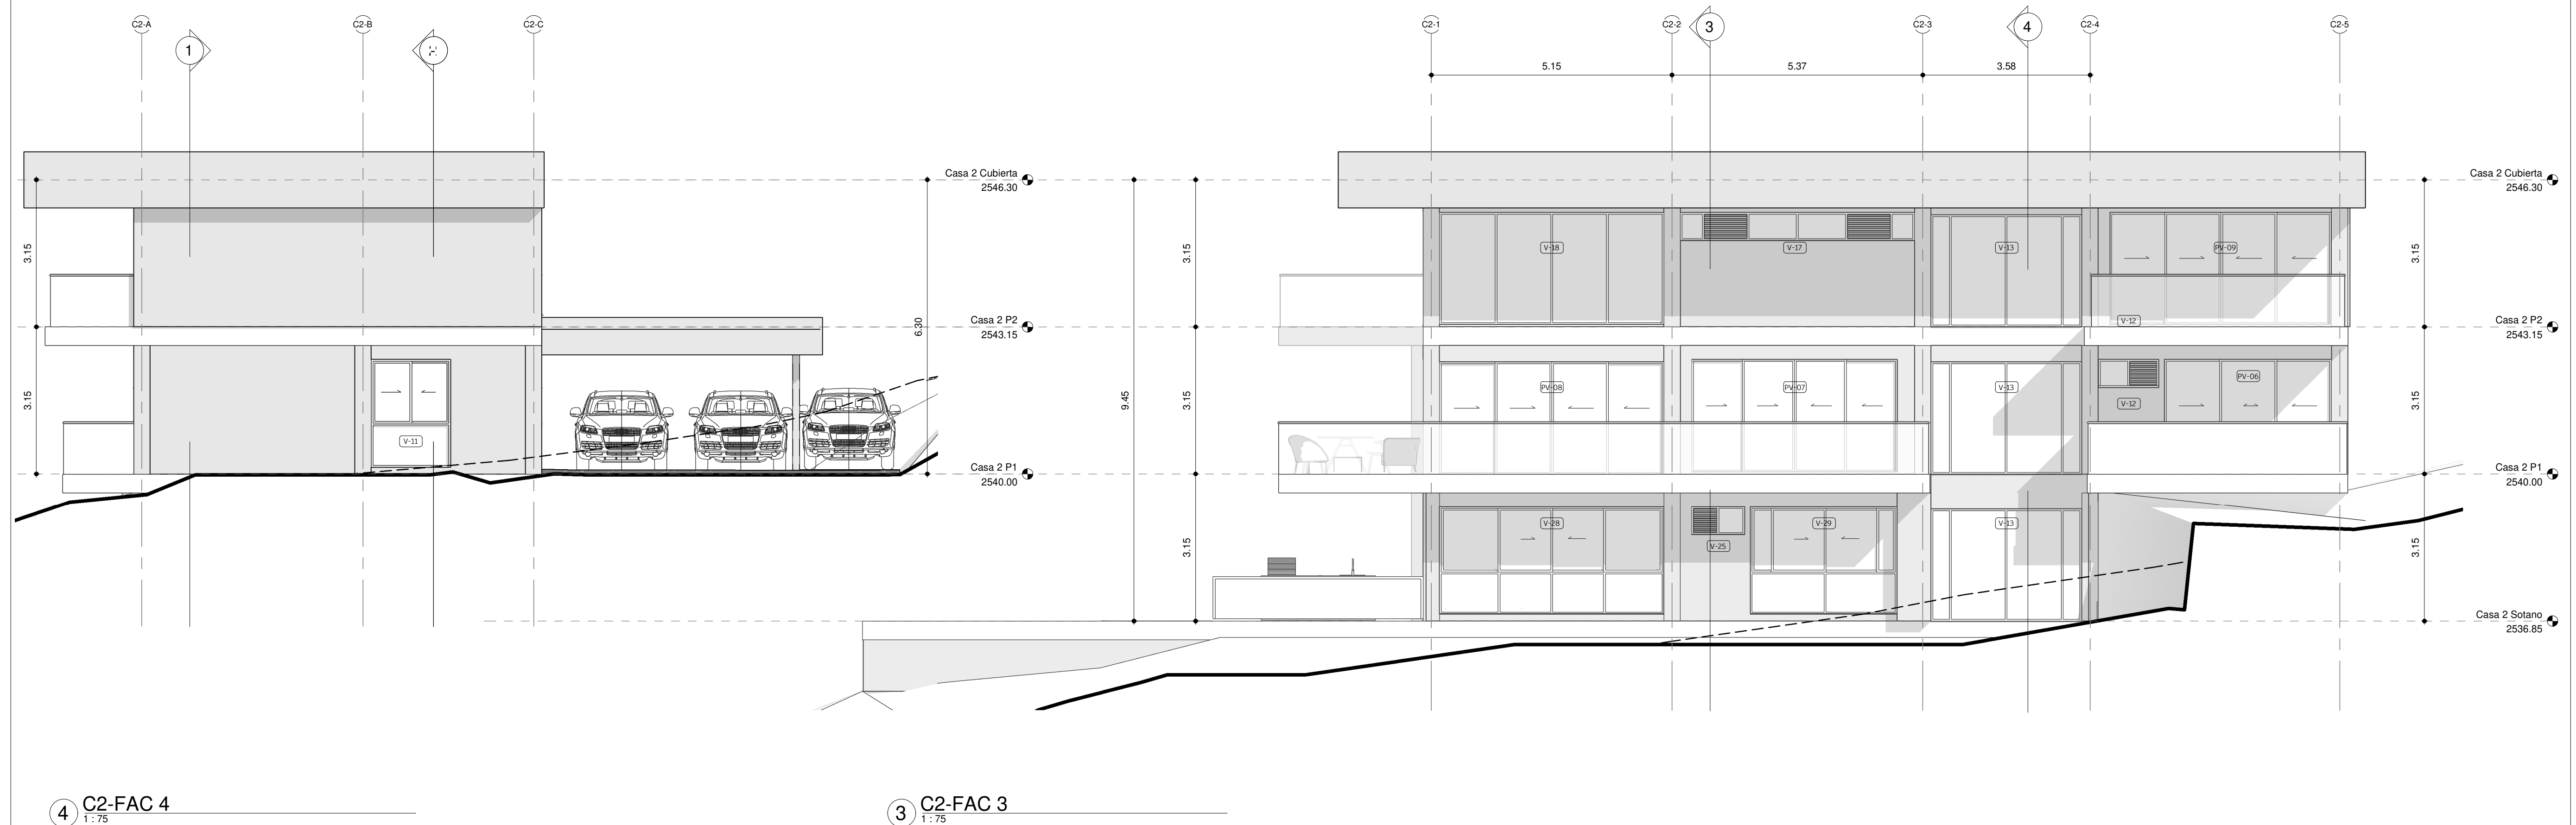
CONTIENE:

Casa 2 - Secciones

ESCALA:

1:75

Este plano y su contenido, están protegidos por la ley de derechos de autor. Si el poseedor de este plano lo diseña, distribuye, copia o usa sin autorización escrita, formal y legal de STUDIO AREA & S.A.S., estará violando las disposiciones de la Ley 23 de 1982, sobre derechos de autor.

1 C2-FAC 1
1:752 C2-FAC 2
1:754 C2-FAC 4
1:753 C2-FAC 3
1:75

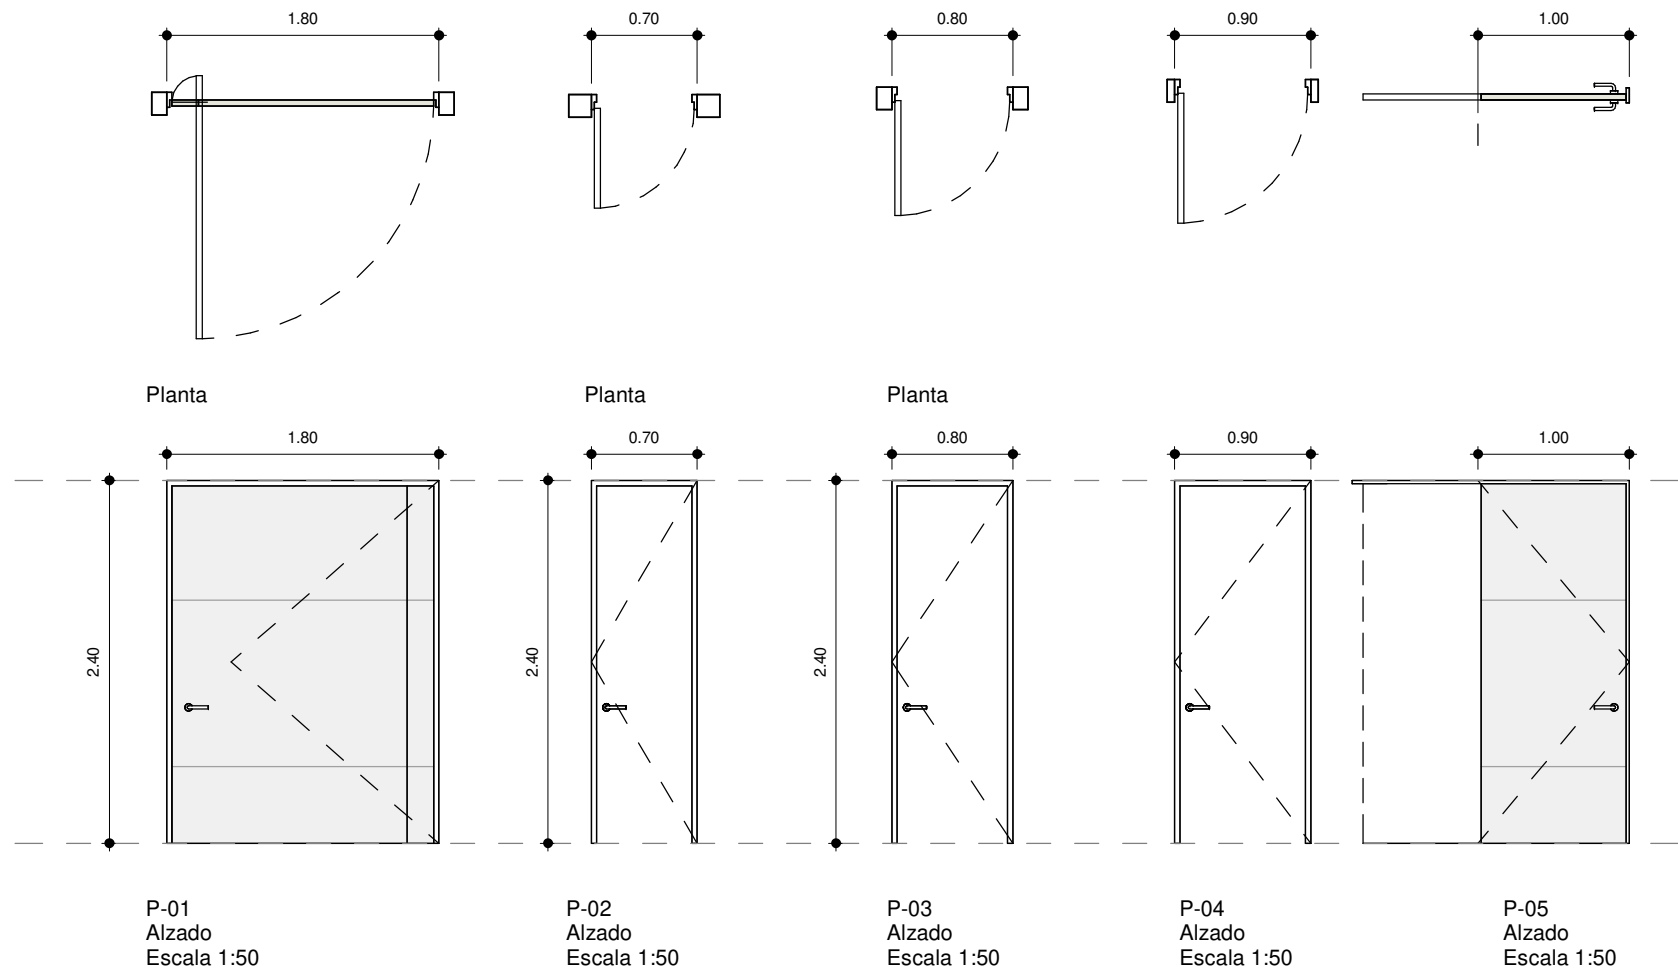


Tabla de planificación de puertas					
Marca de tipo	Alto	Ancho	Cantidad	Descripción	Nivel
P-01					
P-01	2.40	1.80	1	Puerta maciza 100% en Cedro (secada en horno), espesor 35 mm, incluye marco y cerradura.	Casa 2 P1
P-01	2.40	1.80	1	Puerta maciza 100% en Cedro (secada en horno), espesor 35 mm, incluye marco y cerradura.	Casa 1 P1
P-02					
P-02	2.40	0.70	5	Puertas Batientes en madera entamboradas compuestas por dos láminas de HDF , un bastidor (marco interno) en pino radiata con refuerzos internos para la instalación de las cerraduras, y un relleno interior de honey comb. + Juntas de 4 mm + Cerradura pomo aluminio tipo duralock.	Casa 2 Sotano
P-02	2.40	0.70	6	Puertas Batientes en madera entamboradas compuestas por dos láminas de HDF , un bastidor (marco interno) en pino radiata con refuerzos internos para la instalación de las cerraduras, y un relleno interior de honey comb. + Juntas de 4 mm + Cerradura pomo aluminio tipo duralock.	Casa 2 P1
P-02	2.40	0.70	5	Puertas Batientes en madera entamboradas compuestas por dos láminas de HDF , un bastidor (marco interno) en pino radiata con refuerzos internos para la instalación de las cerraduras, y un relleno interior de honey comb. + Juntas de 4 mm + Cerradura pomo aluminio tipo duralock.	Casa 1 P1
P-02	2.40	0.70	2	Puertas Batientes en madera entamboradas compuestas por dos láminas de HDF , un bastidor (marco interno) en pino radiata con refuerzos internos para la instalación de las cerraduras, y un relleno interior de honey comb. + Juntas de 4 mm + Cerradura pomo aluminio tipo duralock.	Casa 2 P2
P-03					
P-03	2.40	0.80	4	Puertas Batientes en madera entamboradas compuestas por dos láminas de HDF , un bastidor (marco interno) en pino radiata con refuerzos internos para la instalación de las cerraduras, y un relleno interior de honey comb. + Juntas de 4 mm + Cerradura pomo aluminio tipo duralock.	Casa 1 P2
P-04					
P-04	2.40	0.90	5	Puertas Batientes en madera entamboradas compuestas por dos láminas de HDF , un bastidor (marco interno) en pino radiata con refuerzos internos para la instalación de las cerraduras, y un relleno interior de honey comb. + Juntas de 4 mm + Cerradura pomo Aluminio Tipo Duralock.	Casa 2 Sotano
P-04	2.40	0.90	2	Puertas Batientes en madera entamboradas compuestas por dos láminas de HDF , un bastidor (marco interno) en pino radiata con refuerzos internos para la instalación de las cerraduras, y un relleno interior de honey comb. + Juntas de 4 mm + Cerradura pomo Aluminio Tipo Duralock.	Casa 2 P1
P-04	2.40	0.90	3	Puertas Batientes en madera entamboradas compuestas por dos láminas de HDF , un bastidor (marco interno) en pino radiata con refuerzos internos para la instalación de las cerraduras, y un relleno interior de honey comb. + Juntas de 4 mm + Cerradura pomo Aluminio Tipo Duralock.	Casa 1 P1
P-04	2.40	0.90	2	Puertas Batientes en madera entamboradas compuestas por dos láminas de HDF , un bastidor (marco interno) en pino radiata con refuerzos internos para la instalación de las cerraduras, y un relleno interior de honey comb. + Juntas de 4 mm + Cerradura pomo Aluminio Tipo Duralock.	Casa 2 P2
P-04	2.40	0.90	3	Puertas Batientes en madera entamboradas compuestas por dos láminas de HDF , un bastidor (marco interno) en pino radiata con refuerzos internos para la instalación de las cerraduras, y un relleno interior de honey comb. + Juntas de 4 mm + Cerradura pomo Aluminio Tipo Duralock.	Casa 1 P2
P-05					
P-05	2.40	1.00	1	Puertas Corredizas en madera entamboradas compuestas por dos láminas de HDF , un bastidor (marco interno) en pino radiata con refuerzos internos para la instalación de las cerraduras, y un relleno interior de honey comb. + Juntas de 4 mm + Cerradura pomo a	Casa 1 P2

40

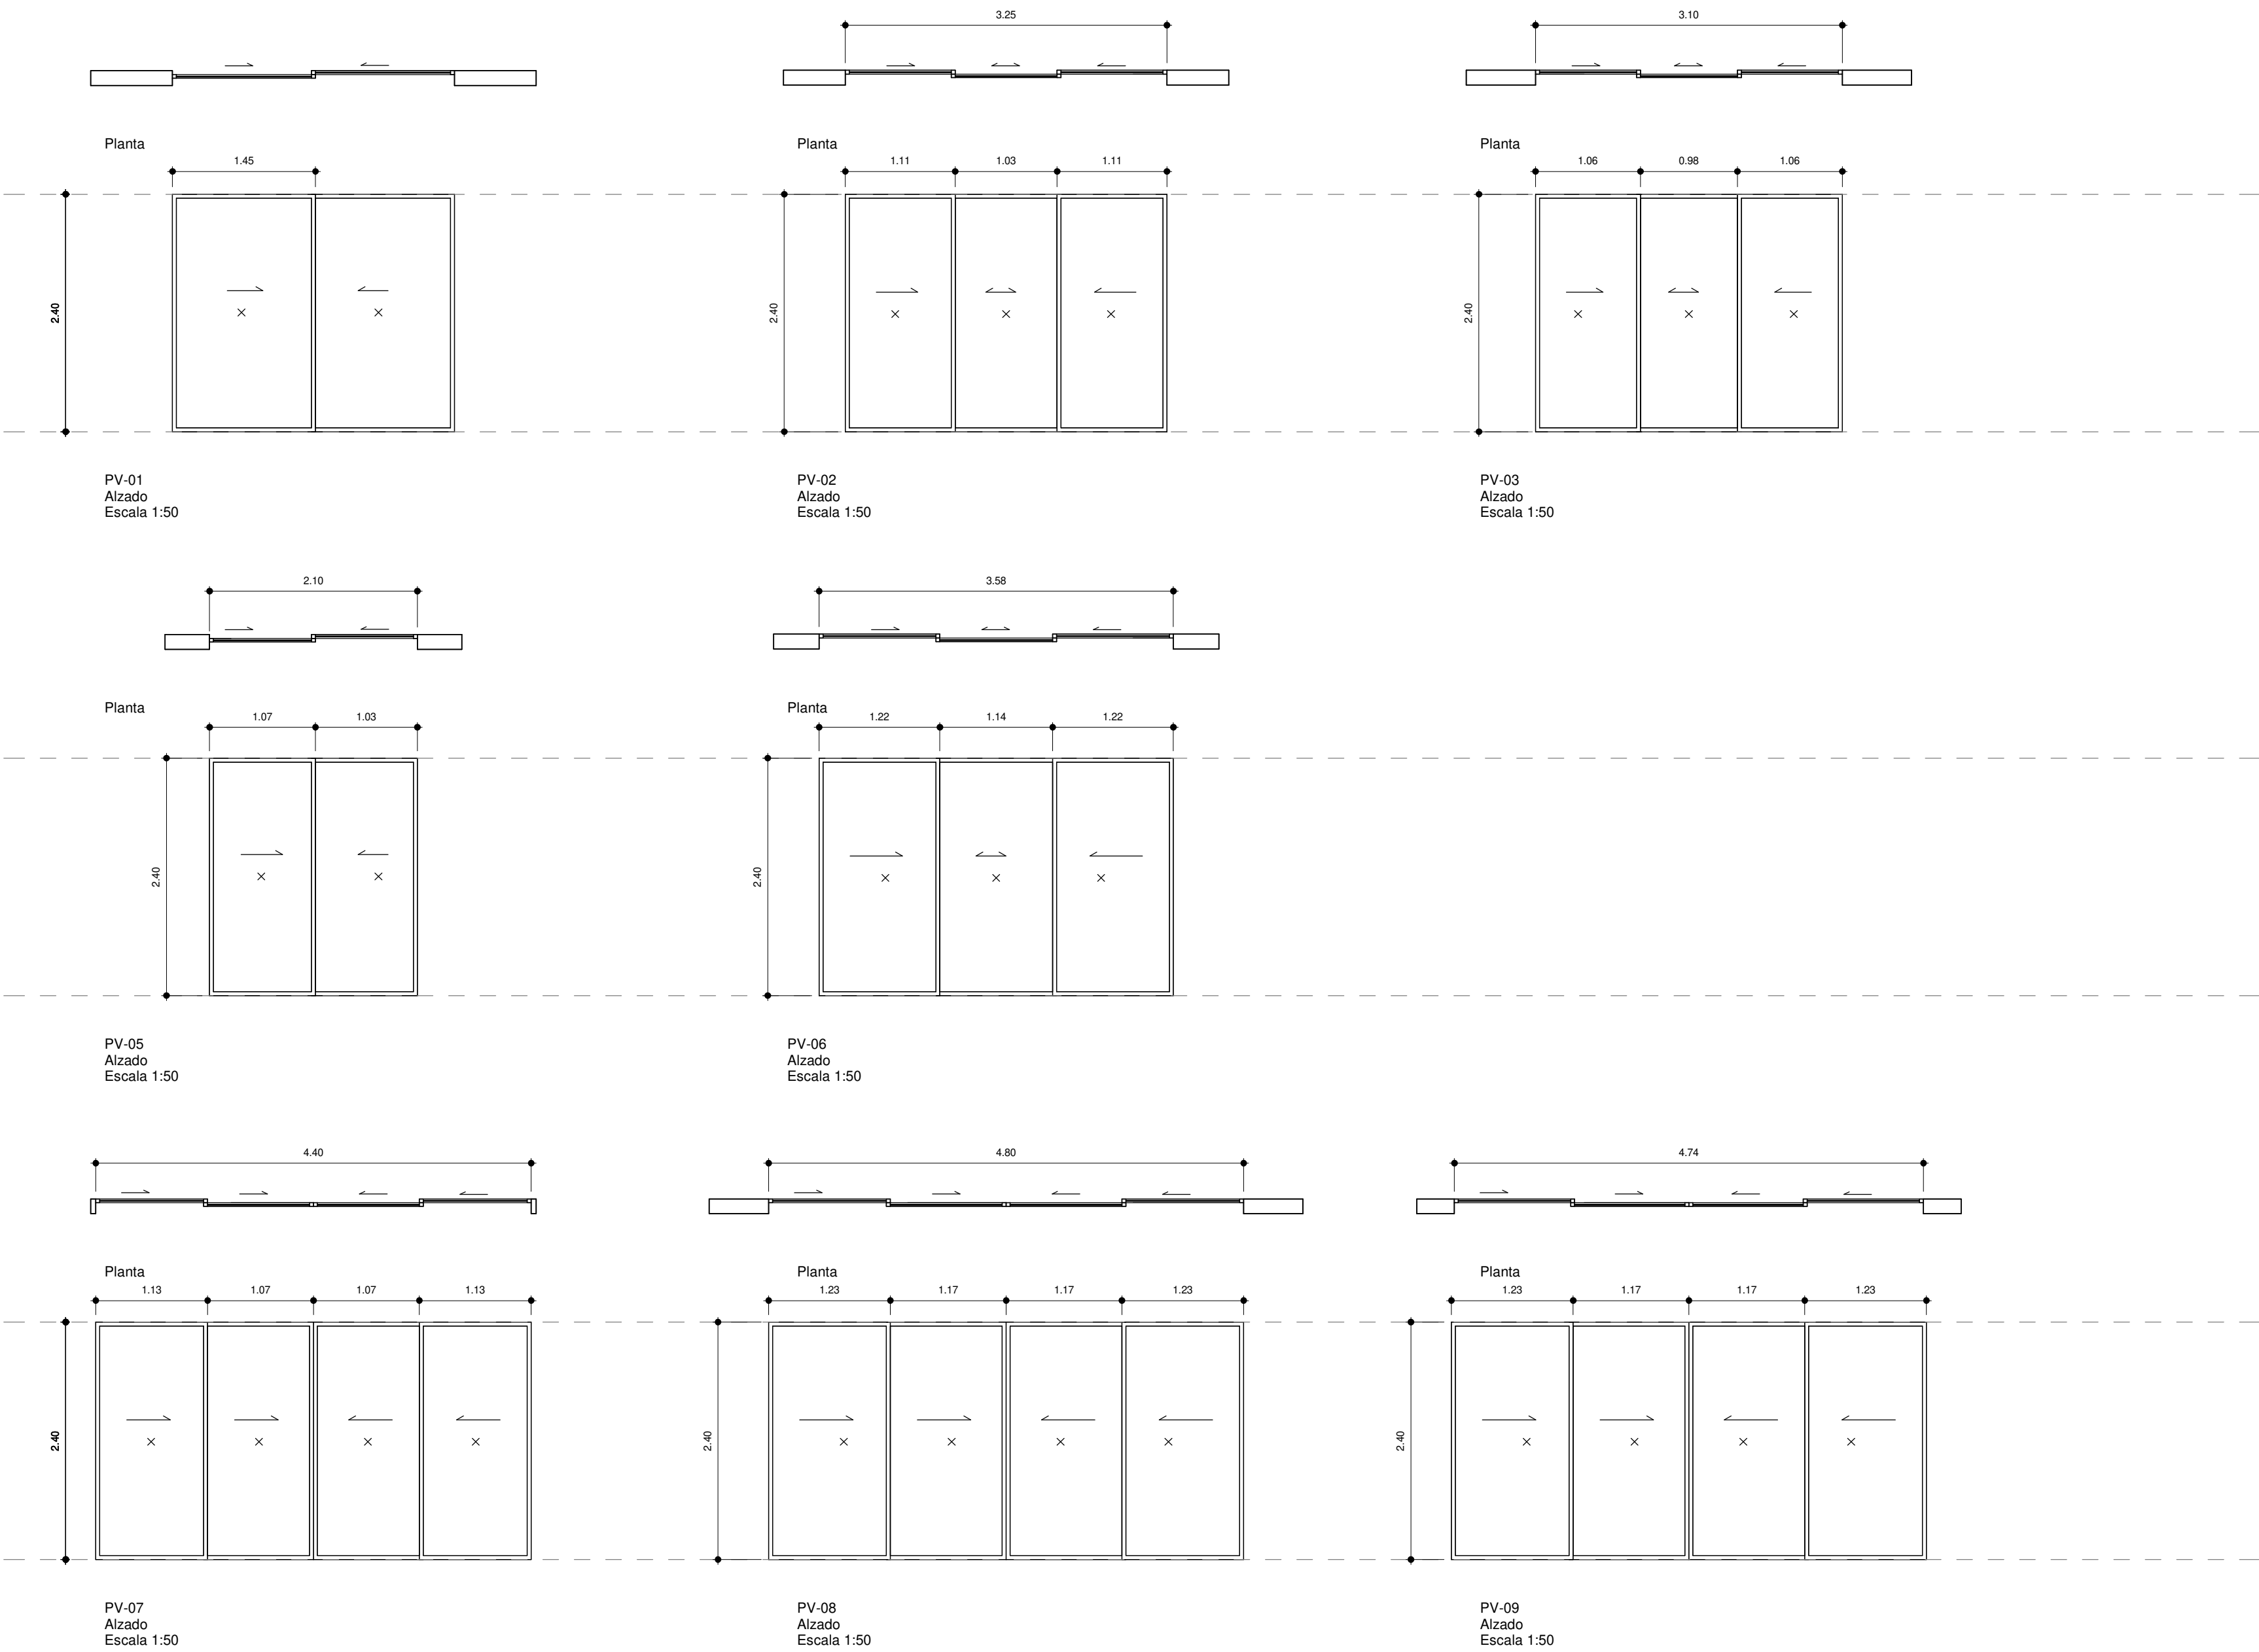


Tabla de planificación de Puertas Vidrieras					
Marca de tipo	Anchura	Altura	Cantidad	Nivel	Descripción
PV-01					
PV-01	2.85	2.40	1	Casa 1 P1	Puerta vidriera en sistema deslizante con marco en 2 pistas y montaje a 2 naves deslizantes con rodamientos abb teflonados, marco 7038 en color negro y cubierta en vidrio templado de 6mm incoloro con chapas overseas y manijas de armar, sellos externos en sika 1a multipropósito.
PV-02					
PV-02	3.25	2.40	1	Casa 1 P1	Puerta vidriera en sistema deslizante con marco en 2 pistas y montaje a 3 naves deslizantes con rodamientos abb teflonados, marco 7038 en color negro y cubierta en vidrio templado de 6mm incoloro con chapas overseas y manijas de armar, sellos externos en sika 1a multipropósito.
PV-02	3.25	2.40	1	Casa 1 P2	Puerta vidriera en sistema deslizante con marco en 2 pistas y montaje a 3 naves deslizantes con rodamientos abb teflonados, marco 7038 en color negro y cubierta en vidrio templado de 6mm incoloro con chapas overseas y manijas de armar, sellos externos en sika 1a multipropósito.
PV-02	3.25	2.40	1	Casa 2 P2	Puerta vidriera en sistema deslizante con marco en 2 pistas y montaje a 3 naves deslizantes con rodamientos abb teflonados, marco 7038 en color negro y cubierta en vidrio templado de 6mm incoloro con chapas overseas y manijas de armar, sellos externos en sika 1a multipropósito.
PV-03					
PV-03	3.10	2.40	1	Casa 1 P2	Puerta vidriera en sistema deslizante con marco en 2 pistas y montaje a 3 naves deslizantes con rodamientos abb teflonados, marco 7038 en color negro y cubierta en vidrio templado de 6mm incoloro con chapas overseas y manijas de armar, sellos externos en sika 1a multipropósito.
PV-05					
PV-05	2.10	2.40	1	Casa 1 P2	Puerta vidriera en sistema deslizante con marco en 2 pistas y montaje a 2 naves deslizantes con rodamientos abb teflonados, marco 7038 en color negro y cubierta en vidrio templado de 6mm incoloro con chapas overseas y manijas de armar, sellos externos en sika 1a multipropósito.
PV-06					
PV-06	3.58	2.40	1	Casa 2 P1	Puerta vidriera en sistema deslizante con marco en 2 pistas y montaje a 3 naves deslizantes con rodamientos abb teflonados, marco 7038 en color negro y cubierta en vidrio templado de 6mm incoloro con chapas overseas y manijas de armar, sellos externos en sika 1a multipropósito.
PV-07					
PV-07	4.40	2.40	1	Casa 2 P1	Puerta vidriera en sistema deslizante con marco en 2 pistas y montaje a 4 naves deslizantes con rodamientos abb teflonados, marco 7038 en color negro y cubierta en vidrio templado de 6mm incoloro con chapas overseas y manijas de armar, sellos externos en sika 1a multipropósito.
PV-07	4.40	2.40	1	Casa 2 P1	Puerta vidriera en sistema deslizante con marco en 2 pistas y montaje a 4 naves deslizantes con rodamientos abb teflonados, marco 7038 en color negro y cubierta en vidrio templado de 6mm incoloro con chapas overseas y manijas de armar, sellos externos en sika 1a multipropósito.
PV-08					
PV-08	4.80	2.40	1	Casa 2 P1	Puerta vidriera en sistema deslizante con marco en 2 pistas y montaje a 4 naves deslizantes con rodamientos abb teflonados, marco 7038 en color negro y cubierta en vidrio templado de 6mm incoloro con chapas overseas y manijas de armar, sellos externos en sika 1a multipropósito.
PV-09					
PV-09	4.74	2.40	1	Casa 2 P2	Puerta vidriera en sistema deslizante con marco en 2 pistas y montaje a 4 naves deslizantes con rodamientos abb teflonados, marco 7038 en color negro y cubierta en vidrio templado de 6mm incoloro con chapas overseas y manijas de armar, sellos externos en sika 1a multipropósito.
Total general			11		

NOTAS IMPORTANTES: INSUMOS COMO ENTREGA DEFINITIVA VÁLIDOS PARA CONSTRUCCIÓN.

El predimensionamiento será responsabilidad del fabricante y la cantidad deberá ser ratificada por el mismo. Los tamaños de varcos se rectificarán en obra, previa colocación de la estructura. Las dimensiones establecidas en los planos de detalles deberán conservarse.

El Diseñador no se hace responsable de modificaciones y/o enmendaduras realizadas por otros, sobre planos entregados. Por tal motivo manifestamos que únicamente serán válidos los planos originales o copia de ellos, que presentan las firmas de los profesionales que intervinieron en la ejecución del proyecto, las cuales aparecen en las casillas Proyectista, Desarrolló, Revisó y/o quien presentó a Curaduría; documentos que deberán ser idénticos a las copias que reposan en nuestros archivos.

Todos los elementos que no están consignados en estos planos o en los planos de proyectos técnicos no son responsabilidad del equipo profesional de diseñadores del proyecto. El constructor debe garantizar que todos los elementos de construcción cumplan con un nivel de desempeño II (Superior) según lo exigido por la norma NBR-10 / capítulo A.9 elementos no estructurales. Todos los elementos que requieren de solución estructural harán parte del proyecto estructural diseñado por el ingeniero a cargo. La información y soluciones que no se han consignado en los cortes de detalle y que corresponden a elementos no estructurales que se les deba dar solución estructural se deberán solucionar en comité de proyecto y quedar consignados en el libro oficial de obra o similar.

Todos los cambios que se susciten o surjan en el proceso de construcción, deberán ser consultados y aprobados por el arquitecto responsable y la interventoría a cargo. De ser necesario se construirán prototipos. El constructor elaborará planos de detalles de formalistas para los elementos de concreto a la vista y planos de taller del mobiliario y de los detalles especiales, tipo estructuras metálicas. Todos los muros cerámicos o cerámicos a losa, sometidos a la intemperie deberán ser tratados con material Hidrotégu. Hidrotégu y/o simla en superficies horizontales. Las muestras deberán contar con la aprobación del Arquitecto Diseñador y la Interventoría y deberán incluir salvaguardas y garantías de estabilidad, duración, estanqueidad etc., así como los exigidos por el contratista relacionados con plazos de entrega y sustitución de piezas o partes que presenten defectos en su fabricación o puesta en obra.

Todos los elementos de concreto visto deberán llevar las aristas rectas y esquinas con ochave de 1 x 1 cm.

Cuando se presenten dudas o alternativas en el diseño o ejecución de cualquiera de los detalles previstos, estas deberán ser dirimidas con la aprobación de los Arquitectos diseñadores y constarán en el acta de comité, la aprobación de la Interventoría.

Es responsabilidad de los diseñadores técnicos, de la supervisión técnica, y de los proveedores, fabricantes o instaladores de los elementos no estructurales del edificio, suministrar al arquitecto diseñador la información requerida para complementar la coordinación de los diseños, previo a la aplicación de obra (Según N.S.R.2010).



Casa Campestre

Plancha No. **A110**

LOTE No. 1 El Espigal-Envigado-Ant

Mat. 001-1416040

ARQUITECTO:

ALEJANDRO GONZÁLEZ JARAMILLO

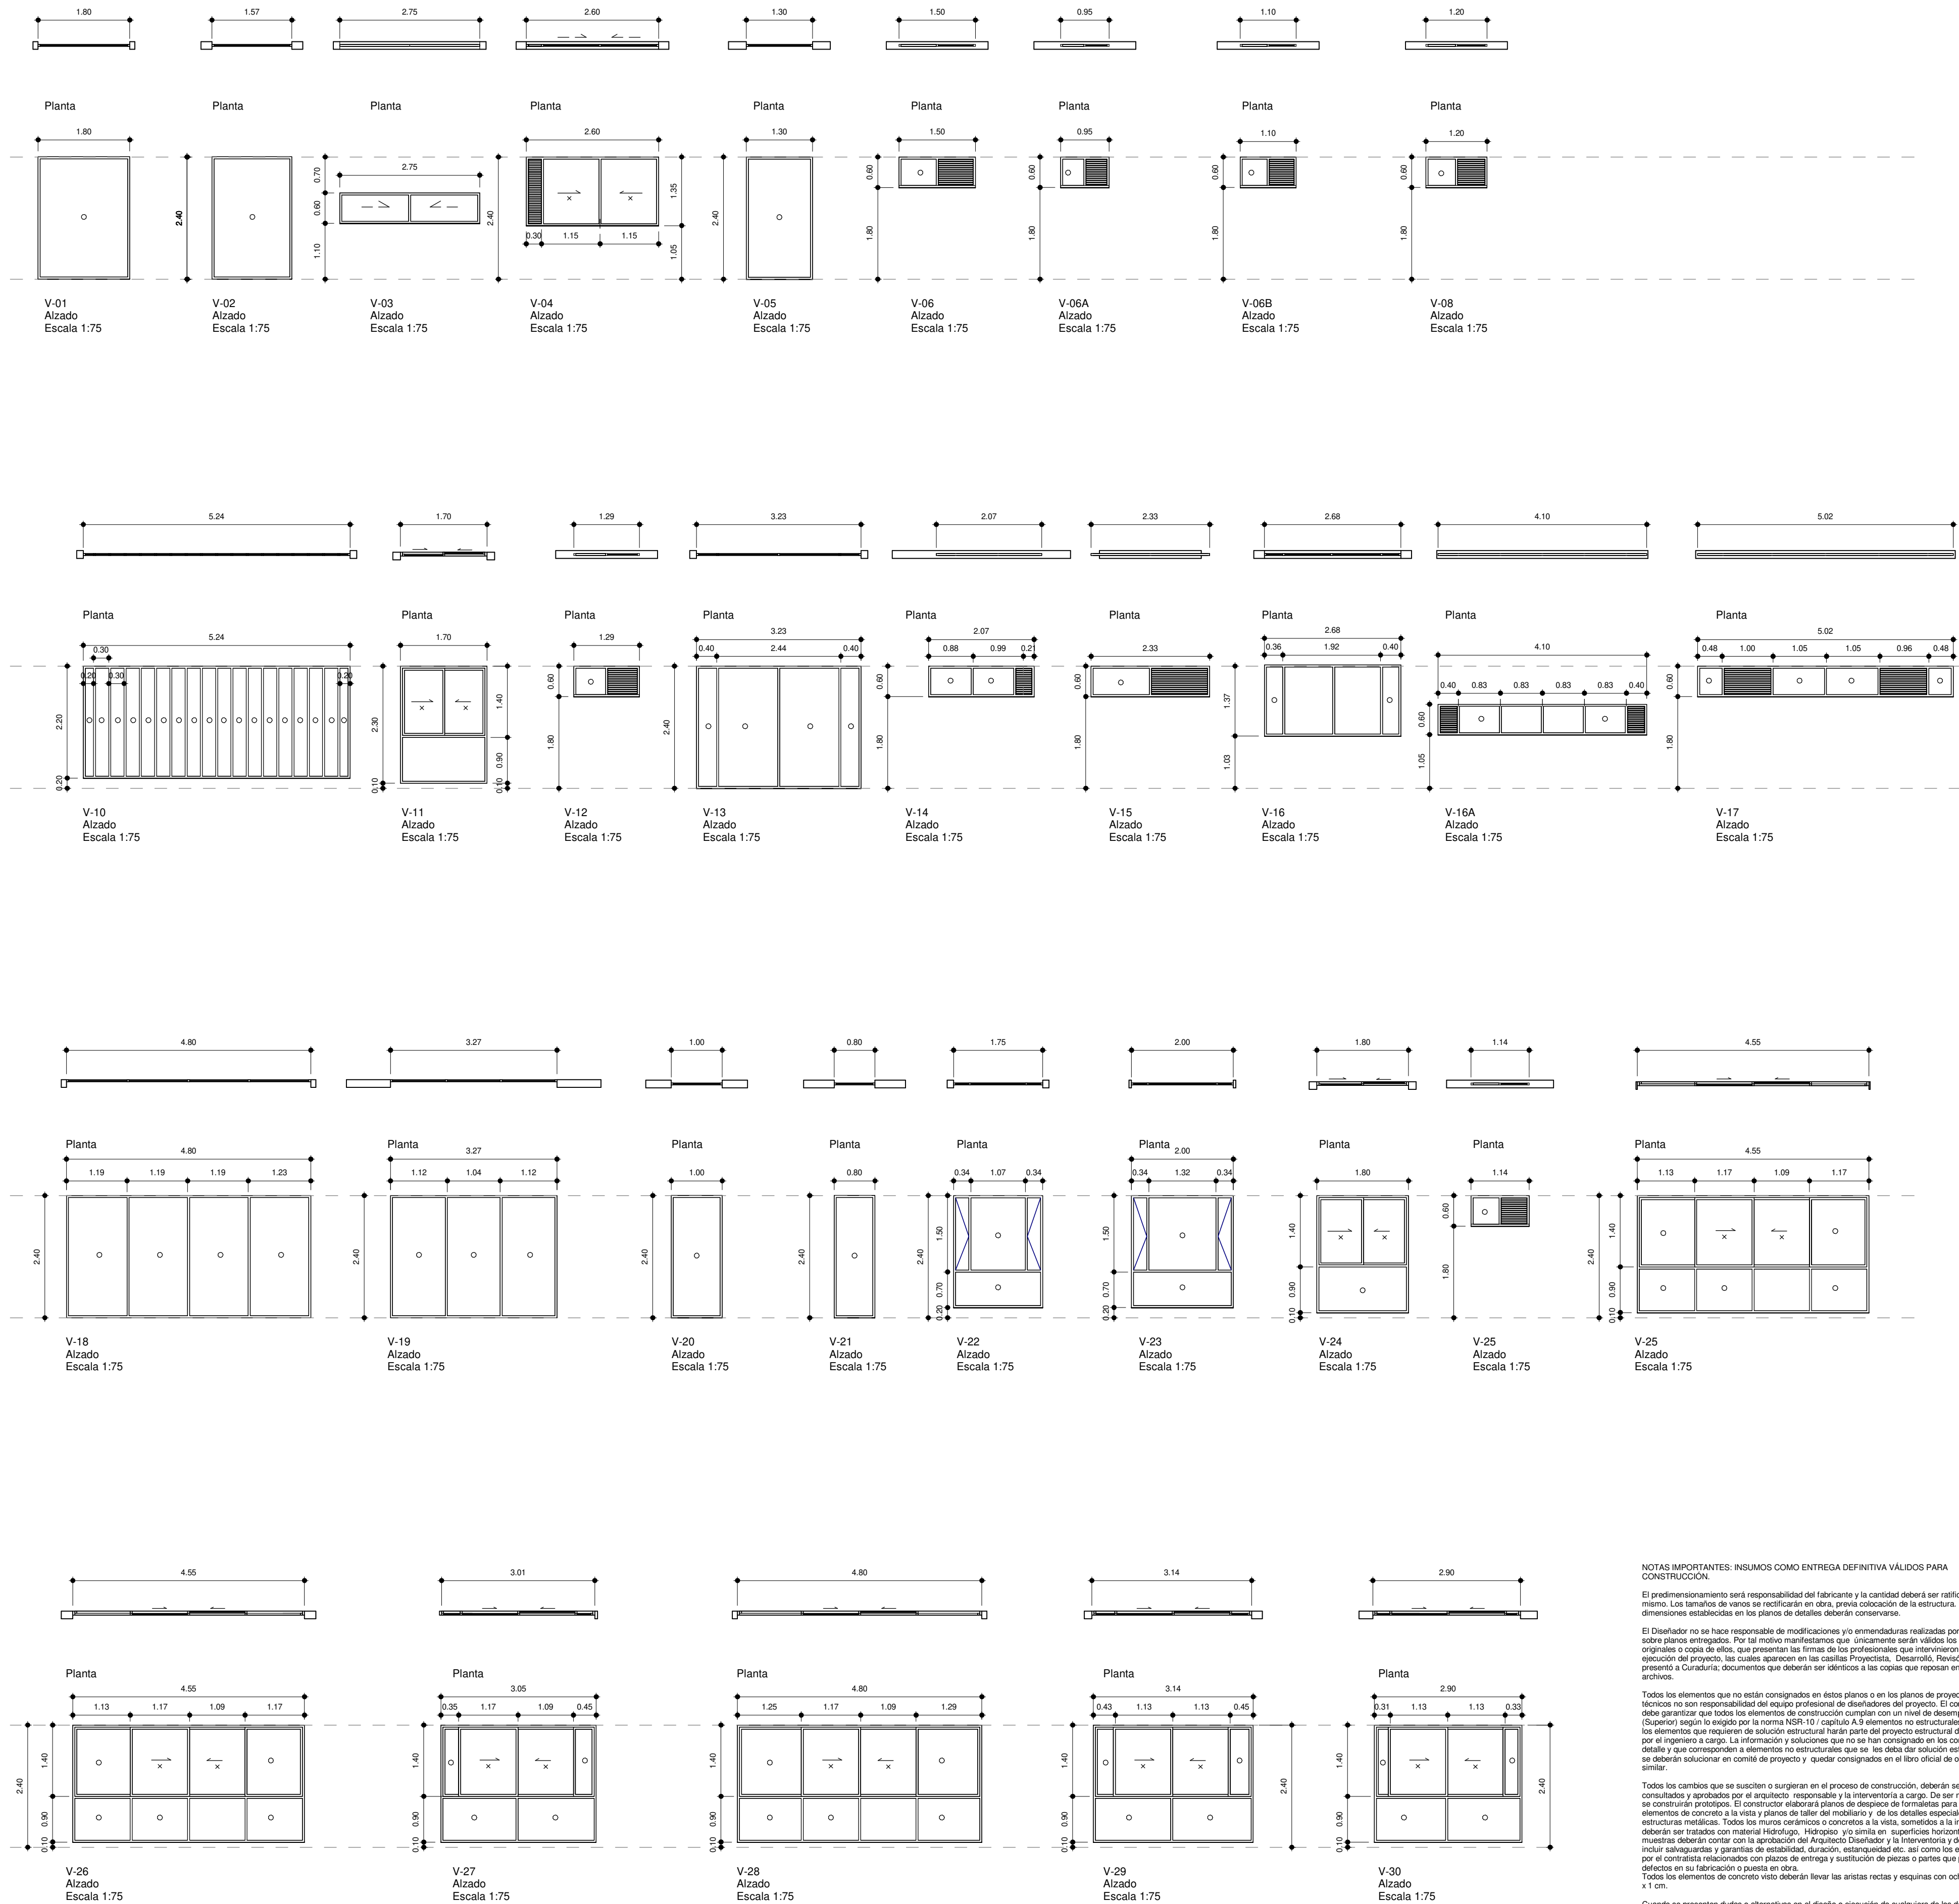
CONTIENE:

MAT. A05A02007-8359284

Cuadro Puertas-Ventanas

ESCALA: 1 : 50

Este plano y su contenido, están protegidos por la ley de derechos de autor. Si el poseedor de este plano lo disemina, distribuye, copia o usa sin autorización escrita, formal y legal de STUDIO AREA & S.A.S., estará violando las disposiciones de la Ley 23 de 1982, sobre derechos de autor.



NOTAS IMPORTANTES: INSUMOS COMO ENTREGA DEFINITIVA VÁLIDOS PARA CONSTRUCCIÓN.

El predimensionamiento será responsabilidad del fabricante y la cantidad deberá ser ratificada por el mismo. Los tamaños de varcos se notificarán en obra, previa colocación de la estructura. Las dimensiones establecidas en los planos de detalles deberán conservarse.

El Diseñador no se hace responsable de modificaciones y/o enmiendas realizadas por otros, sobre planos entregados. Por tal motivo manifestamos que únicamente serán válidos los planos originales o copia de ellos, que presenten las firmas de los profesionales que intervienen en la ejecución del proyecto, las cuales aparecen en las carpetas Proyecto, Desarrollo, Revisó y quien presentó a Curaduría, documentos que deberán ser idénticos a las copias que reposan en nuestros archivos.

Todos los elementos que no estén consignados en estos planos o en los planos de proyectos técnicos no son responsabilidad del equipo profesional de diseñadores del proyecto. El constructor debe garantizar que todos los elementos de construcción cumplan con un nivel de desempeño III (Superior) según lo exigido por la norma NSR-10, capítulo A.5 elementos no estructurales. Todos los elementos que requieren de solución estructural harán parte del proyecto estructural diseñado por el ingeniero a cargo. La información y soluciones que no se han consignado en los cortes de detalle y que corresponden a elementos no estructurales que se les deba dar solución estructural se deberán solucionar en comité de proyecto y quedar consignados en el libro oficial de obra o similar.

Todos los cambios que se susciten o surjan en el proceso de construcción, deberán ser consultados y aprobados por el arquitecto responsable y la interventoría a cargo. De ser necesario se construirán prototipos. El constructor elaborará planos de despiece de formateras para los elementos de concreto a la vista y planos de taller del mobiliario y de los detalles especiales, tipo estructuras metálicas. Todos los muros cortinados o concretos a la vista, sometidos a la intemperie deberán ser tratados con material hidrófugo. Hidrófugo y/o similar en superficies horizontales. Las muestras deberán contar con la aprobación del Arquitecto Diseñador y la Interventoría y deberán incluir salvaguardas y garantías de estabilidad, duración, estanqueidad etc, así como los orgános per el control de calidad relacionados con plazos de entrega y sustitución de piezas o partes que presenten defectos en su fabricación o puesta en obra. Todos los elementos de concreto visto deberán llevar las aristas rectas y esquinas con ochave de 1 x 1 cm.

Cuando se presenten dudas o alternativas en el diseño o ejecución de cualquiera de los detalles previstos, estos deberán ser dirigidos con la aprobación de los Arquitectos Diseñadores y constará en el acta de comité, la aprobación de la Interventoría.

Es responsabilidad de los diseñadores técnicos, de la supervisión técnica, y de los proveedores, fabricantes e instaladores de los elementos no estructurales del edificio, suministrar al arquitecto diseñador la información requerida para complementar la coordinación de los diseños, previo a la aplicación de obra (Según N.S.R.2010).

Tabla de planificación de ventanas						
Marca de tipo	Anchura	Altura	Cantidad	Nivel	Descripción	
V-01	1.80	2.40	1	Casa 1 P1	Modulo fijo en marco 1101 negro con pisaavídrio 177 y divisores en 1103 y alfaja de 12 cms, cubierta en vidrio templado de 6mm incoloro, sellos perimetrales externos en sika 1a multiproposito.	
V-02	1.57	2.40	1	Casa 1 P1	Modulo fijo en marco 1101 negro con pisaavídrio 177 y divisores en 1103 y alfaja de 12 cms, cubierta en vidrio templado de 6mm incoloro, sellos perimetrales externos en sika 1a multiproposito.	
V-02	1.57	2.40	1	Casa 1 P1	Modulo fijo en marco 1101 negro con pisaavídrio 177 y divisores en 1103 y alfaja de 12 cms, cubierta en vidrio templado de 6mm incoloro, sellos perimetrales externos en sika 1a multiproposito.	
V-03	2.75	0.60	1	Casa 1 P1	Ventana en 3831 color negro y alfaja + vidrio templado de 5mm incoloro y modulo con persiana 316 y mosquetero interno, instalada con sellos perimetrales externos en sika 1a multiproposito.	
V-04	2.60	1.35	1	Casa 1 P1	Ventana en 3831 color negro y alfaja + vidrio templado de 5mm incoloro y modulo con persiana 316 y mosquetero interno, instalada con sellos perimetrales externos en sika 1a multiproposito.	
V-05	1.30	2.40	1	Casa 1 P2	Modulo fijo en marco 1101 negro con pisaavídrio 177 y divisores en 1103 y alfaja de 12 cms, cubierta en vidrio templado de 6mm incoloro, sellos perimetrales externos en sika 1a multiproposito.	
V-06	1.50	0.60	1	Casa 1 P1	Ventana en 3831 color negro y alfaja + vidrio templado de 5mm incoloro y modulo con persiana 316 y mosquetero interno, instalada con sellos perimetrales externos en sika 1a multiproposito.	
V-06	1.50	0.60	1	Casa 1 P2	Ventana en 3831 color negro y alfaja + vidrio templado de 5mm incoloro y modulo con persiana 316 y mosquetero interno, instalada con sellos perimetrales externos en sika 1a multiproposito.	
V-06A	0.95	0.60	1	Casa 1 P1	Ventana en 3831 color negro y alfaja + vidrio templado de 5mm incoloro y modulo con persiana 316 y mosquetero interno, instalada con sellos perimetrales externos en sika 1a multiproposito.	
V-06B	1.10	0.60	1	Casa 1 P1	Ventana en 3831 color negro y alfaja + vidrio templado de 5mm incoloro y modulo con persiana 316 y mosquetero interno, instalada con sellos perimetrales externos en sika 1a multiproposito.	
V-06B	1.10	0.60	1	Casa 1 P1	Ventana en 3831 color negro y alfaja + vidrio templado de 5mm incoloro y modulo con persiana 316 y mosquetero interno, instalada con sellos perimetrales externos en sika 1a multiproposito.	
V-08	1.20	0.60	1	Casa 1 P2	Ventana en 3831 color negro y alfaja + vidrio templado de 5mm incoloro y modulo con persiana 316 y mosquetero interno, instalada con sellos perimetrales externos en sika 1a multiproposito.	
V-08	1.20	0.60	1	Casa 2 Sotano	Ventana en 3831 color negro y alfaja + vidrio templado de 5mm incoloro y modulo con persiana 316 y mosquetero interno, instalada con sellos perimetrales externos en sika 1a multiproposito.	
V-08	1.20	0.60	1	Casa 1 P2	Ventana en 3831 color negro y alfaja + vidrio templado de 5mm incoloro y modulo con persiana 316 y mosquetero interno, instalada con sellos perimetrales externos en sika 1a multiproposito.	
V-10	5.24	2.40	1	Casa 1 P2	Modulo fijo en marco 1101 negro con pisaavídrio 177 y divisores en 1103 y alfaja de 12 cms, cubierta en vidrio templado de 6mm incoloro, sellos perimetrales externos en sika 1a multiproposito.	
V-11	2.60	2.30	1	Casa 2 P1	Vidriera en aluminio arquitectónico color negro Mate, de alumina de sistema 7038, con empaque de Neopreno, balineras de nylon, chapa duming negra, felpas y guías plásticas, vidrio claro templado de 6mm.	
V-12	1.50	0.60	1	Casa 2 P1	Ventana en 3831 color negro y alfaja + vidrio templado de 5mm incoloro y modulo con persiana 316 y mosquetero interno, instalada con sellos perimetrales externos en sika 1a multiproposito.	
V-13	1.57	2.40	1	Casa 2 P1	Modulo fijo en marco 1101 negro con pisaavídrio 177 y divisores en 1103 y alfaja de 12 cms, cubierta en vidrio templado de 6mm incoloro, sellos perimetrales externos en sika 1a multiproposito.	
V-13	1.57	2.40	1	Casa 2 P2	Modulo fijo en marco 1101 negro con pisaavídrio 177 y divisores en 1103 y alfaja de 12 cms, cubierta en vidrio templado de 6mm incoloro, sellos perimetrales externos en sika 1a multiproposito.	
V-13	1.57	2.40	1	Casa 2 Sotano	Modulo fijo en marco 1101 negro con pisaavídrio 177 y divisores en 1103 y alfaja de 12 cms, cubierta en vidrio templado de 6mm incoloro, sellos perimetrales externos en sika 1a multiproposito.	
V-14	2.07	0.60	1	Casa 2 P1	Ventana en 3831 color negro y alfaja + vidrio templado de 5mm incoloro y modulo con persiana 316 y mosquetero interno, instalada con sellos perimetrales externos en sika 1a multiproposito.	
V-15	2.33	0.60	1	Casa 2 P1	Ventana en 3831 color negro y alfaja + vidrio templado de 5mm incoloro y modulo con persiana 316 y mosquetero interno, instalada con sellos perimetrales externos en sika 1a multiproposito.	
V-16	1.90	0.60	1	Casa 2 P1	Ventana en 3831 color negro y alfaja + vidrio templado de 5mm incoloro y modulo con persiana 316 y mosquetero interno, instalada con sellos perimetrales externos en sika 1a multiproposito.	
V-16A	4.10	0.60	1	Casa 2 P1	Ventana en 3831 color negro y alfaja + vidrio templado de 5mm incoloro y modulo con persiana 316 y mosquetero interno, instalada con sellos perimetrales externos en sika 1a multiproposito.	
V-17	5.02	0.60	1	Casa 2 P2	Ventana en 3831 color negro y alfaja + vidrio templado de 5mm incoloro y modulo con persiana 316 y mosquetero interno, instalada con sellos perimetrales externos en sika 1a multiproposito.	
V-18	4.80	2.40	1	Casa 2 P2	Modulo fijo en marco 1101 negro con pisaavídrio 177 y divisores en 1103 y alfaja de 12 cms, cubierta en vidrio templado de 6mm incoloro, sellos perimetrales externos en sika 1a multiproposito.	
V-19	3.27	2.40	1	Casa 2 P2	Modulo fijo en marco 1101 negro con pisaavídrio 177 y divisores en 1103 y alfaja de 12 cms, cubierta en vidrio templado de 6mm incoloro, sellos perimetrales externos en sika 1a multiproposito.	
V-20	1.57	2.40	1	Casa 2 P2	Modulo fijo en marco 1101 negro con pisaavídrio 177 y divisores en 1103 y alfaja de 12 cms, cubierta en vidrio templado de 6mm incoloro, sellos perimetrales externos en sika 1a multiproposito.	
V-21	1.57	2.40	1	Casa 2 P2	Modulo fijo en marco 1101 negro con pisaavídrio 177 y divisores en 1103 y alfaja de 12 cms, cubierta en vidrio templado de 6mm incoloro, sellos perimetrales externos en sika 1a multiproposito.	
V-21	1.57	2.40	1	Casa 2 P2	Modulo fijo en marco 1101 negro con pisaavídrio 177 y divisores en 1103 y alfaja de 12 cms, cubierta en vidrio templado de 6mm incoloro, sellos perimetrales externos en sika 1a multiproposito.	
V-22	1.57	2.40	1	Casa 2 P2	Vidriera en aluminio arquitectónico color negro Mate, de alumina de sistema 7038, con empaque de Neopreno, balineras de nylon, chapa duming negra, felpas y guías plásticas, vidrio claro templado de 6mm. + Cuerpos Projectantes	
V-23	1.57	2.40	1	Casa 2 P2	Vidriera en aluminio arquitectónico color negro Mate, de alumina de sistema 7038, con empaque de Neopreno, balineras de nylon, chapa duming negra, felpas y guías plásticas, vidrio claro templado de 6mm. + Cuerpos Projectantes	
V-24	2.60	2.30	1	Casa 2 Sotano	Vidriera en aluminio arquitectónico color negro Mate, de alumina de sistema 7038, con empaque de Neopreno, balineras de nylon, chapa duming negra, felpas y guías plásticas, vidrio claro templado de 6mm.	
V-25	1.14	0.60	1	Casa 2 Sotano	Ventana en 3831 color negro y alfaja + vidrio templado de 5mm incoloro y modulo con persiana 316 y mosquetero interno, instalada con sellos perimetrales externos en sika 1a multiproposito.	
V-26	2.60	2.30	1	Casa 2 Sotano	Vidriera en aluminio arquitectónico color negro Mate, de alumina de sistema 7038, con empaque de Neopreno, balineras de nylon, chapa duming negra, felpas y guías plásticas, vidrio claro templado de 6mm.	
V-27	2.60	2.30	1	Casa 2 Sotano	Vidriera en aluminio arquitectónico color negro Mate, de alumina de sistema 7038, con empaque de Neopreno, balineras de nylon, chapa duming negra, felpas y guías plásticas, vidrio claro templado de 6mm.	
V-28	2.60	2.30	1	Casa 2 Sotano	Vidriera en aluminio arquitectónico color negro Mate, de alumina de sistema 7038, con empaque de Neopreno, balineras de nylon, chapa duming negra, felpas y guías plásticas, vidrio claro templado de 6mm.	
V-29	2.60	2.30	1	Casa 2 Sotano	Vidriera en aluminio arquitectónico color negro Mate, de alumina de sistema 7038, con empaque de Neopreno, balineras de nylon, chapa duming negra, felpas y guías plásticas, vidrio claro templado de 6mm.	
V-30	2.60	2.30	1	Casa 2 Sotano	Vidriera en aluminio arquitectónico color negro Mate, de alumina de sistema 7038, con empaque de Neopreno, balineras de nylon, chapa duming negra, felpas y guías plásticas, vidrio claro templado de 6mm.	
Total general			39			

Casa Campestre

Lote No. 1 El Espigal-Envigado-Ant
Mat. 001-1416040

ARQUITECTO:

ALEJANDRO GONZÁLEZ JARAMILLO
MAT. A05A02007-8359284

CONTIENE:

Cuadro Ventanas

Plancha

No.

A111

ESCALA:

1 : 75

Este plano y su contenido, están protegidos por la ley de derechos de autor. Si el poseedor de este plano lo diseña, distribuye, copia o usa sin autorización escrita, formal y legal de STUDIO AREA + S.A.S., estará violando las disposiciones de la Ley 23 de 1982, sobre derechos de autor.