




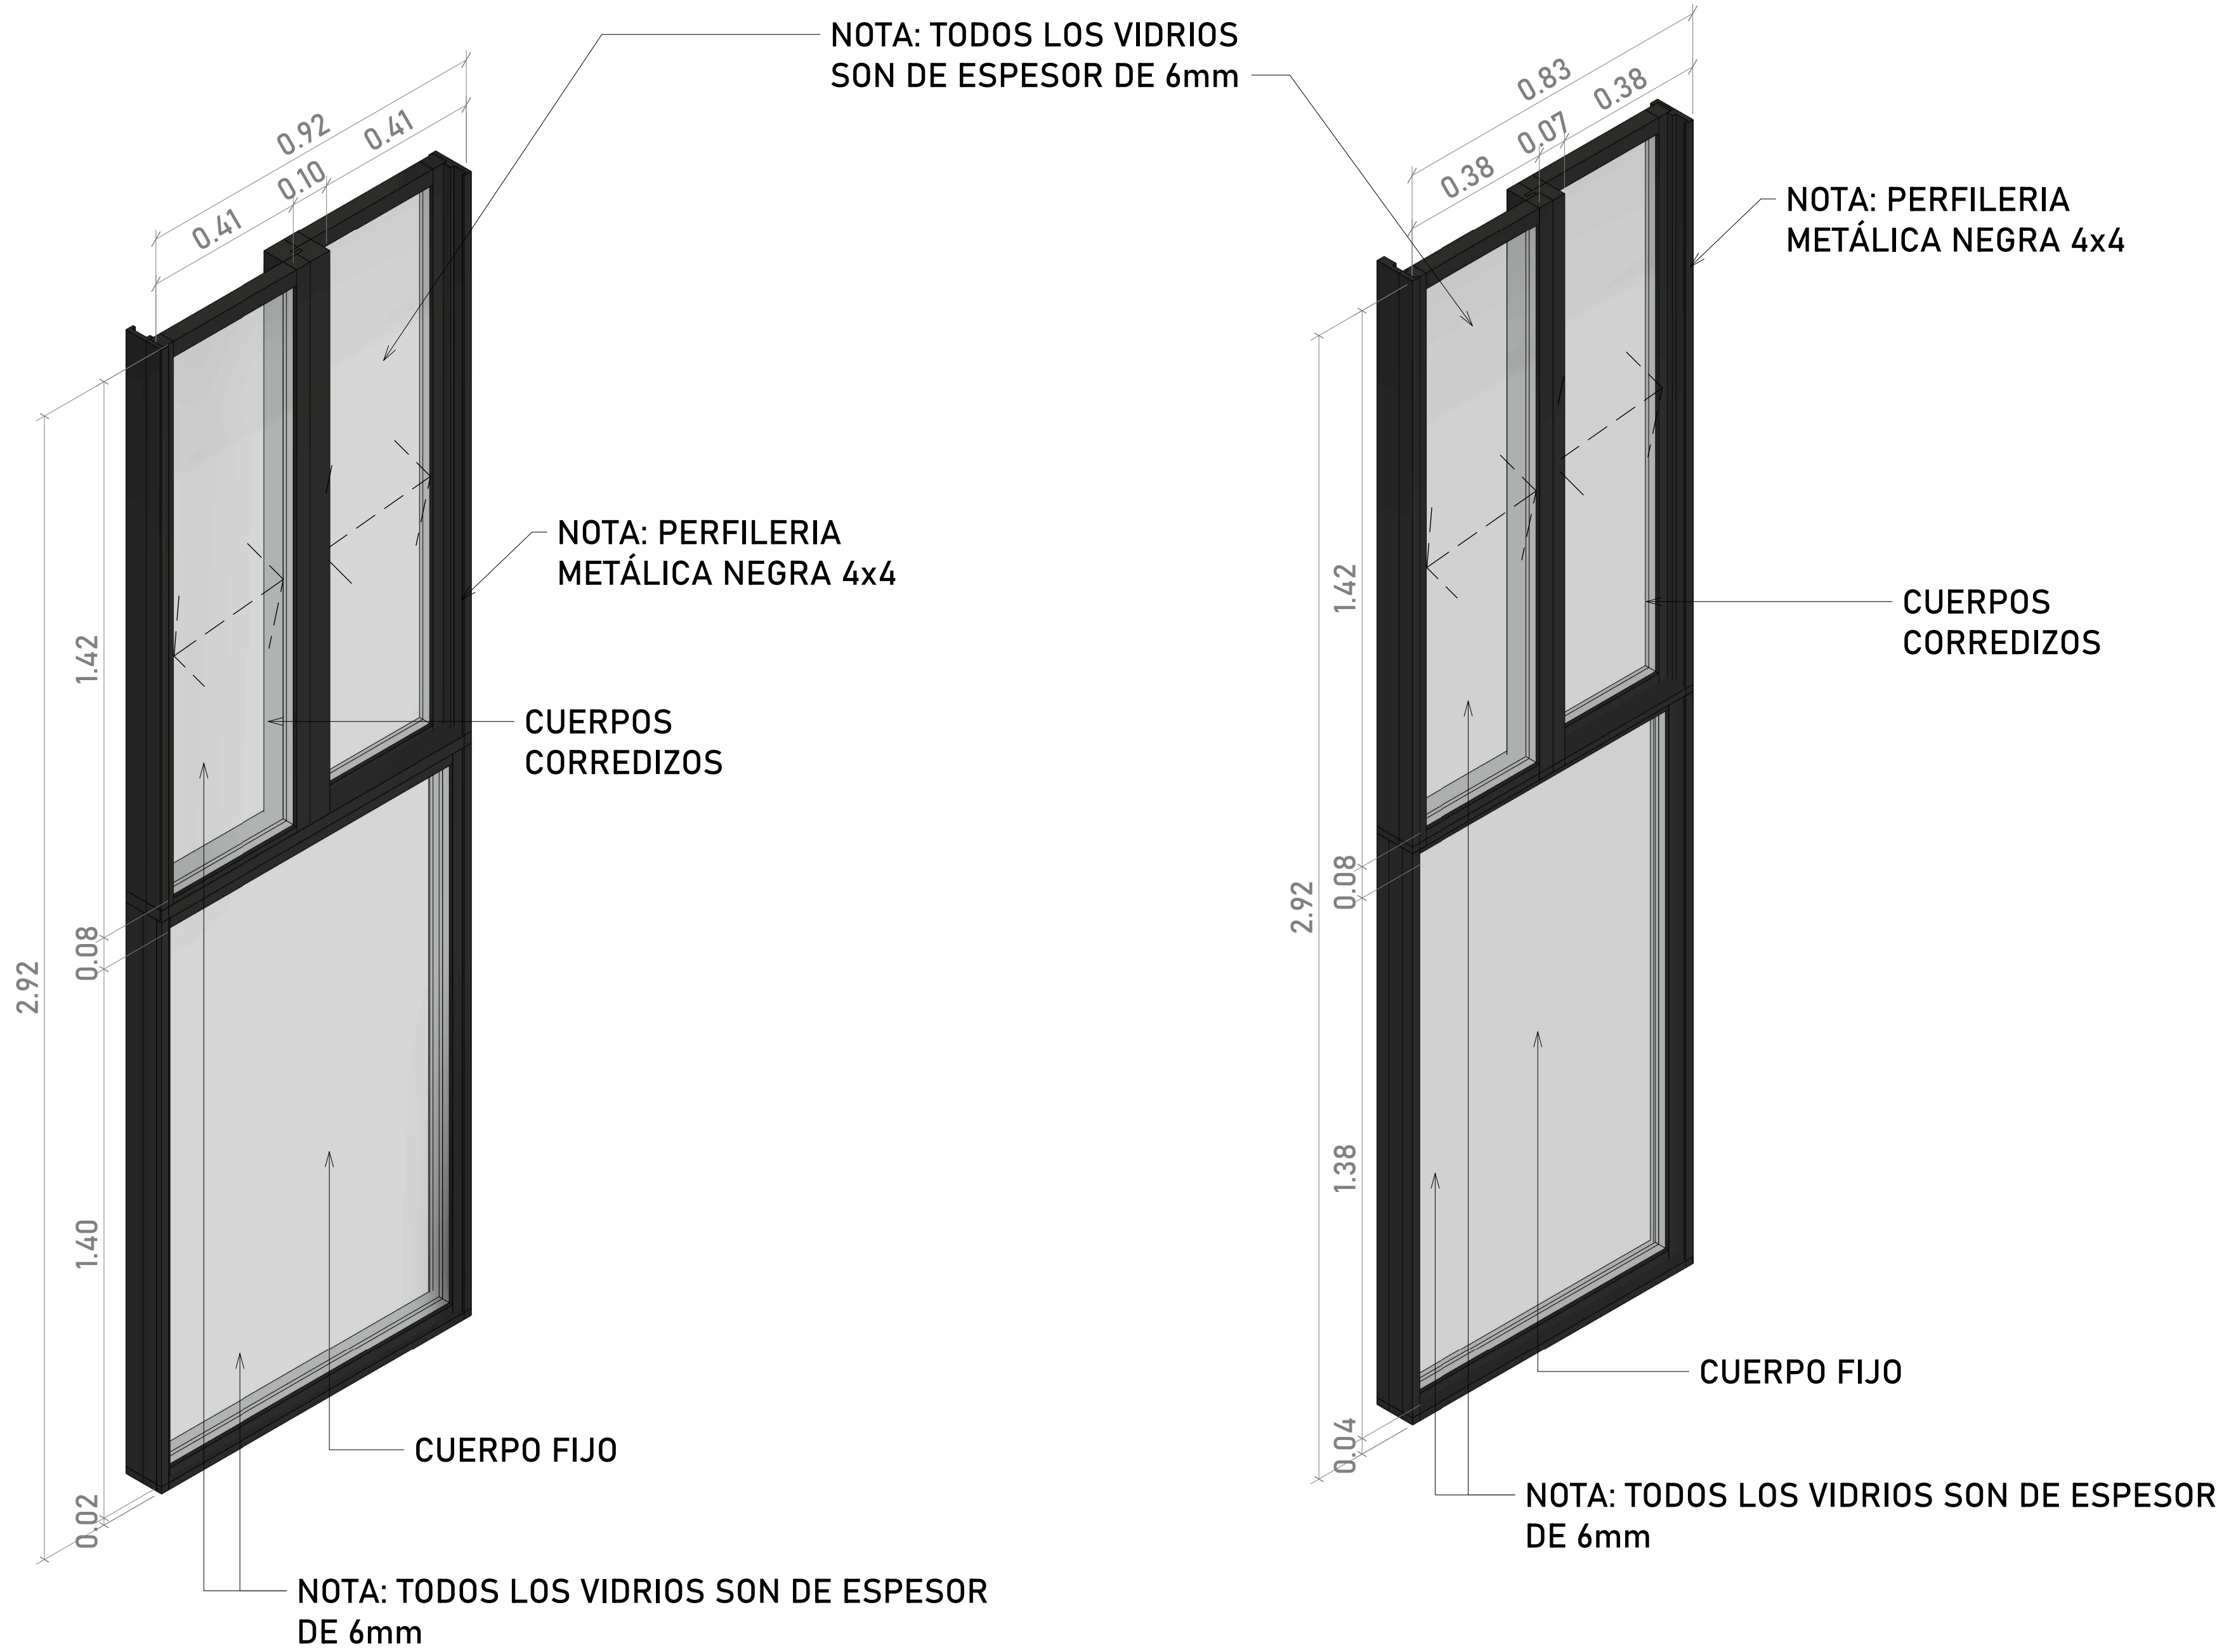


1 VENTANA 1 HAB SERVICIO
1: 10

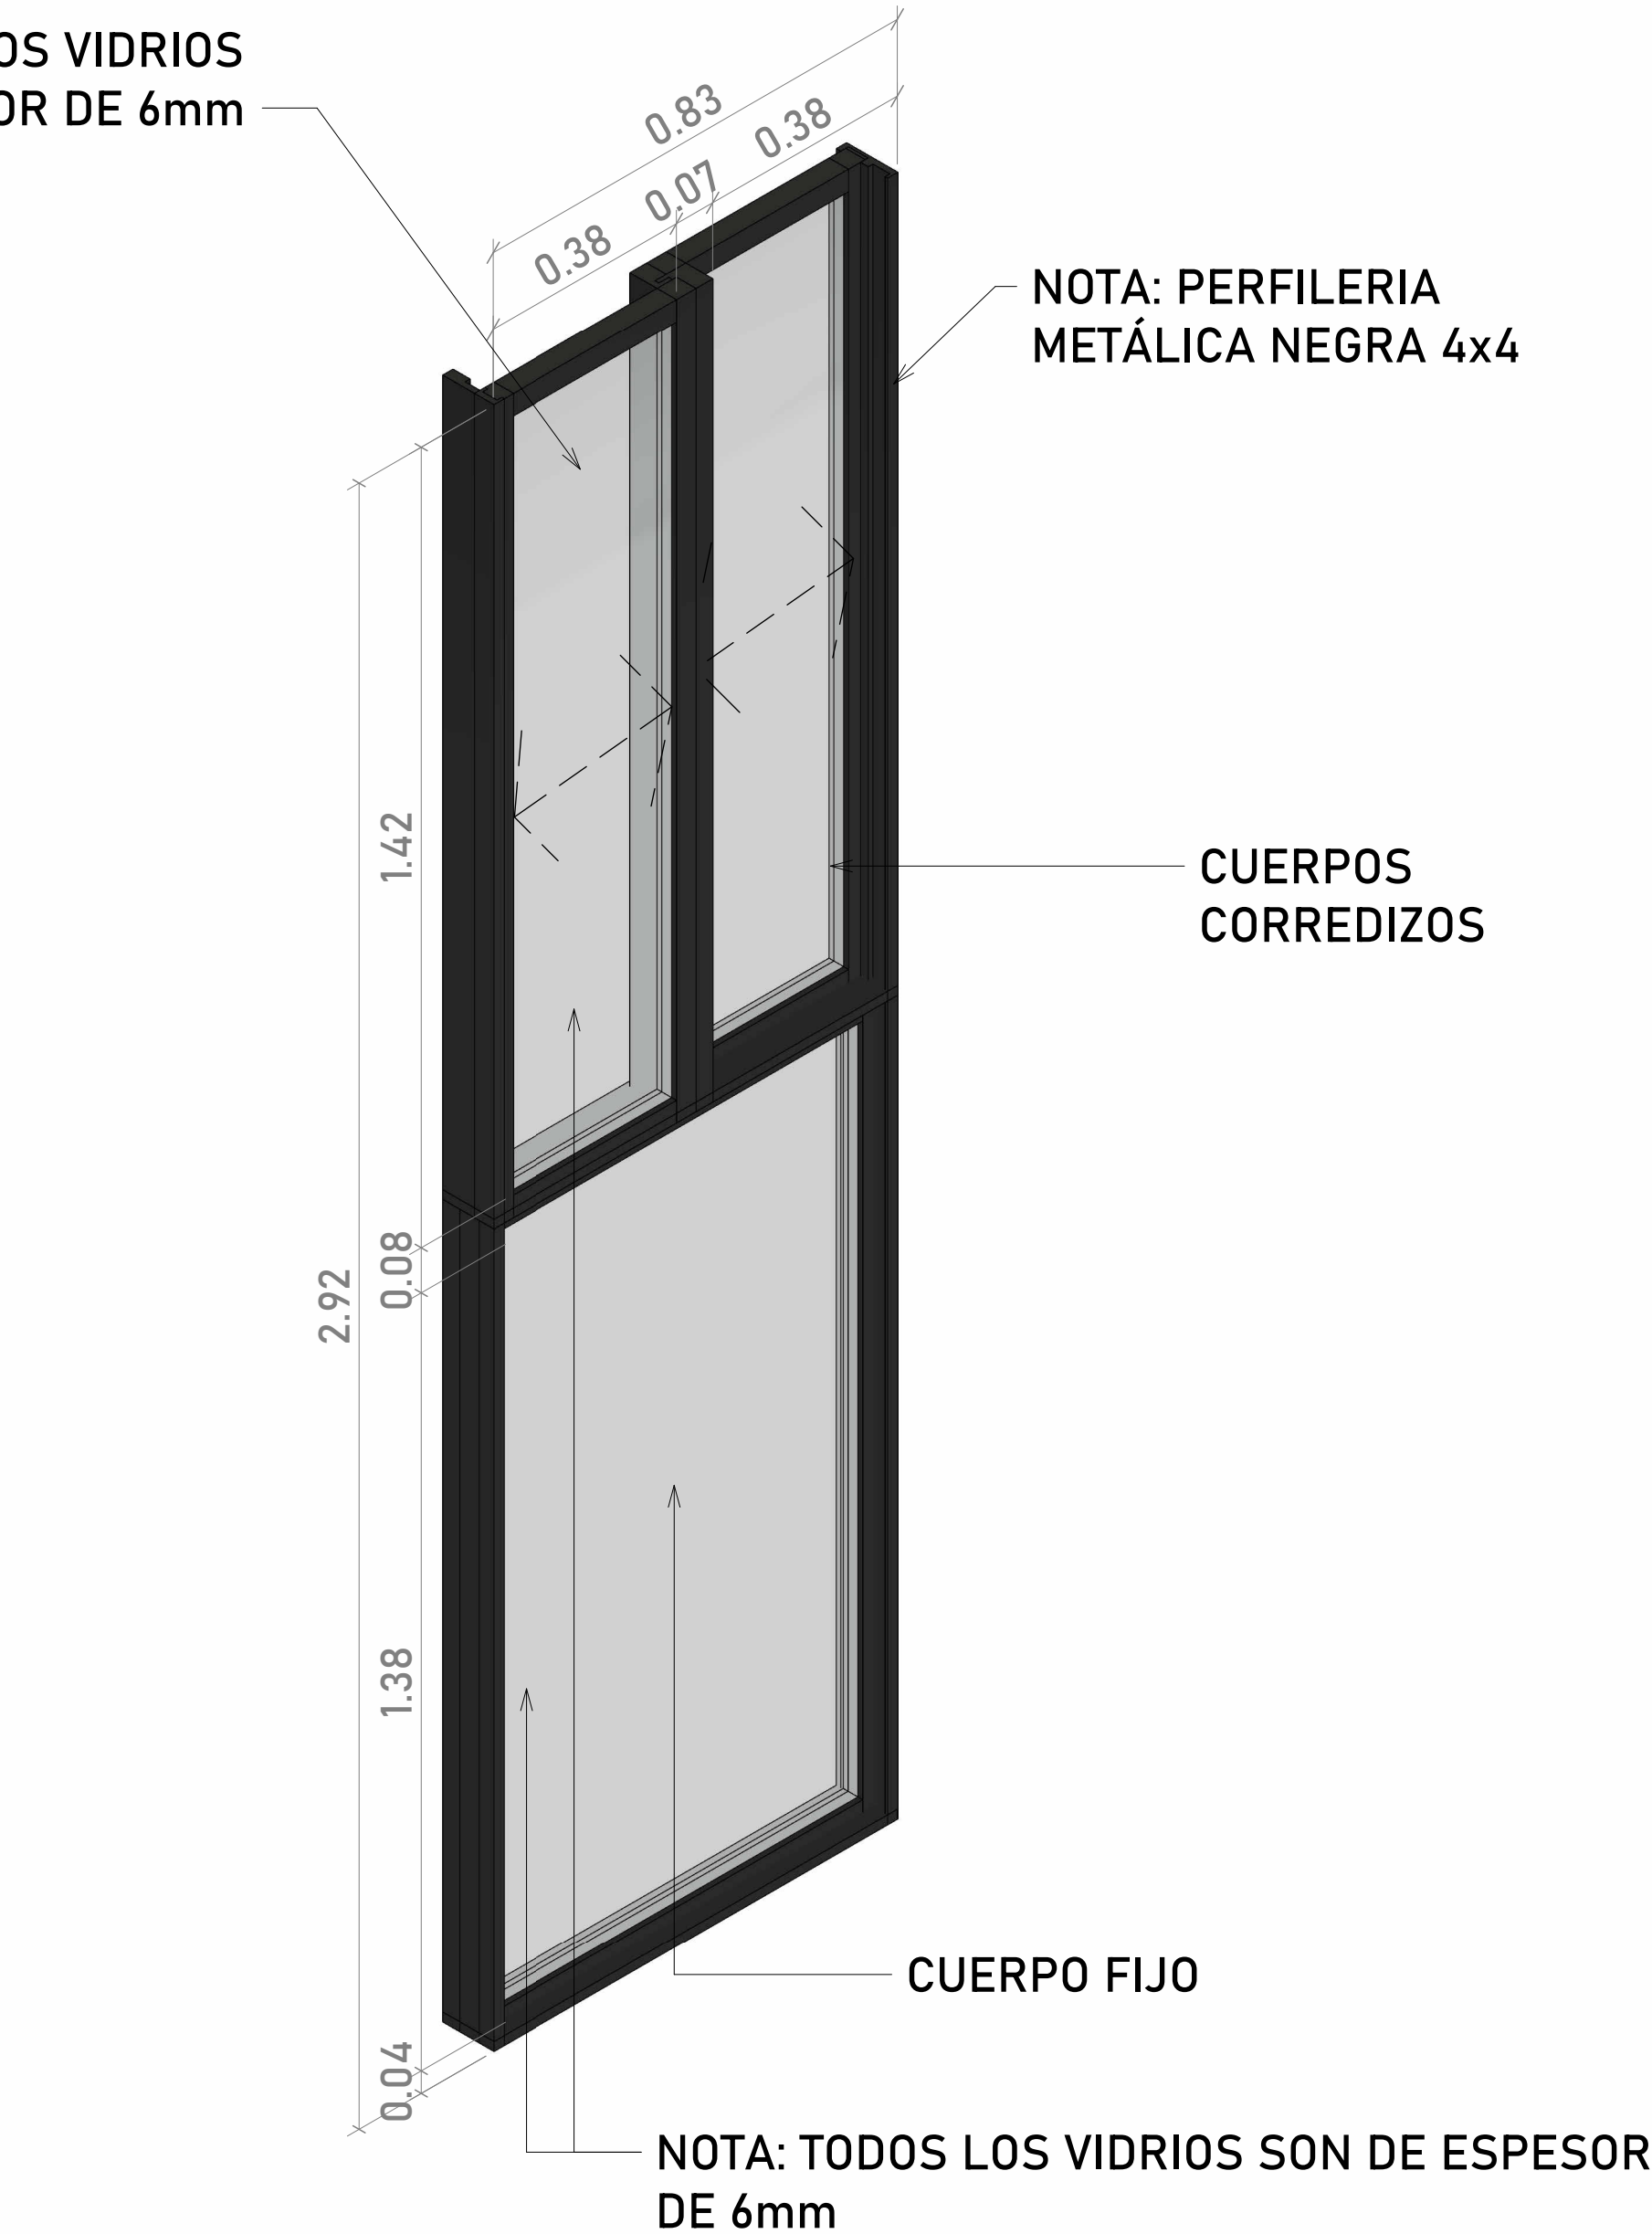


2 VENTANA 2 HAB SERVICIO
1: 10

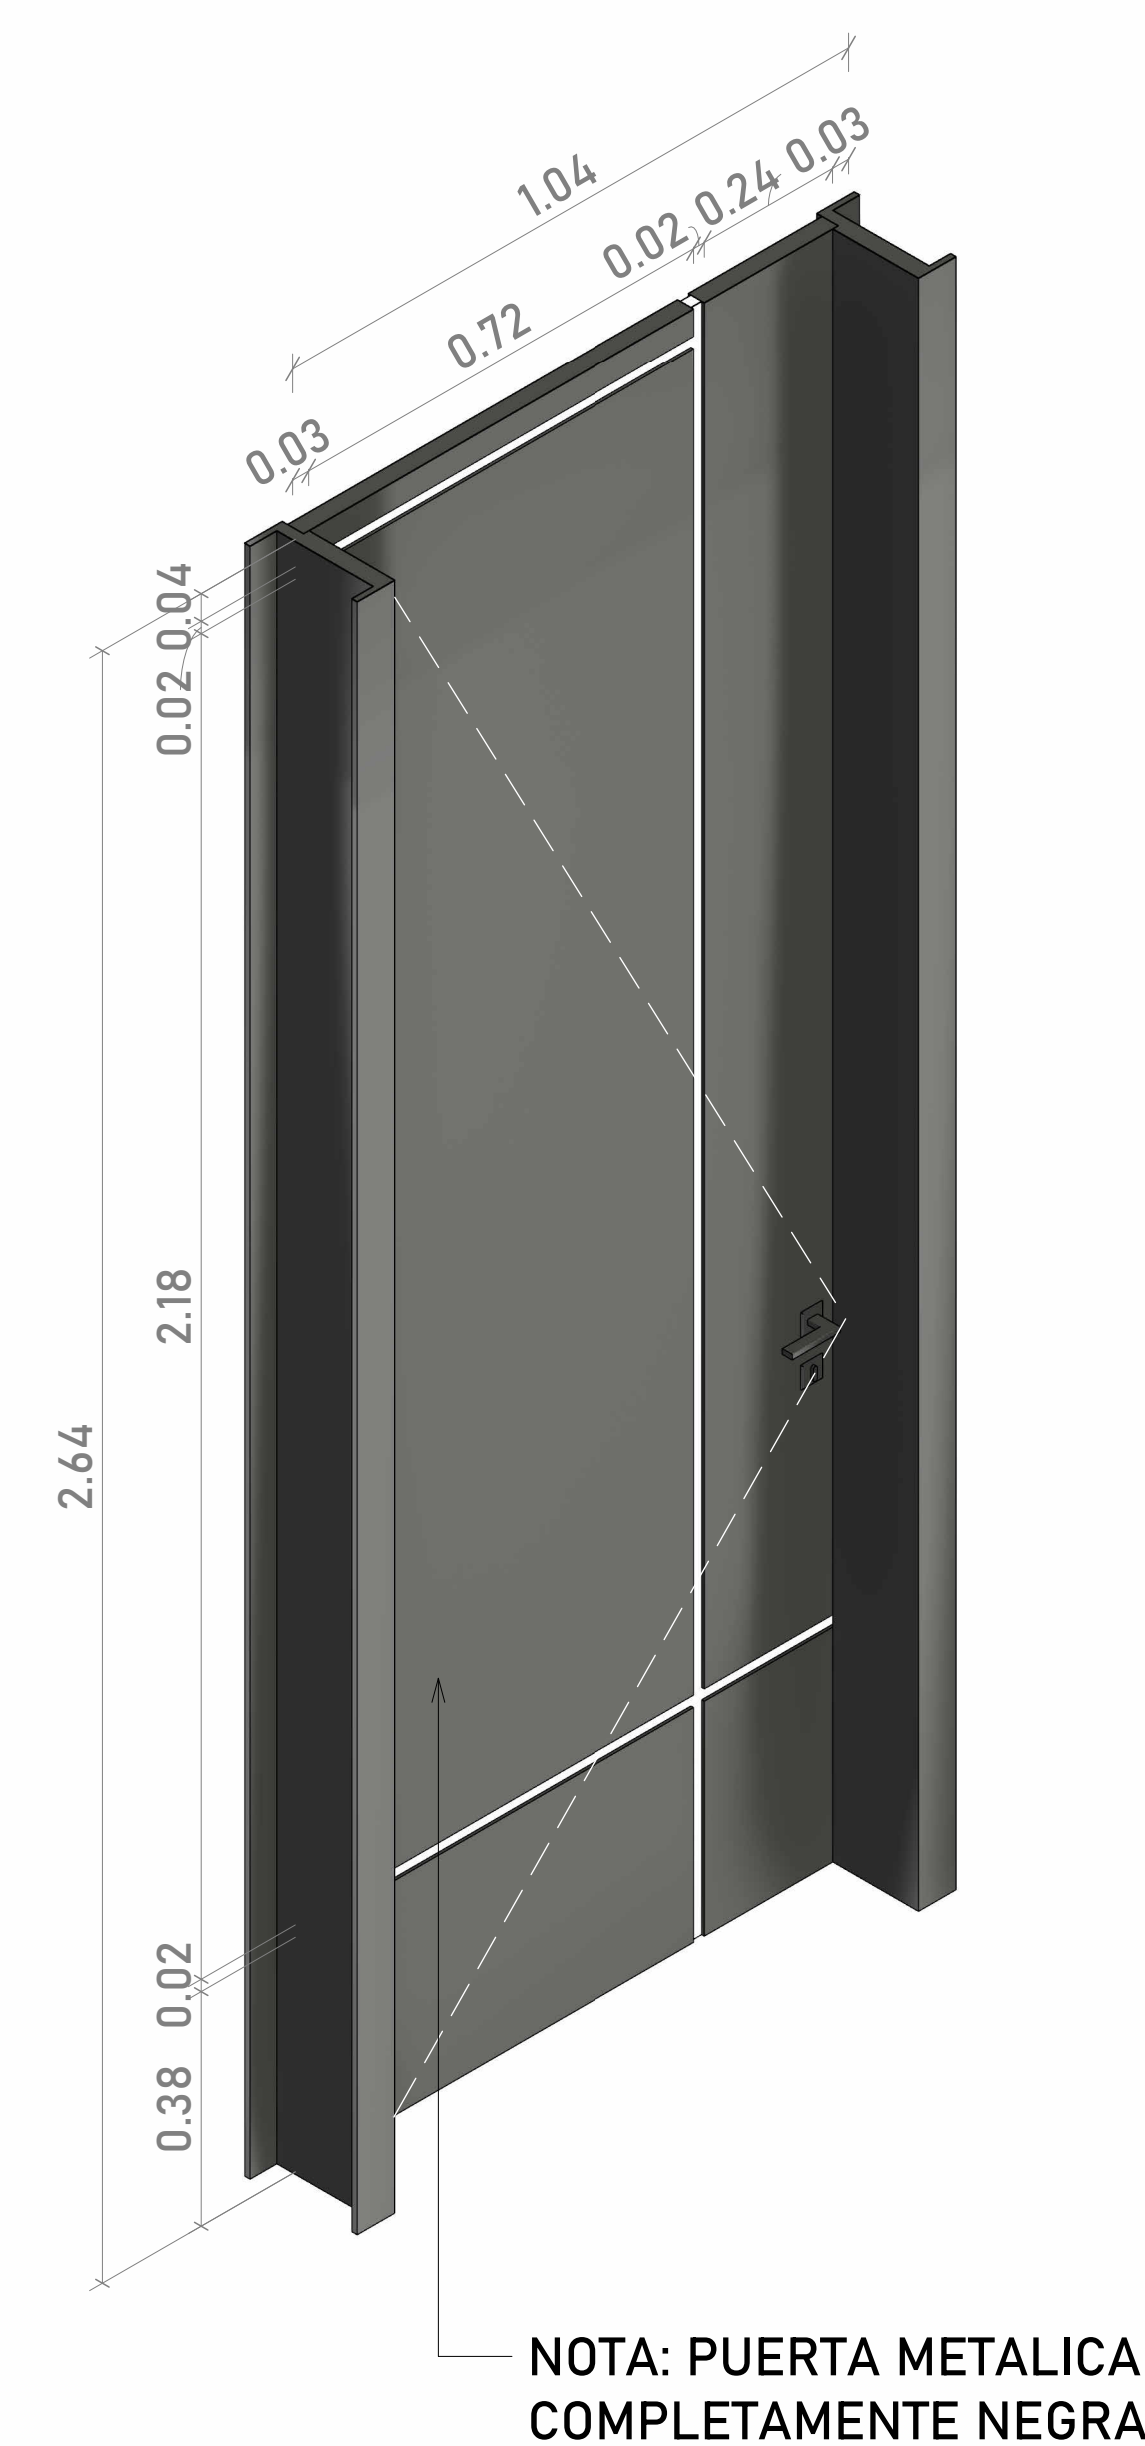


3 PUERTA METÁLICA HAB SERVICIO
1: 10

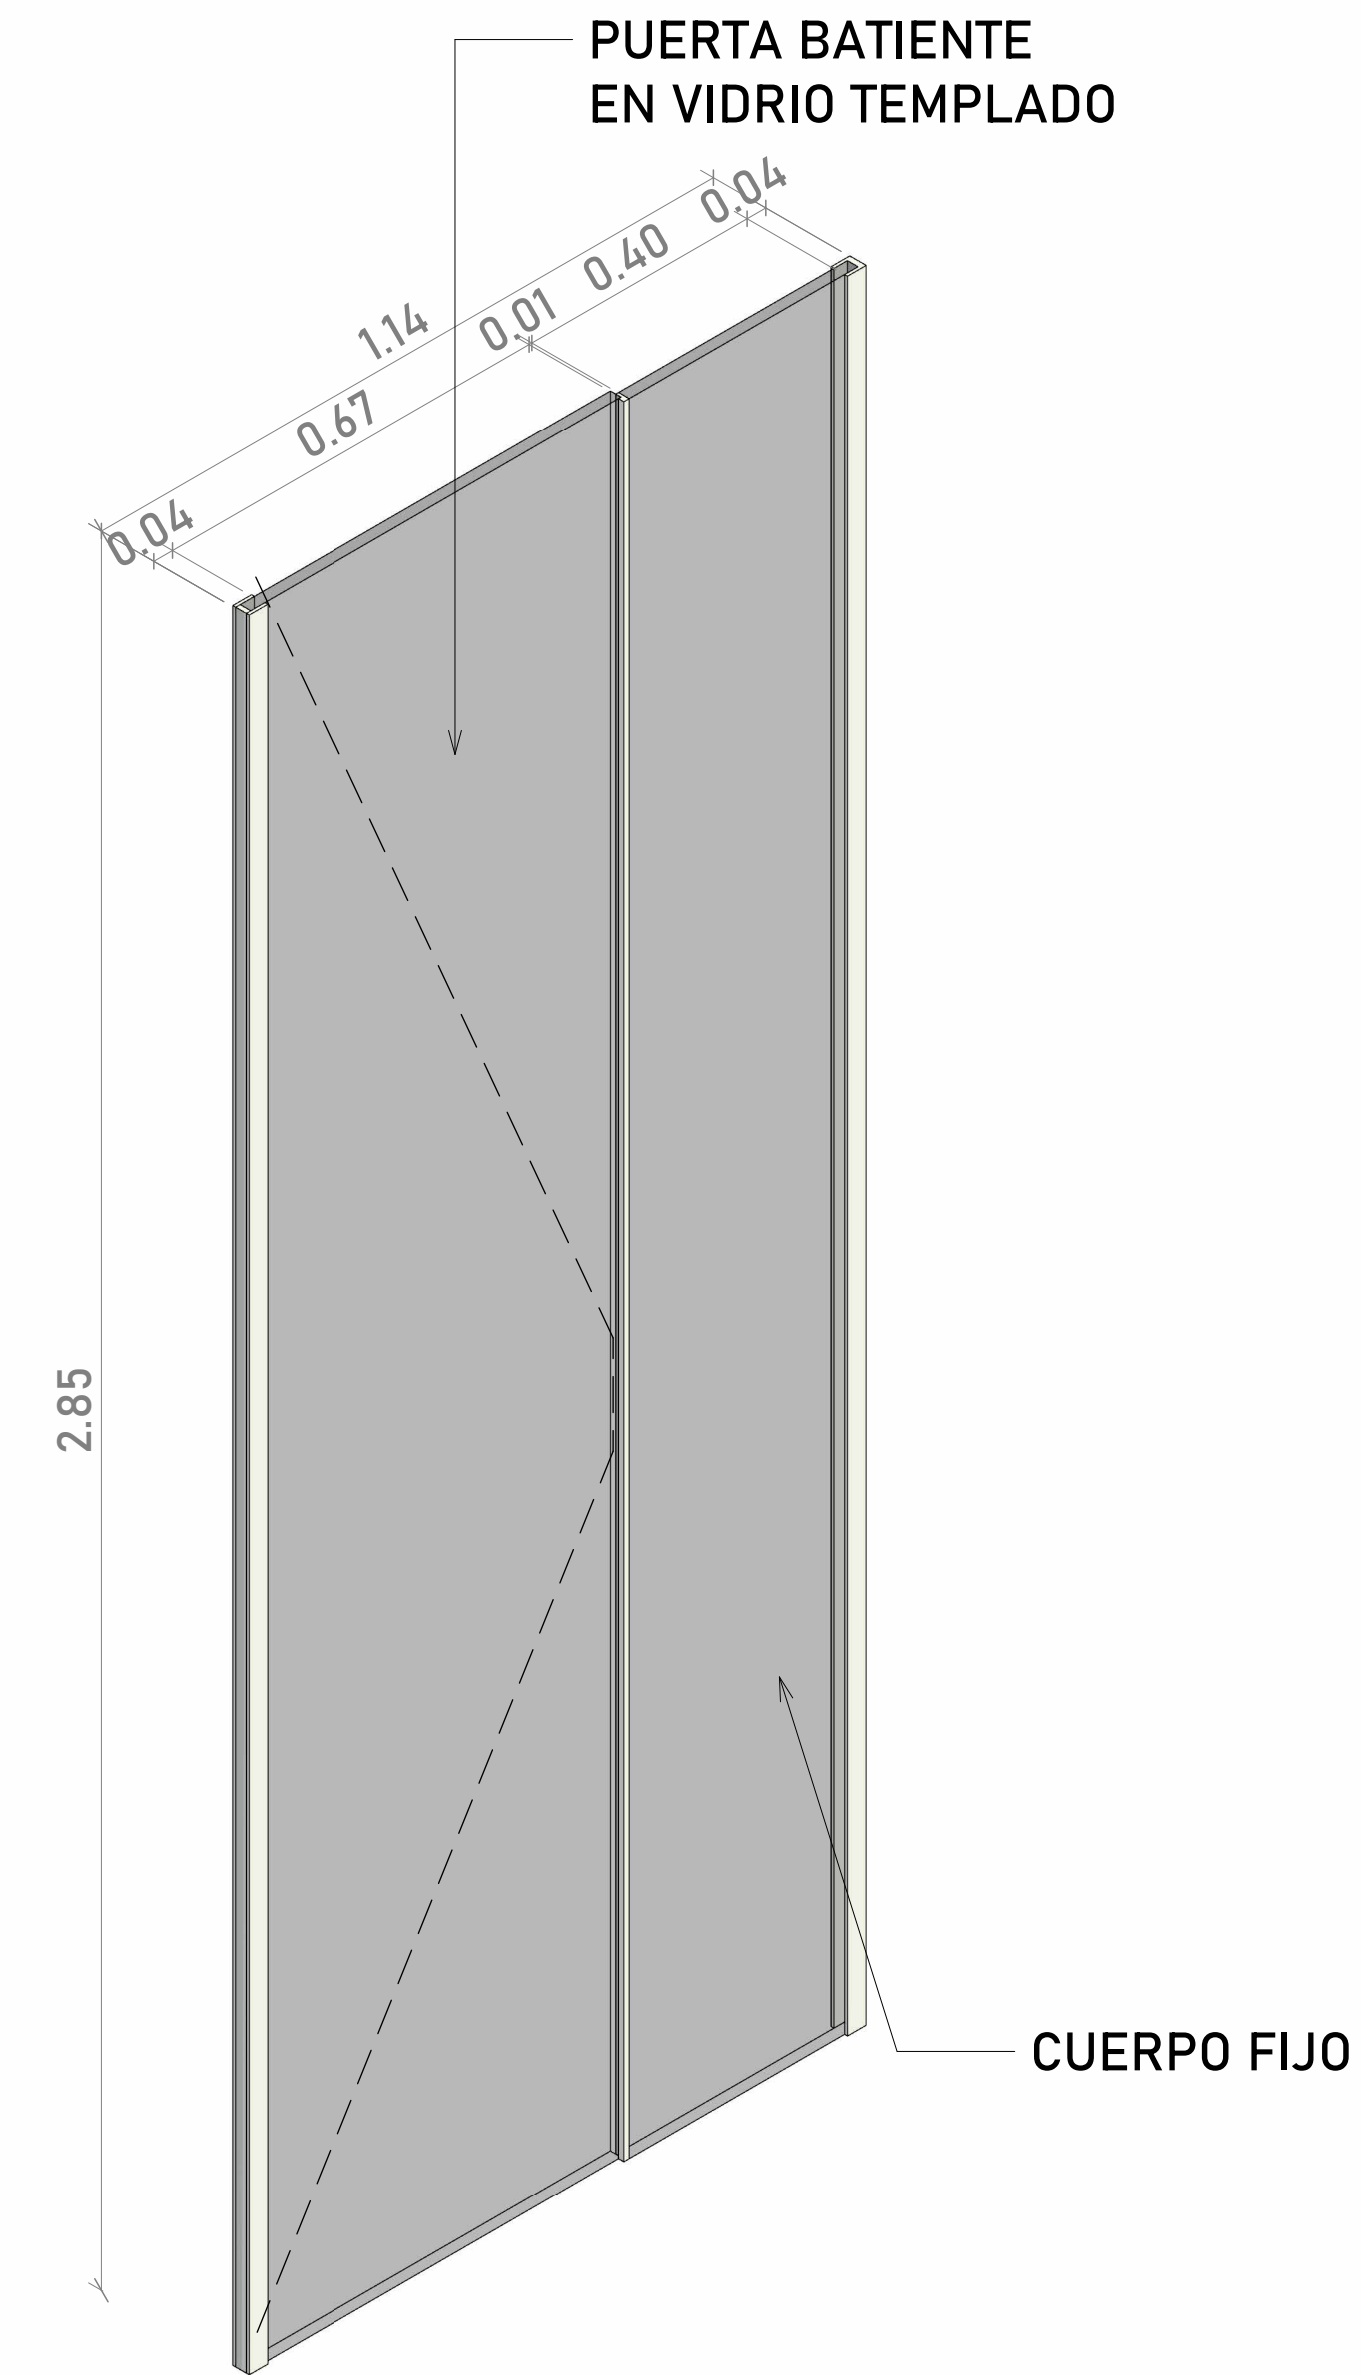


4 CABINA DUCHA HAB SERVICIO
1: 10

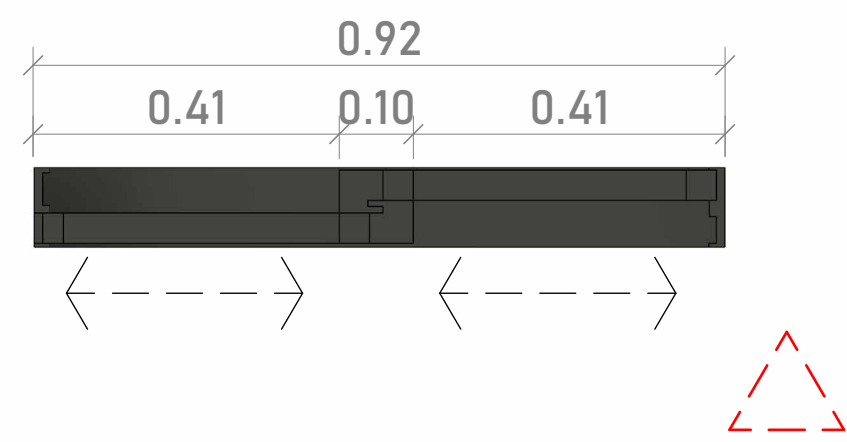


1 VENTANA 1 HAB SERVICIO
1: 10

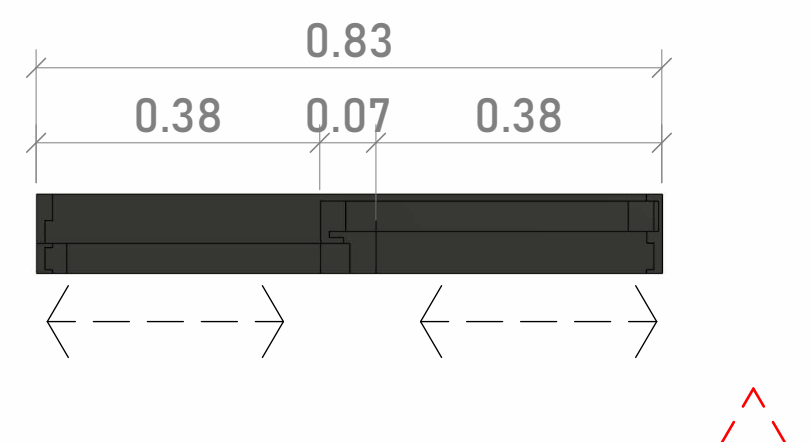


2 VENTANA 2 HAB SERVICIO
1: 10

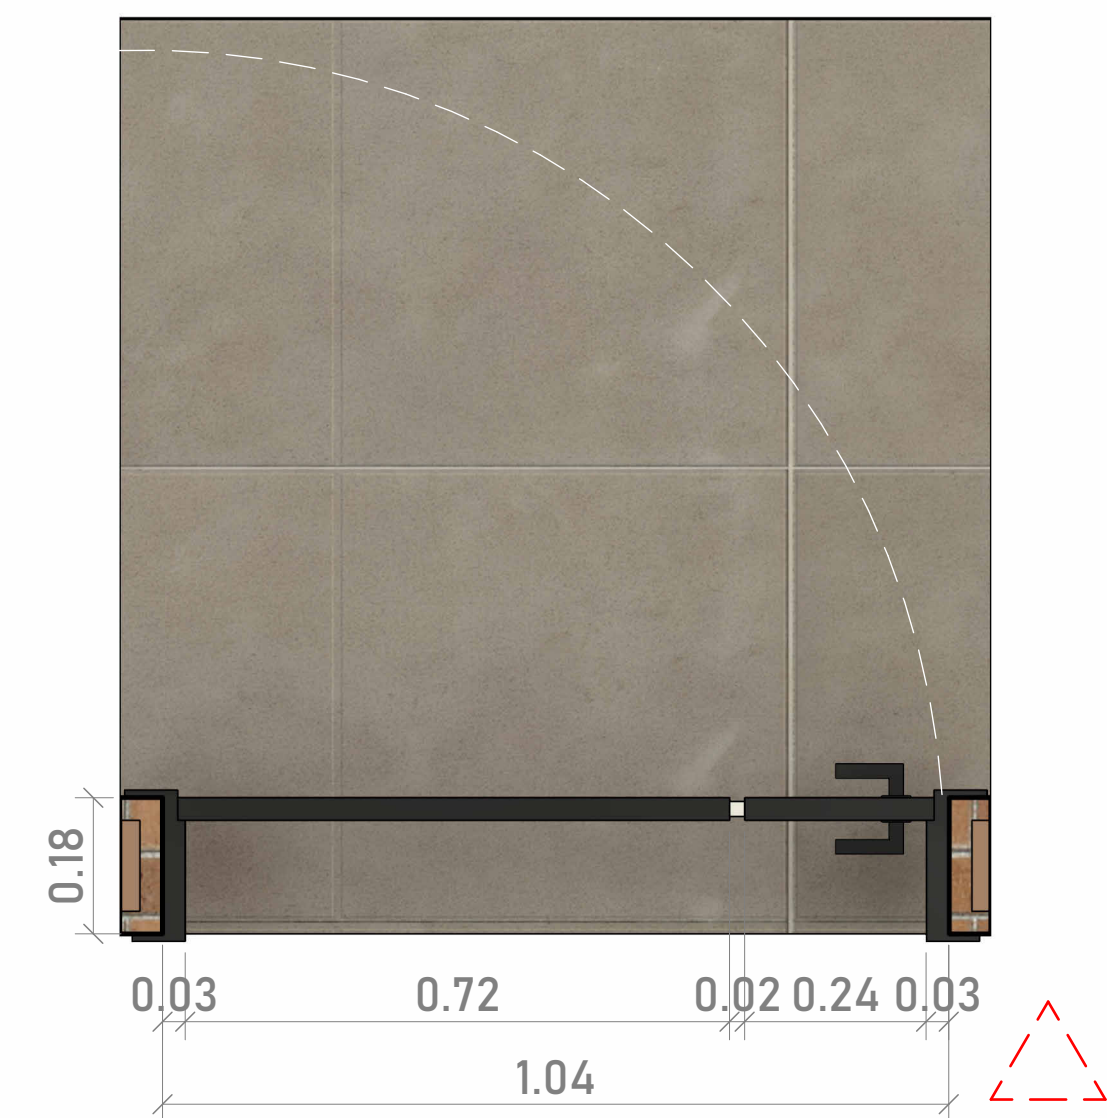

3 PUERTA METÁLICA HAB SERVICIO
1: 10

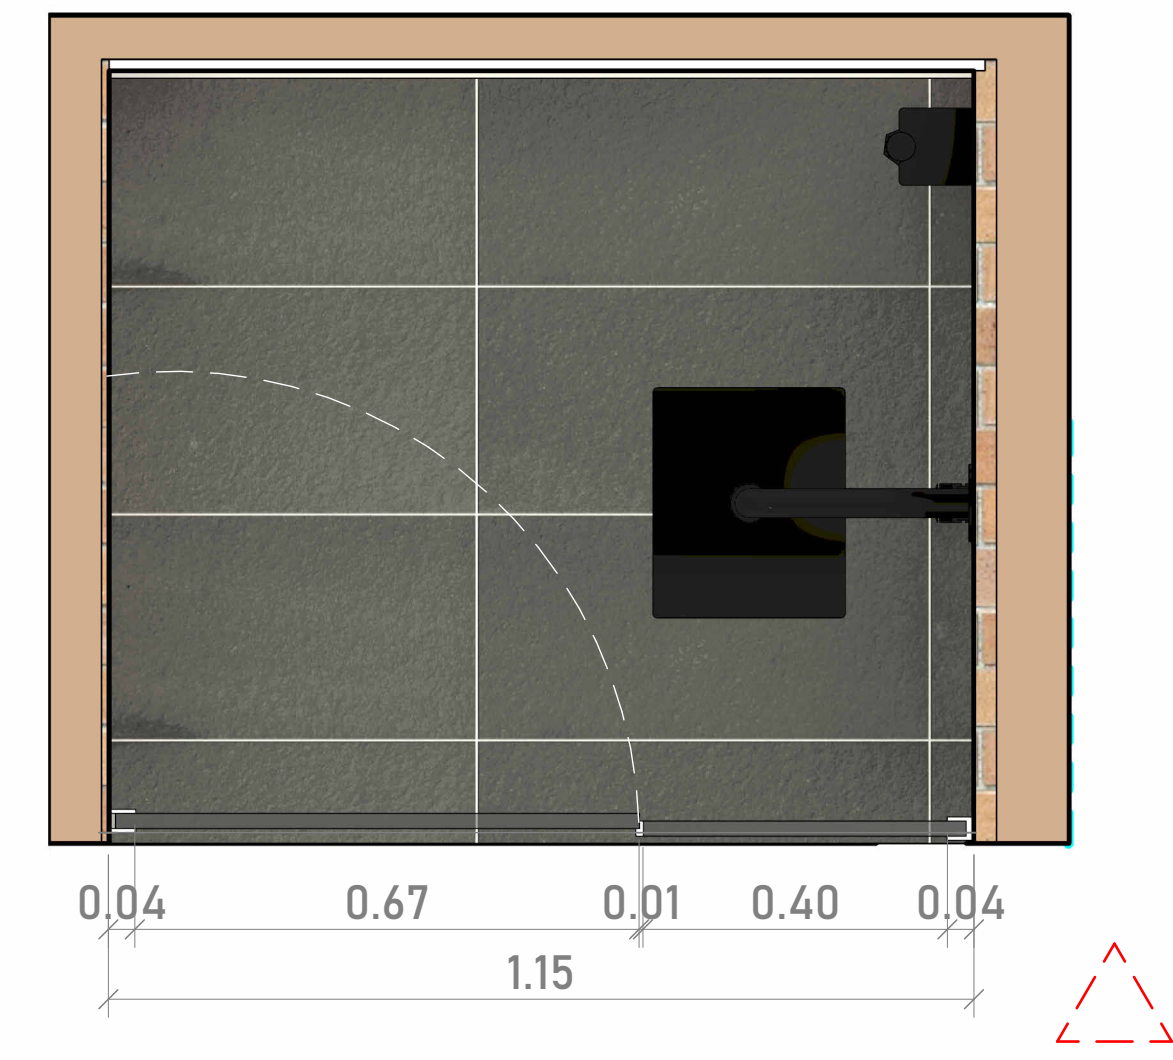


4 CABINA DUCHA HAB SERVICIO
1: 10

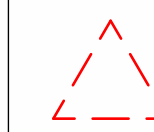

NOTA: TODAS LAS VISTAS EN ISOMETRICO
ESTAN ORIENTADAS DESDE LA PARTE
EXTERIOR


idea/base. ARQUITECTOS	
Proyecto: HARAS	
Matricula inmobiliaria: No 020-238645	
Parcelación: Parcelación Haras Campestre – P.H.	
Número de lote: Lote No. 4 Llanogrande	
Observaciones: Según NSR-10	
Revisa: ANA SOFIA ROLDAN	
Verifica: DANIELA ARIZA RAMIREZ	
Aprueba: DANIELA ARIZA RAMIREZ	
Cliente: SANDRA MEJIA VELEZ Y EDWIN ALFREDO ACOSTA	
Diseño: DANIELA ARIZA RAMIREZ	
Cálculos estructurales:	
Archivo de Referencia: 20251212_DISEÑO HARAS	
Contiene: CARP. METÁLICA DETALLES	
Escala: 1:10	Fecha: 2025/22/12
Dibujo: JORDY PINEDA BELLIDO	
Plancha N°: A 1	De: 9
Firmas:	

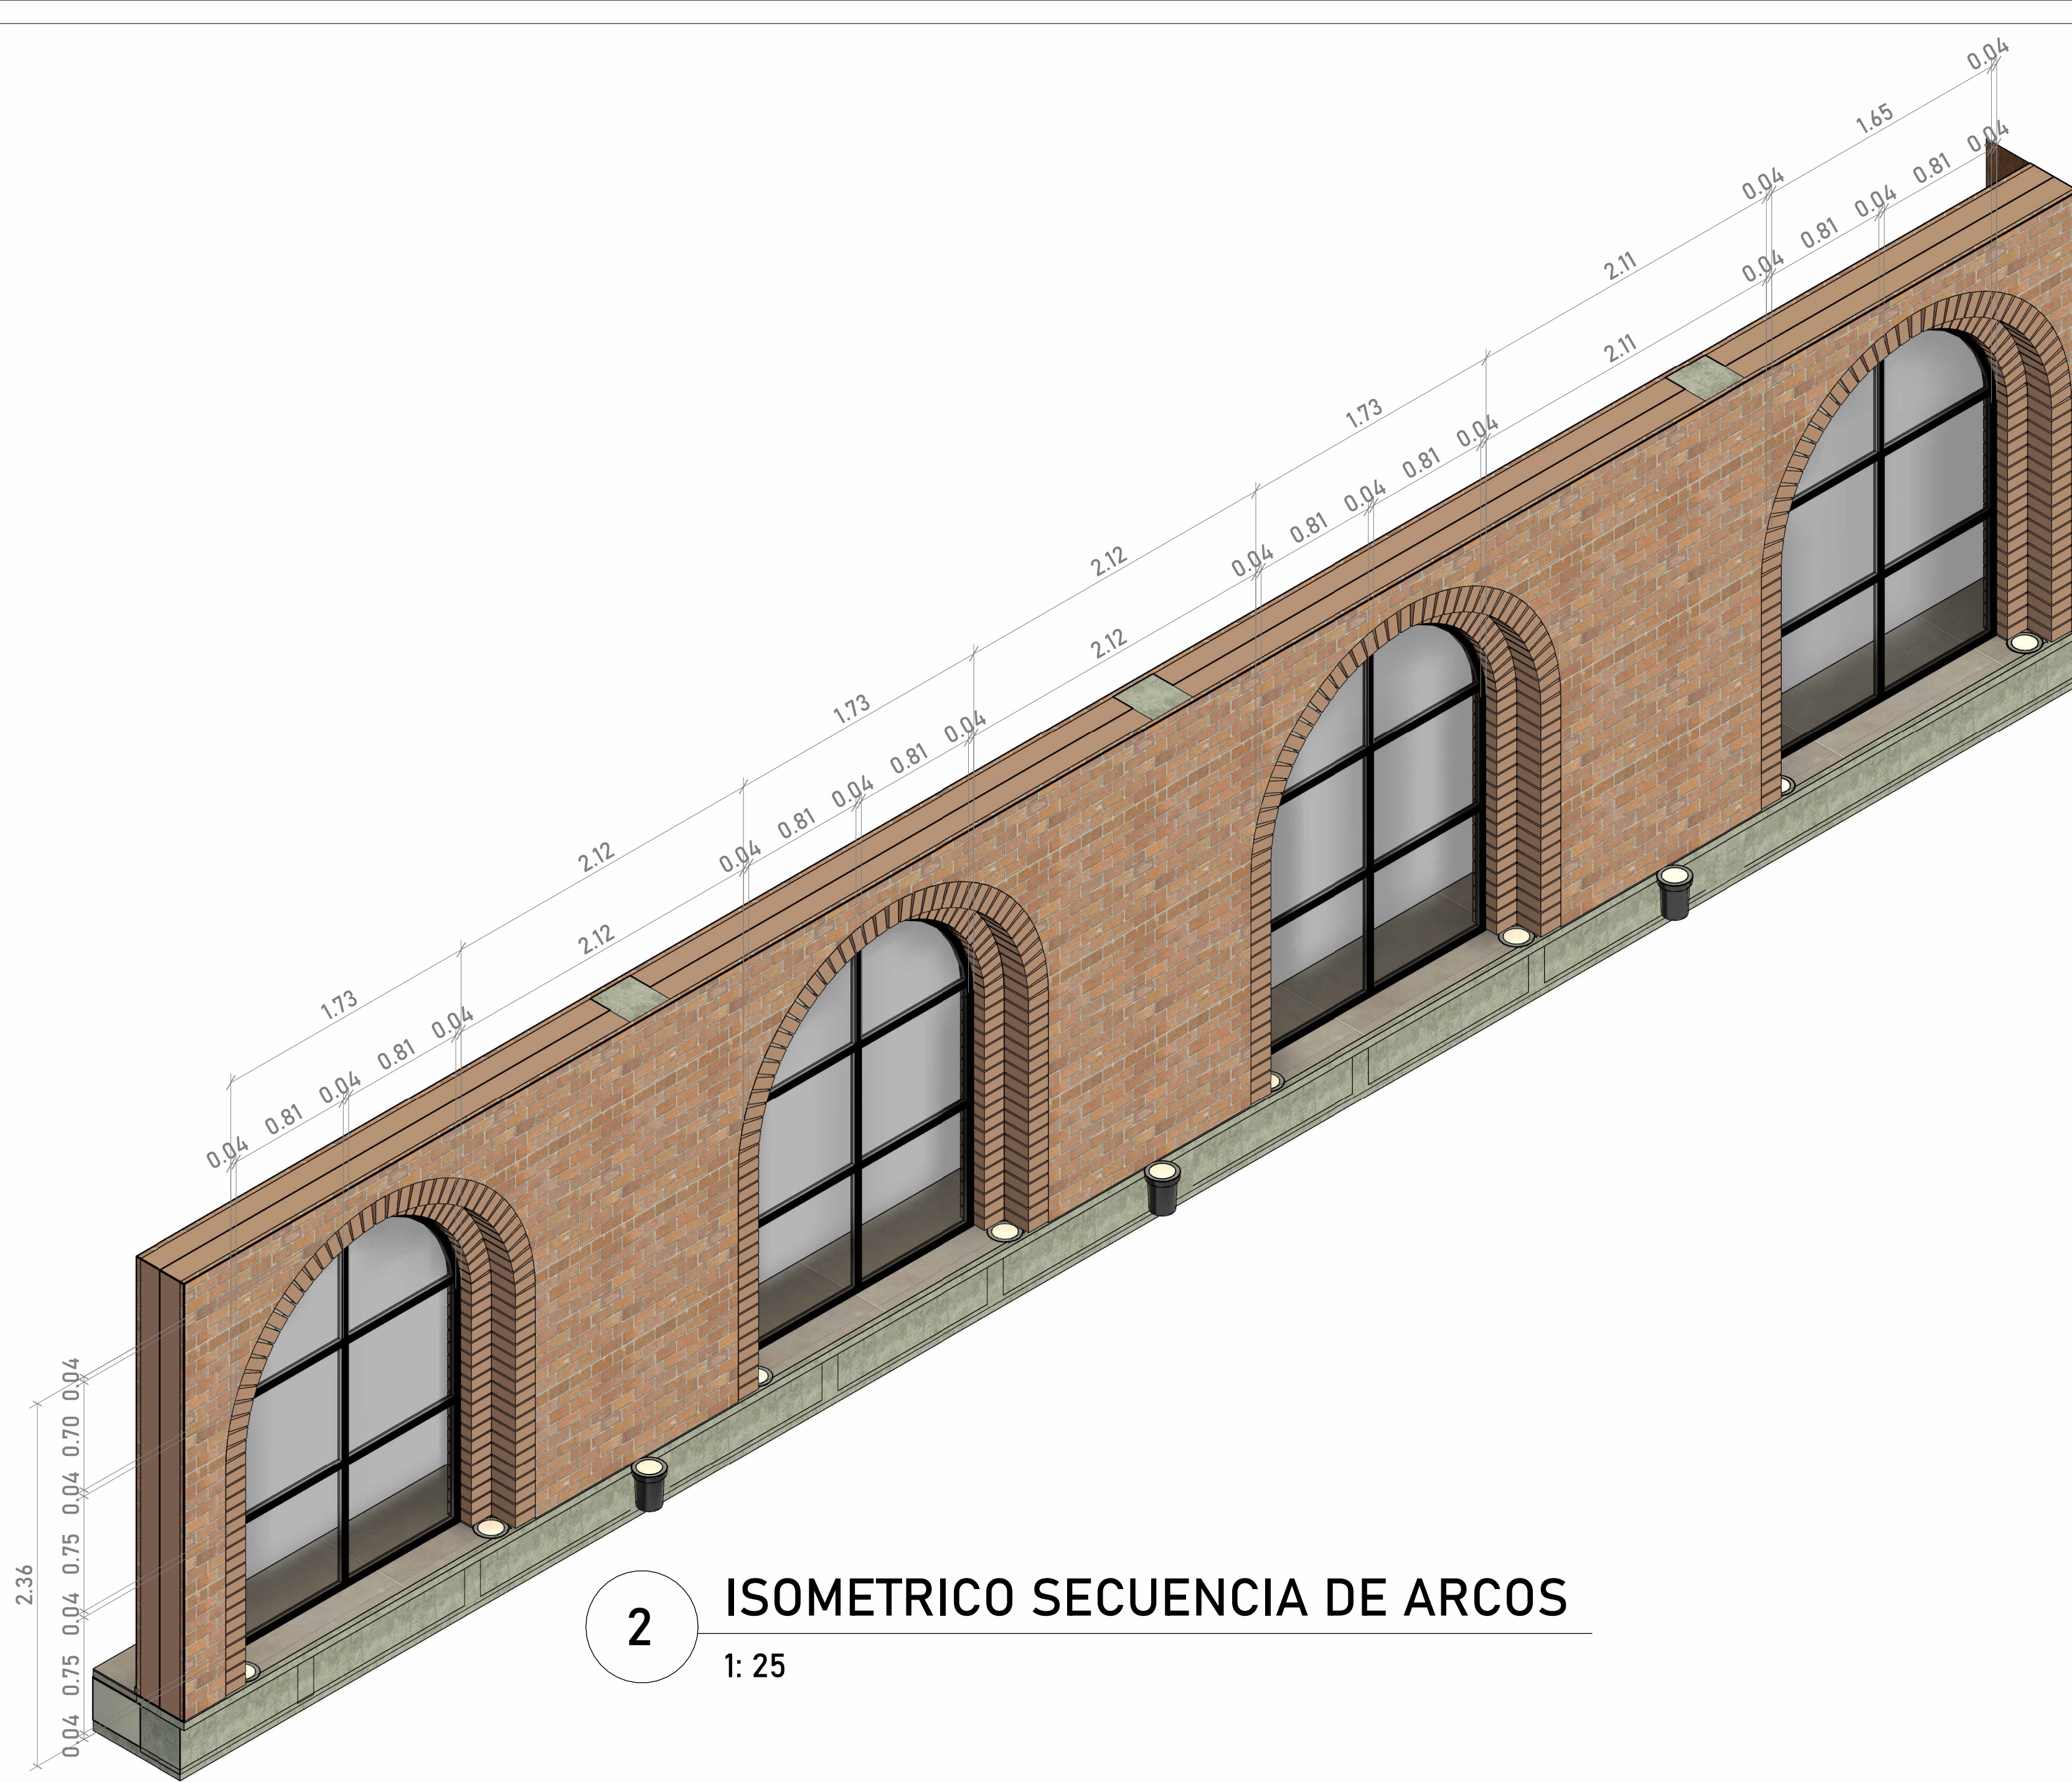


2 ISOMETRICO SECUENCIA DE ARCOS
1: 25



2 IMAGEN REFERENTE ARCOS

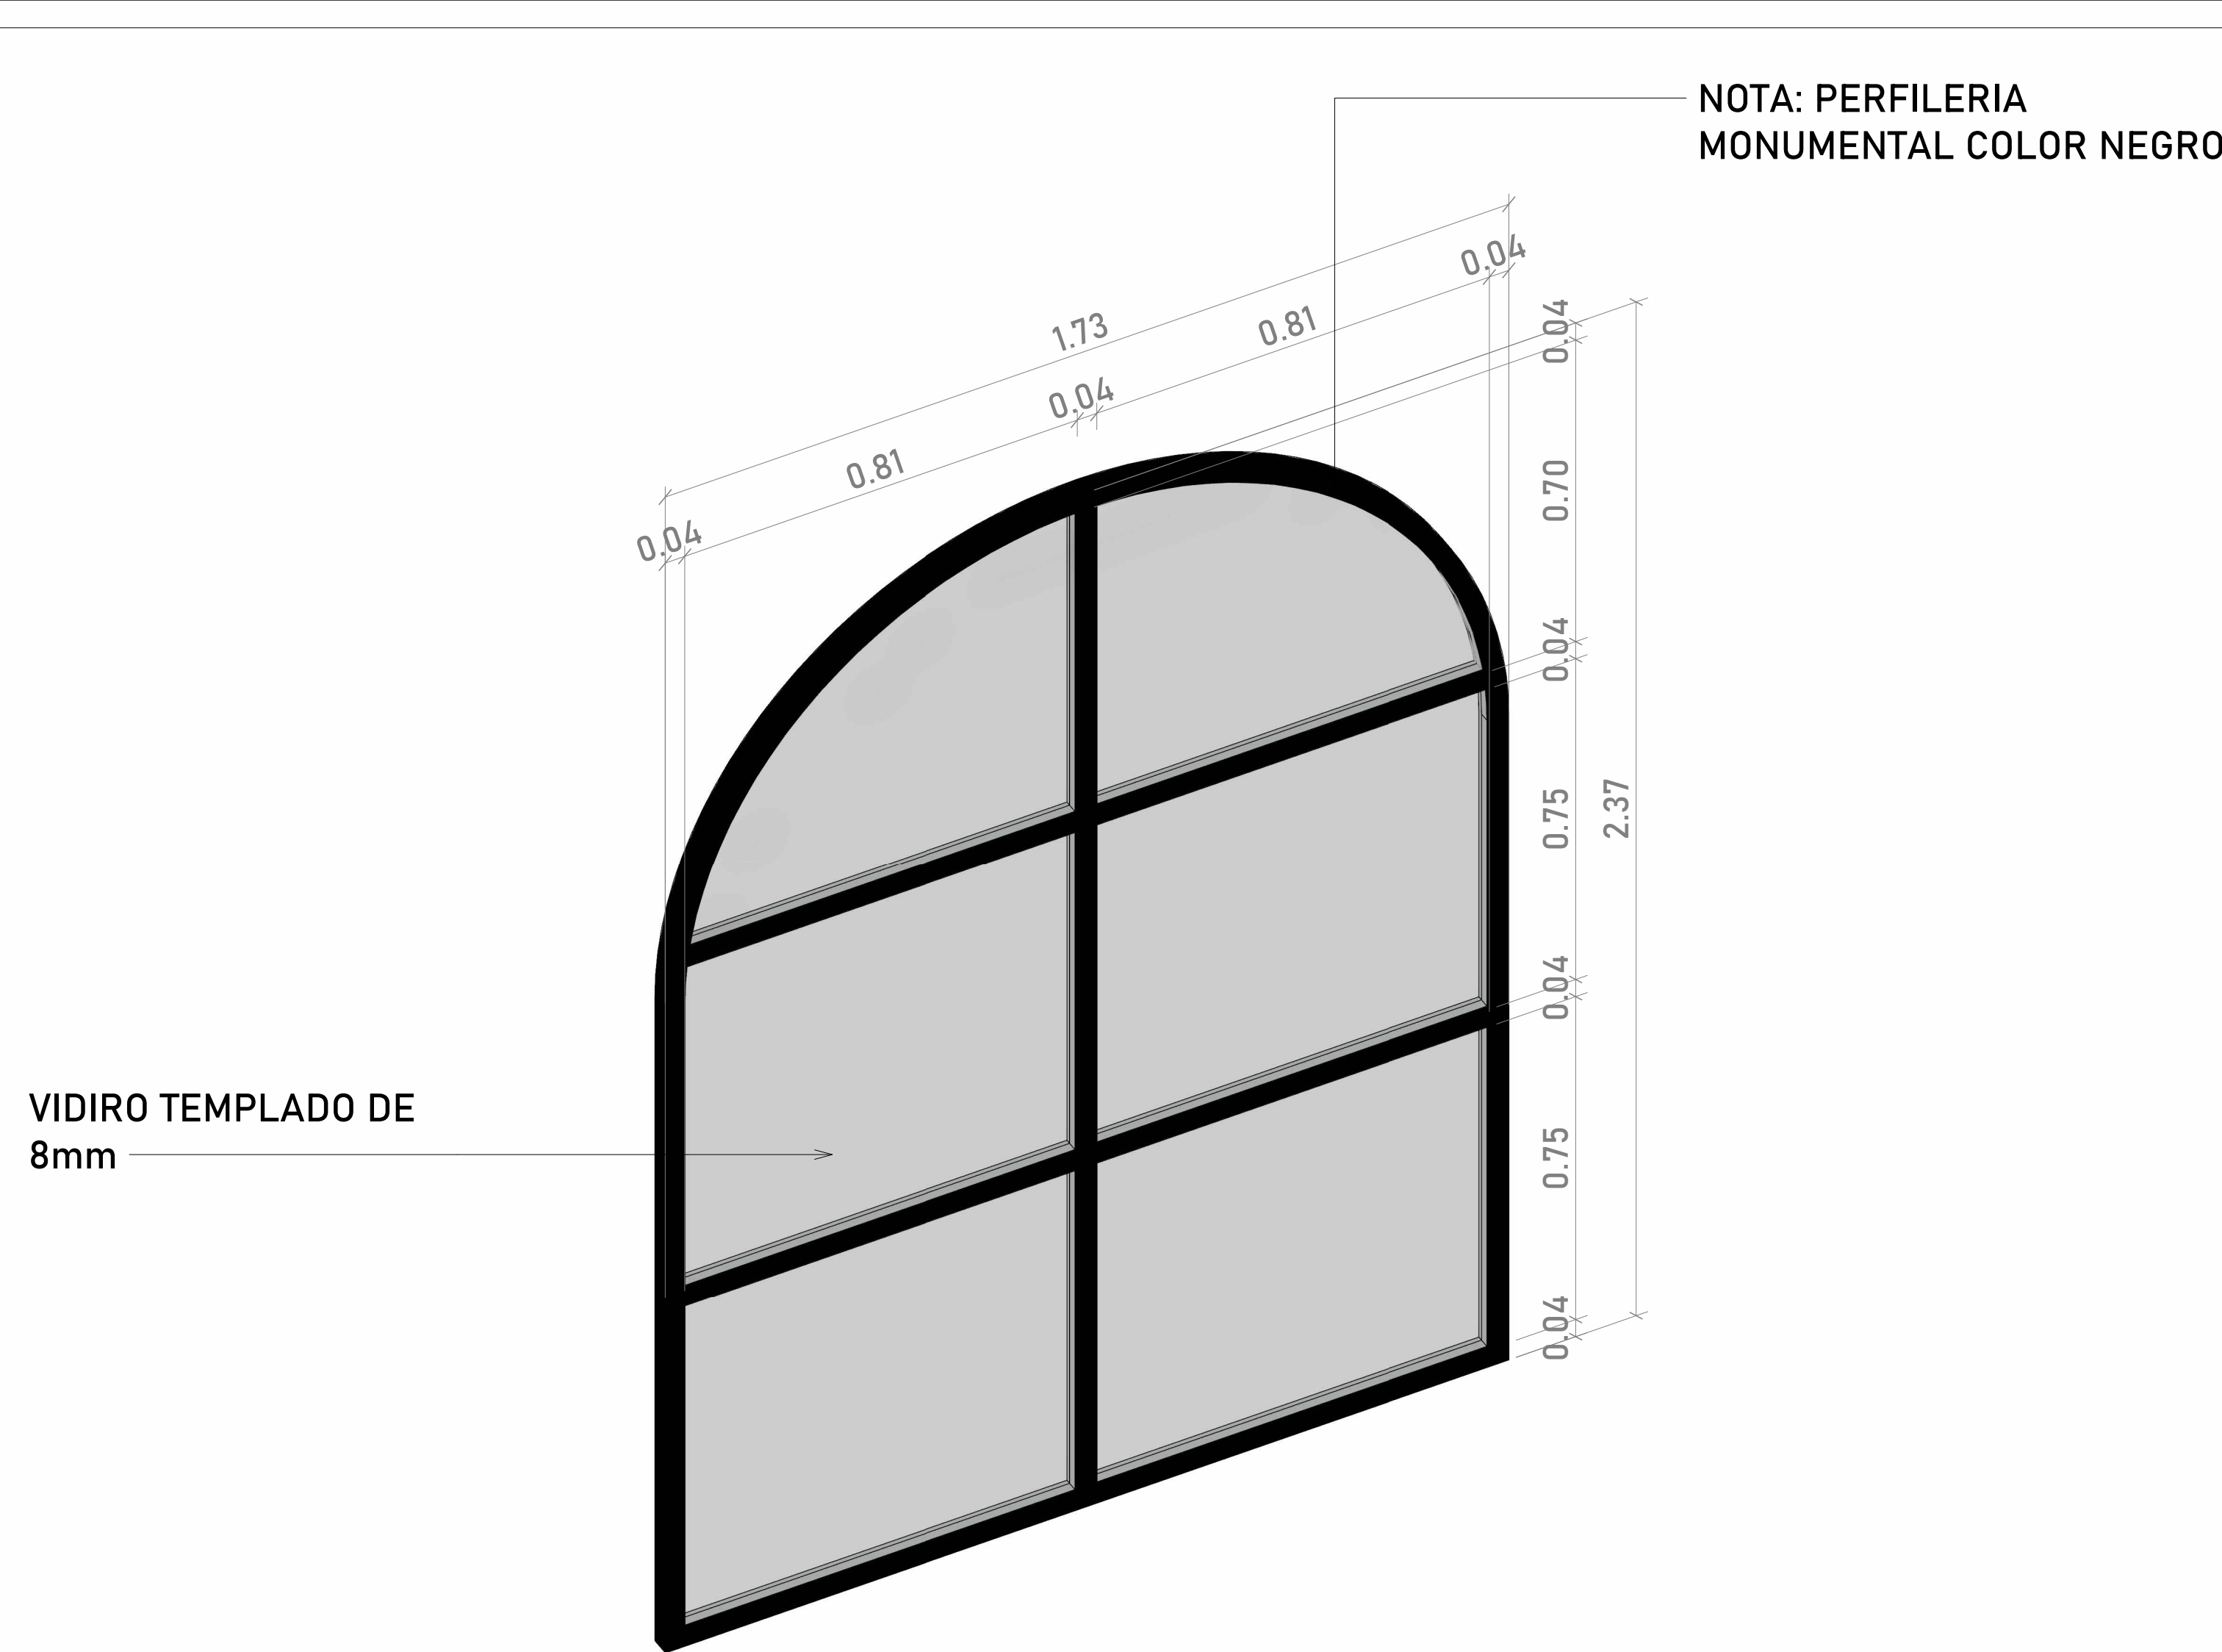

1 ISOMETRICO ARCO PERFILERIA METÁLICA
1: 10

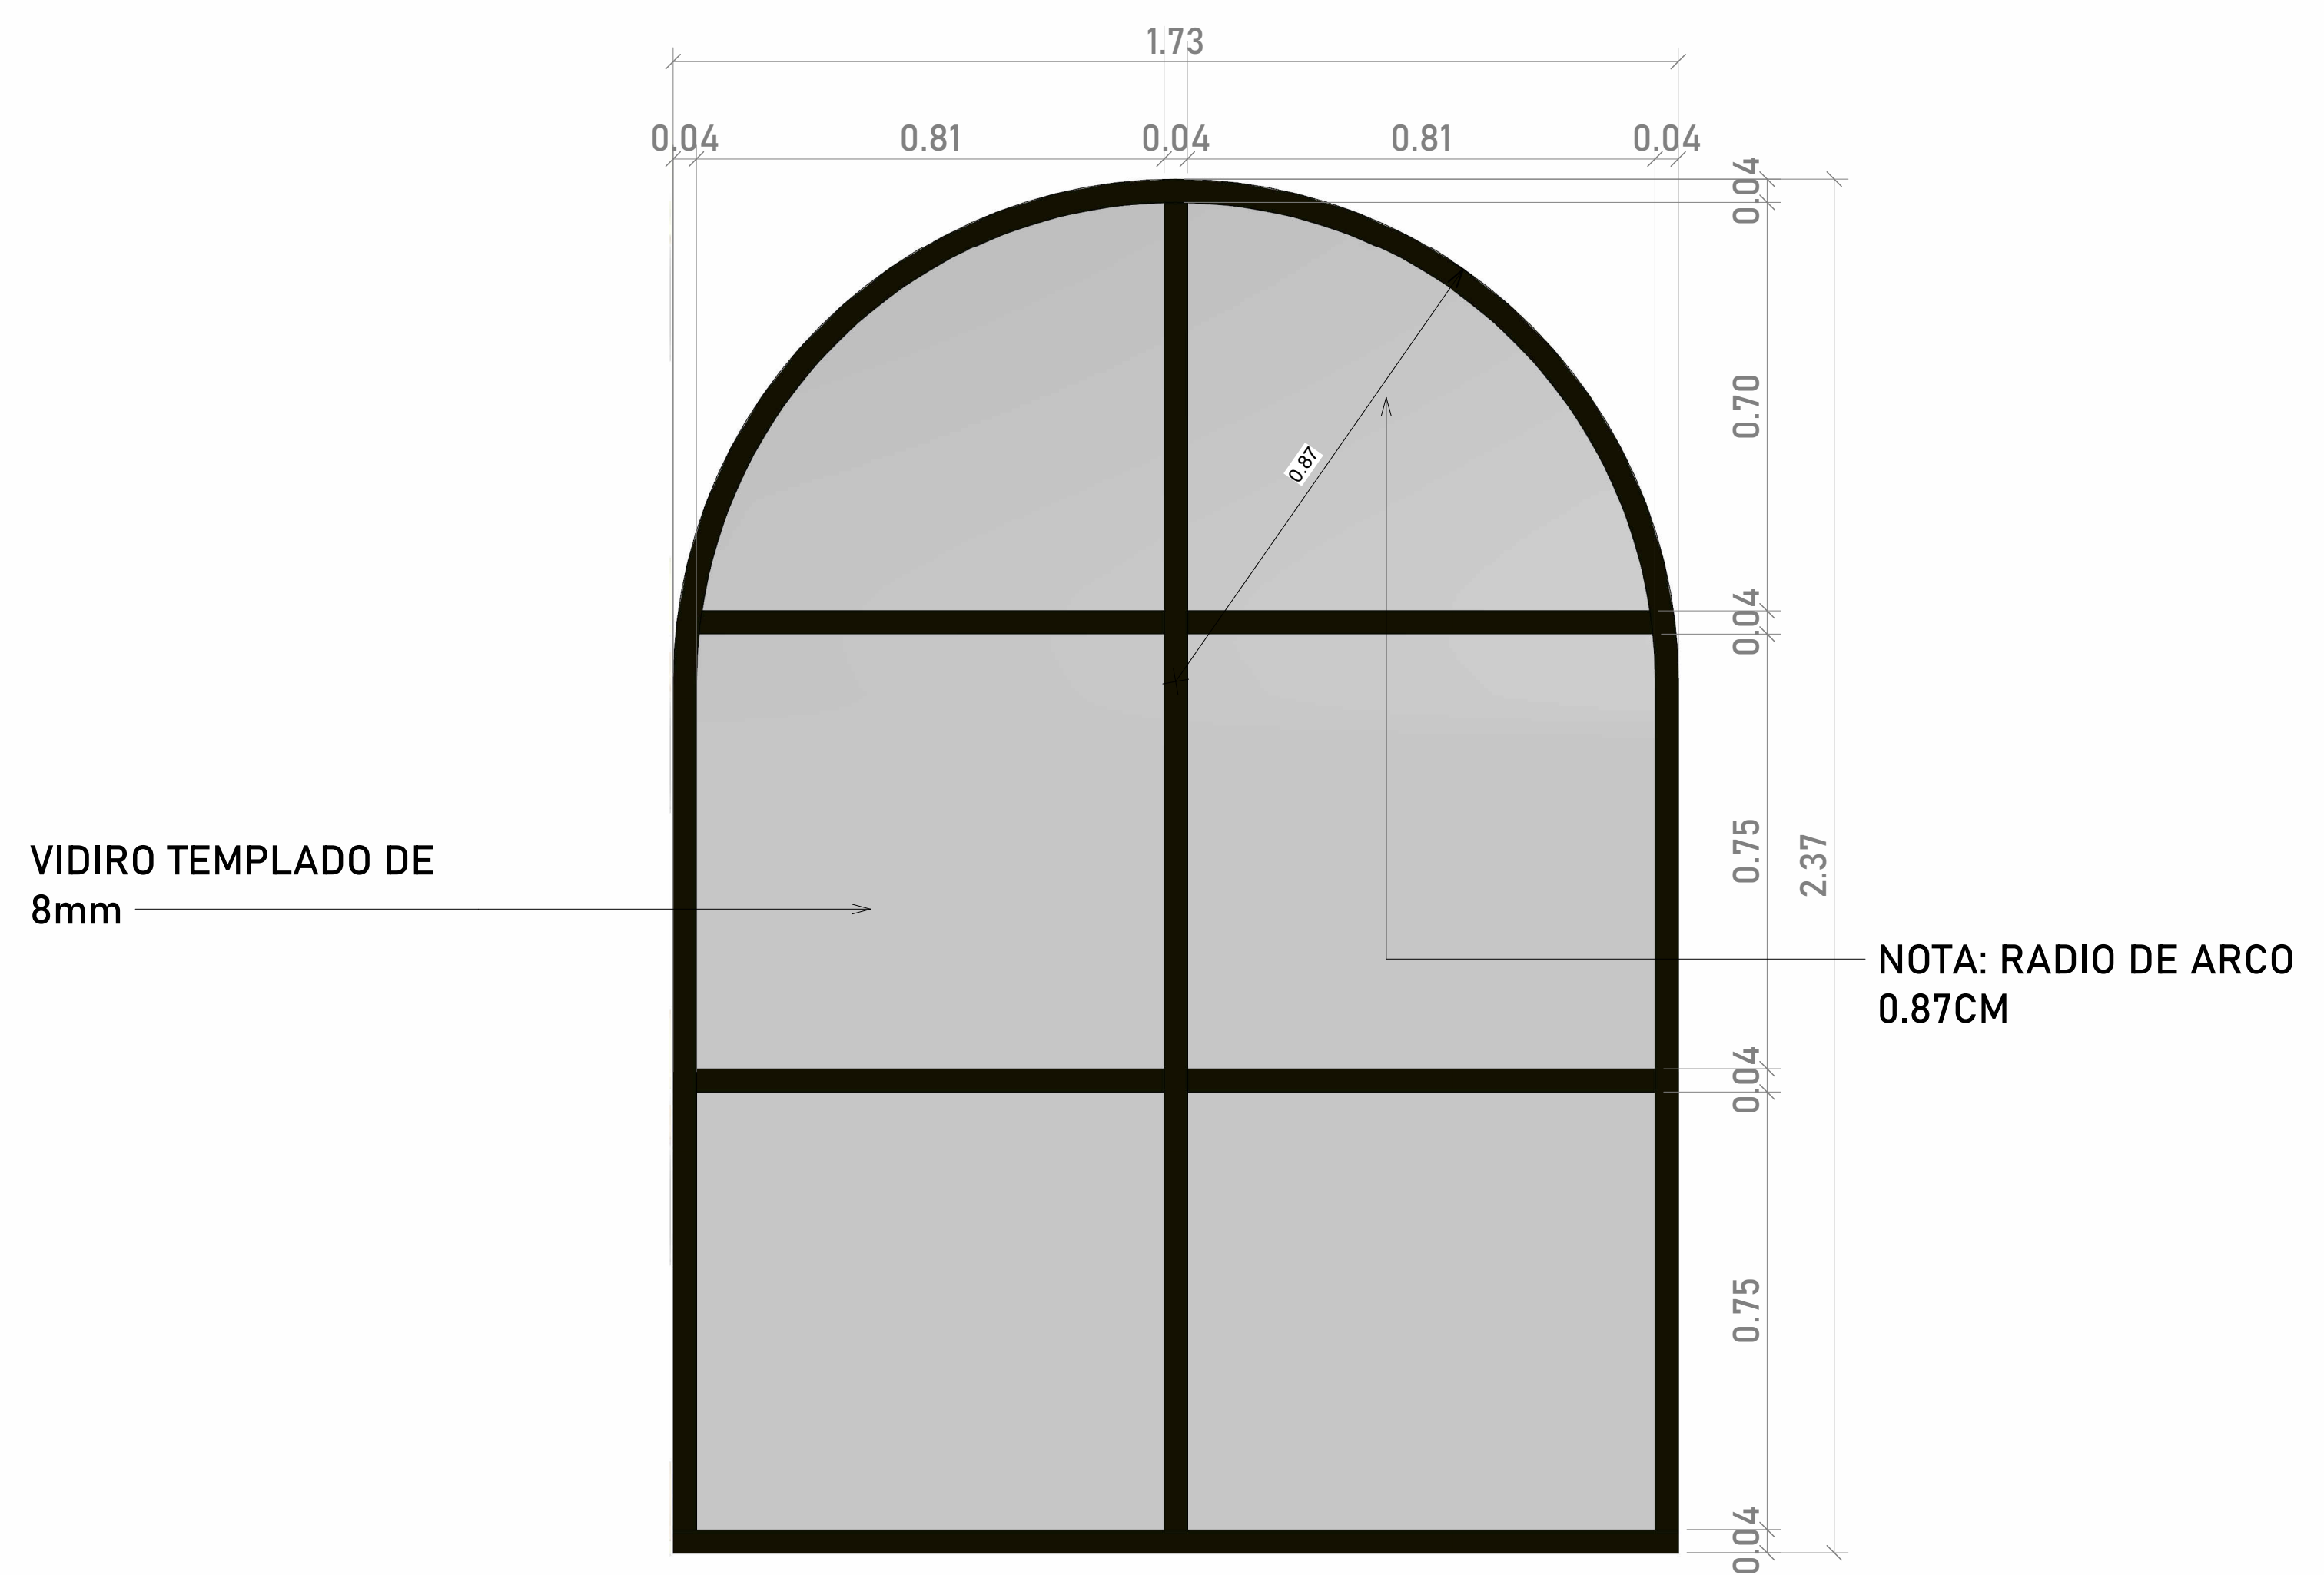

1 ALZADO ARCO PERFILERIA METÁLICA
1: 10

NOTA: CANTIDAD VENTANALES CON ARCO METALICO COLOR NEGRO 6 UND

idea/base. ARQUITECTOS	
Proyecto: HARAS	
Matricula inmobiliaria: No 020-238645	
Parcelación: Parcelación Haras Campestre – P.H.	
Número de lote: Lote No. 4 Llanogrande	
Observaciones: Según NSR-10	
Revisa: ANA SOFIA ROLDAN	
Verifica: DANIELA ARIZA RAMIREZ	
Aprueba: DANIELA ARIZA RAMIREZ	
Cliente: SANDRA MEJIA VELEZ Y EDWIN ALFREDO ACOSTA	
Diseño: DANIELA ARIZA RAMIREZ	
Cálculos estructurales: 12/03/25	
Archivo de Referencia: 20251212_DISEÑO HARAS	
Contiene: CARP. METÁLICA ARCOS	
Escala: 1:10	Fecha: 2025/22/12
Dibujo: JORDY PINEDA BELLIDO	
Plancha N°: A 2	De: 9
Firmas:	

Proyecto:

HARAS

Matricula inmobiliaria:

No 020-238645

Parcelación:

Parcelación Haras
Campestre – P.H.

Número de lote:

Lote No. 4 Llanogrande

Observaciones:

Según NSR-10

Revisa:

ANA SOFIA ROLDAN

Verifica:

DANIELA ARIZA RAMIREZ

Aprueba:

DANIELA ARIZA RAMIREZ

Cliente:

SANDRA MEJIA VELEZ Y
EDWIN ALFREDO ACOSTA

Diseño:

DANIELA ARIZA RAMIREZ

Cálculos estructurales:

12/03/25

Archivo de Referencia:

20251212_DISEÑO HARAS

Contiene:

CARP. METÁLICA PUERTA
CORREDIZA SALA CHIMENEA

Escala:

1:10

Fecha:

2025/22/12

Dibujo:

JORDY PINEDA BELLIDO


Plancha N°:

A 3

De:

9


Firmas:

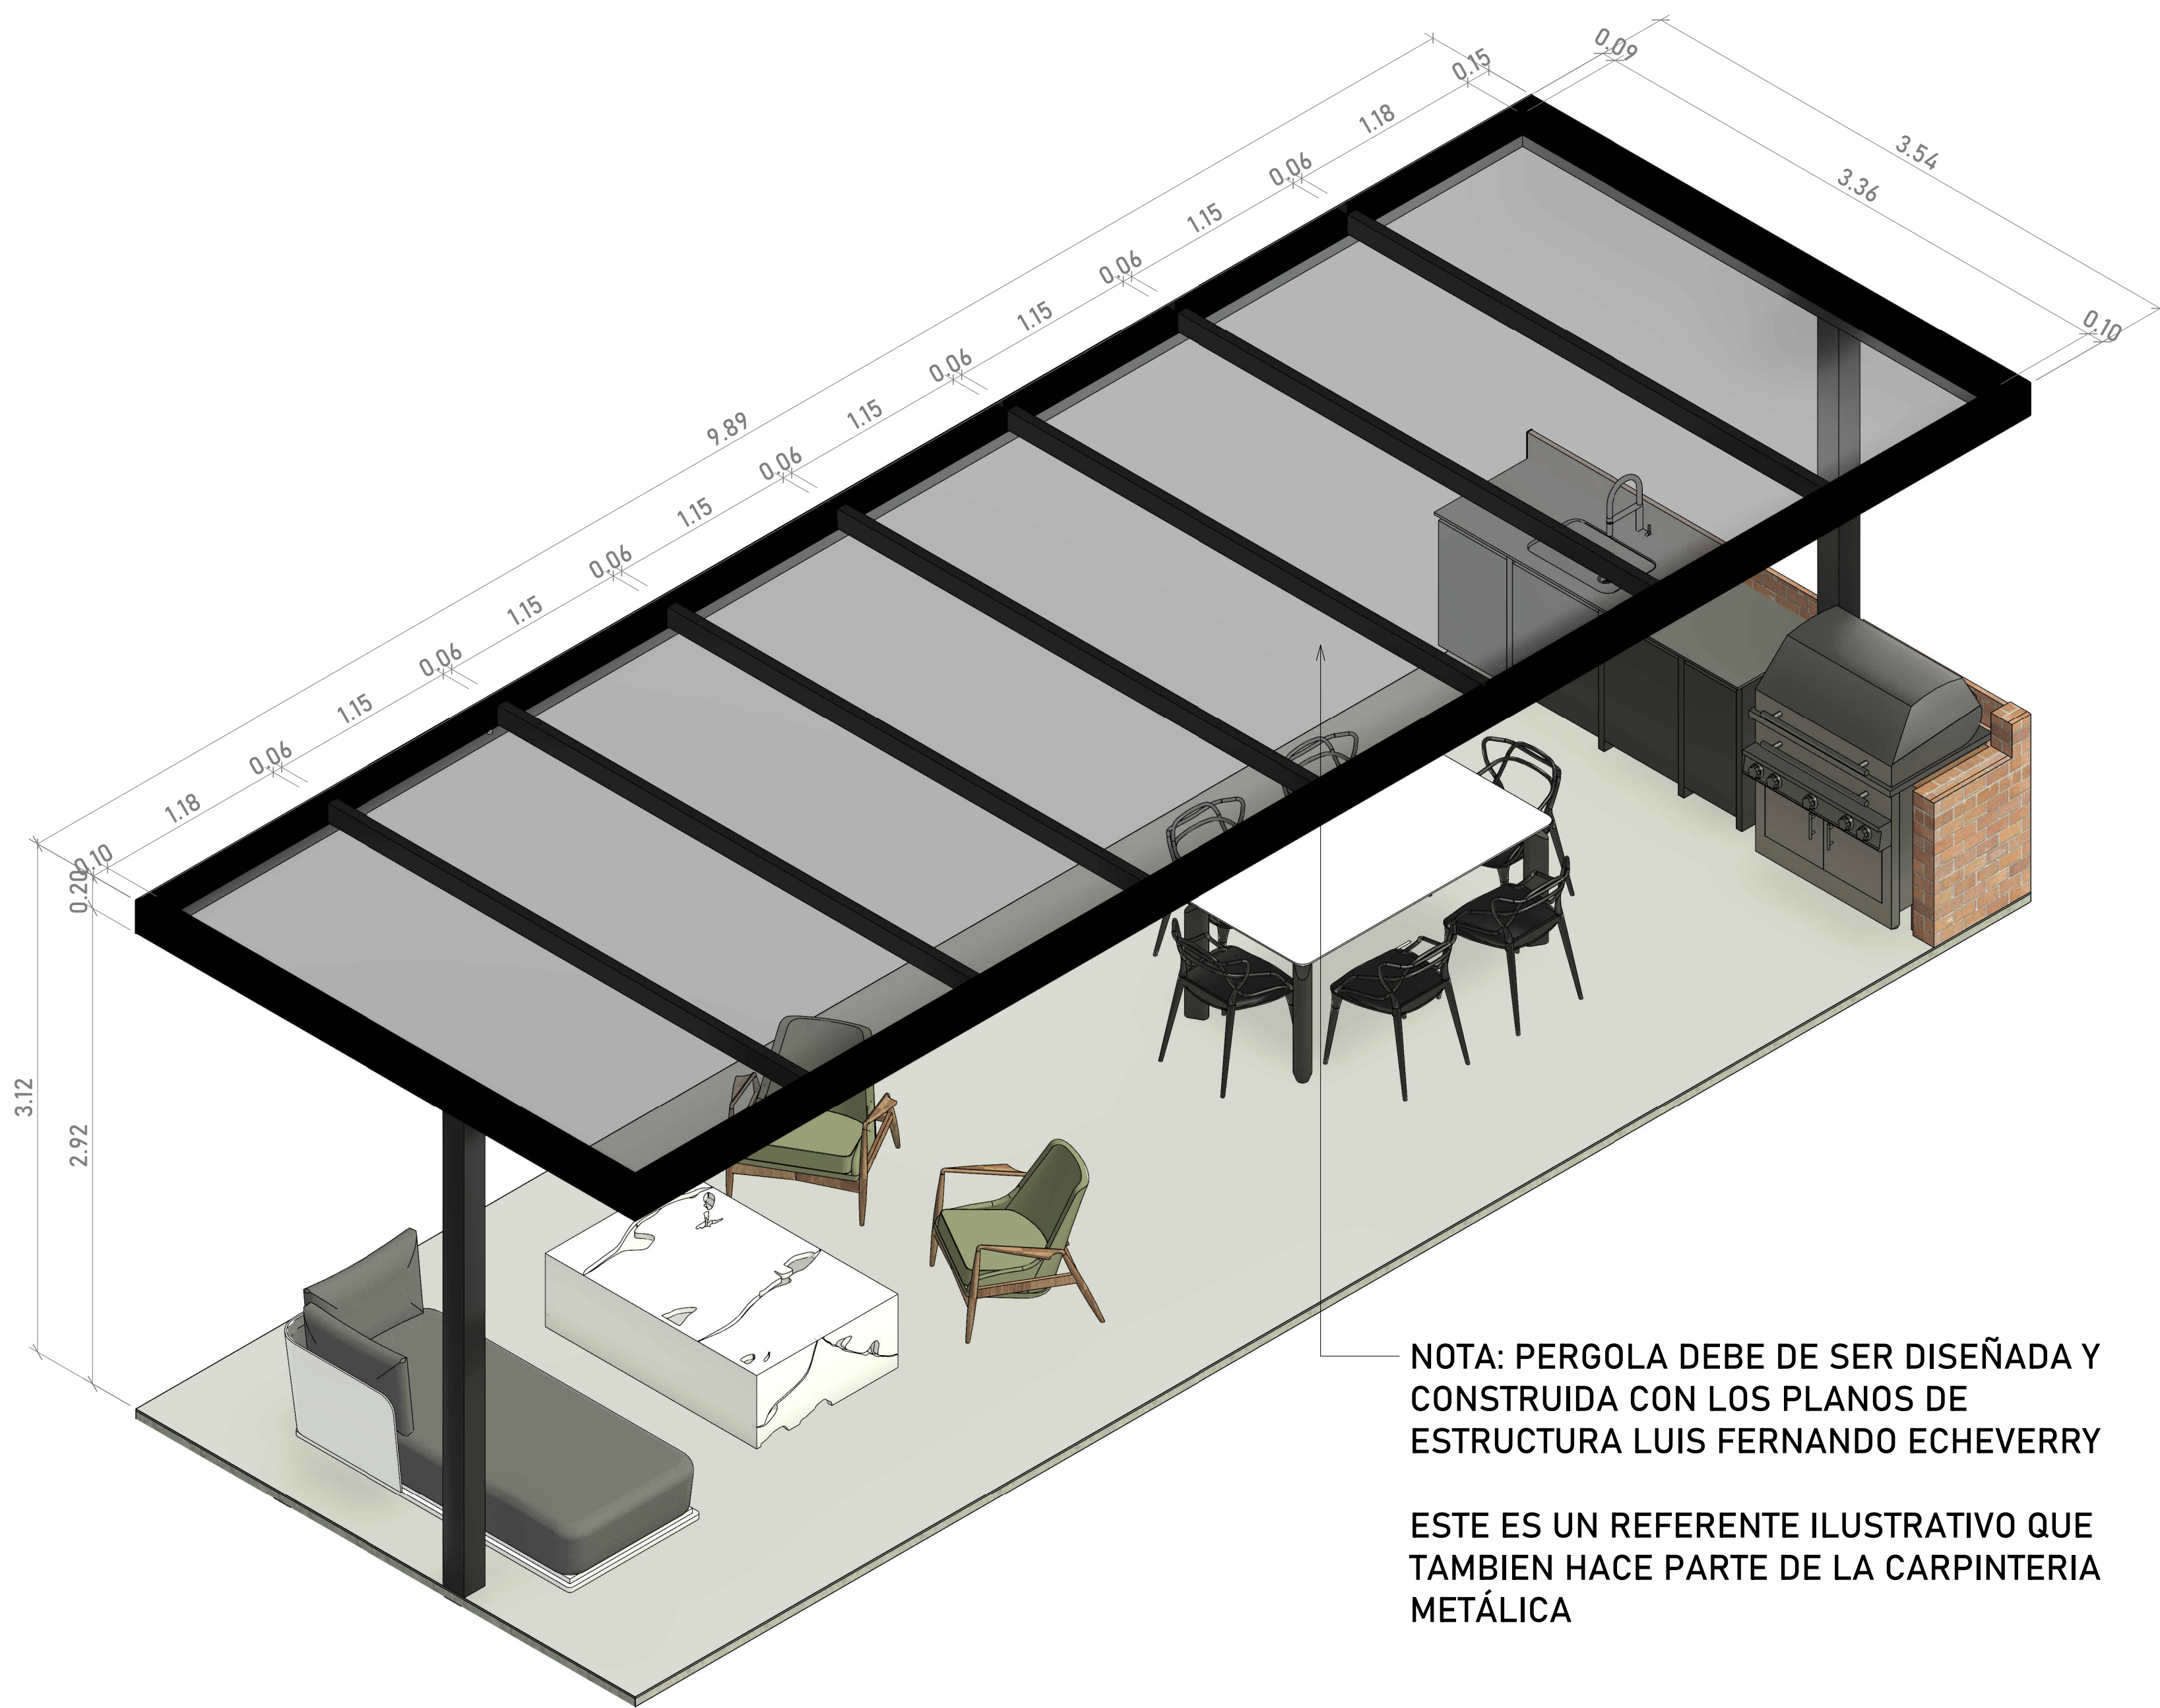

1

ISOMETRICO PERGOLA PERFILERIA METÁLICA

1: 25

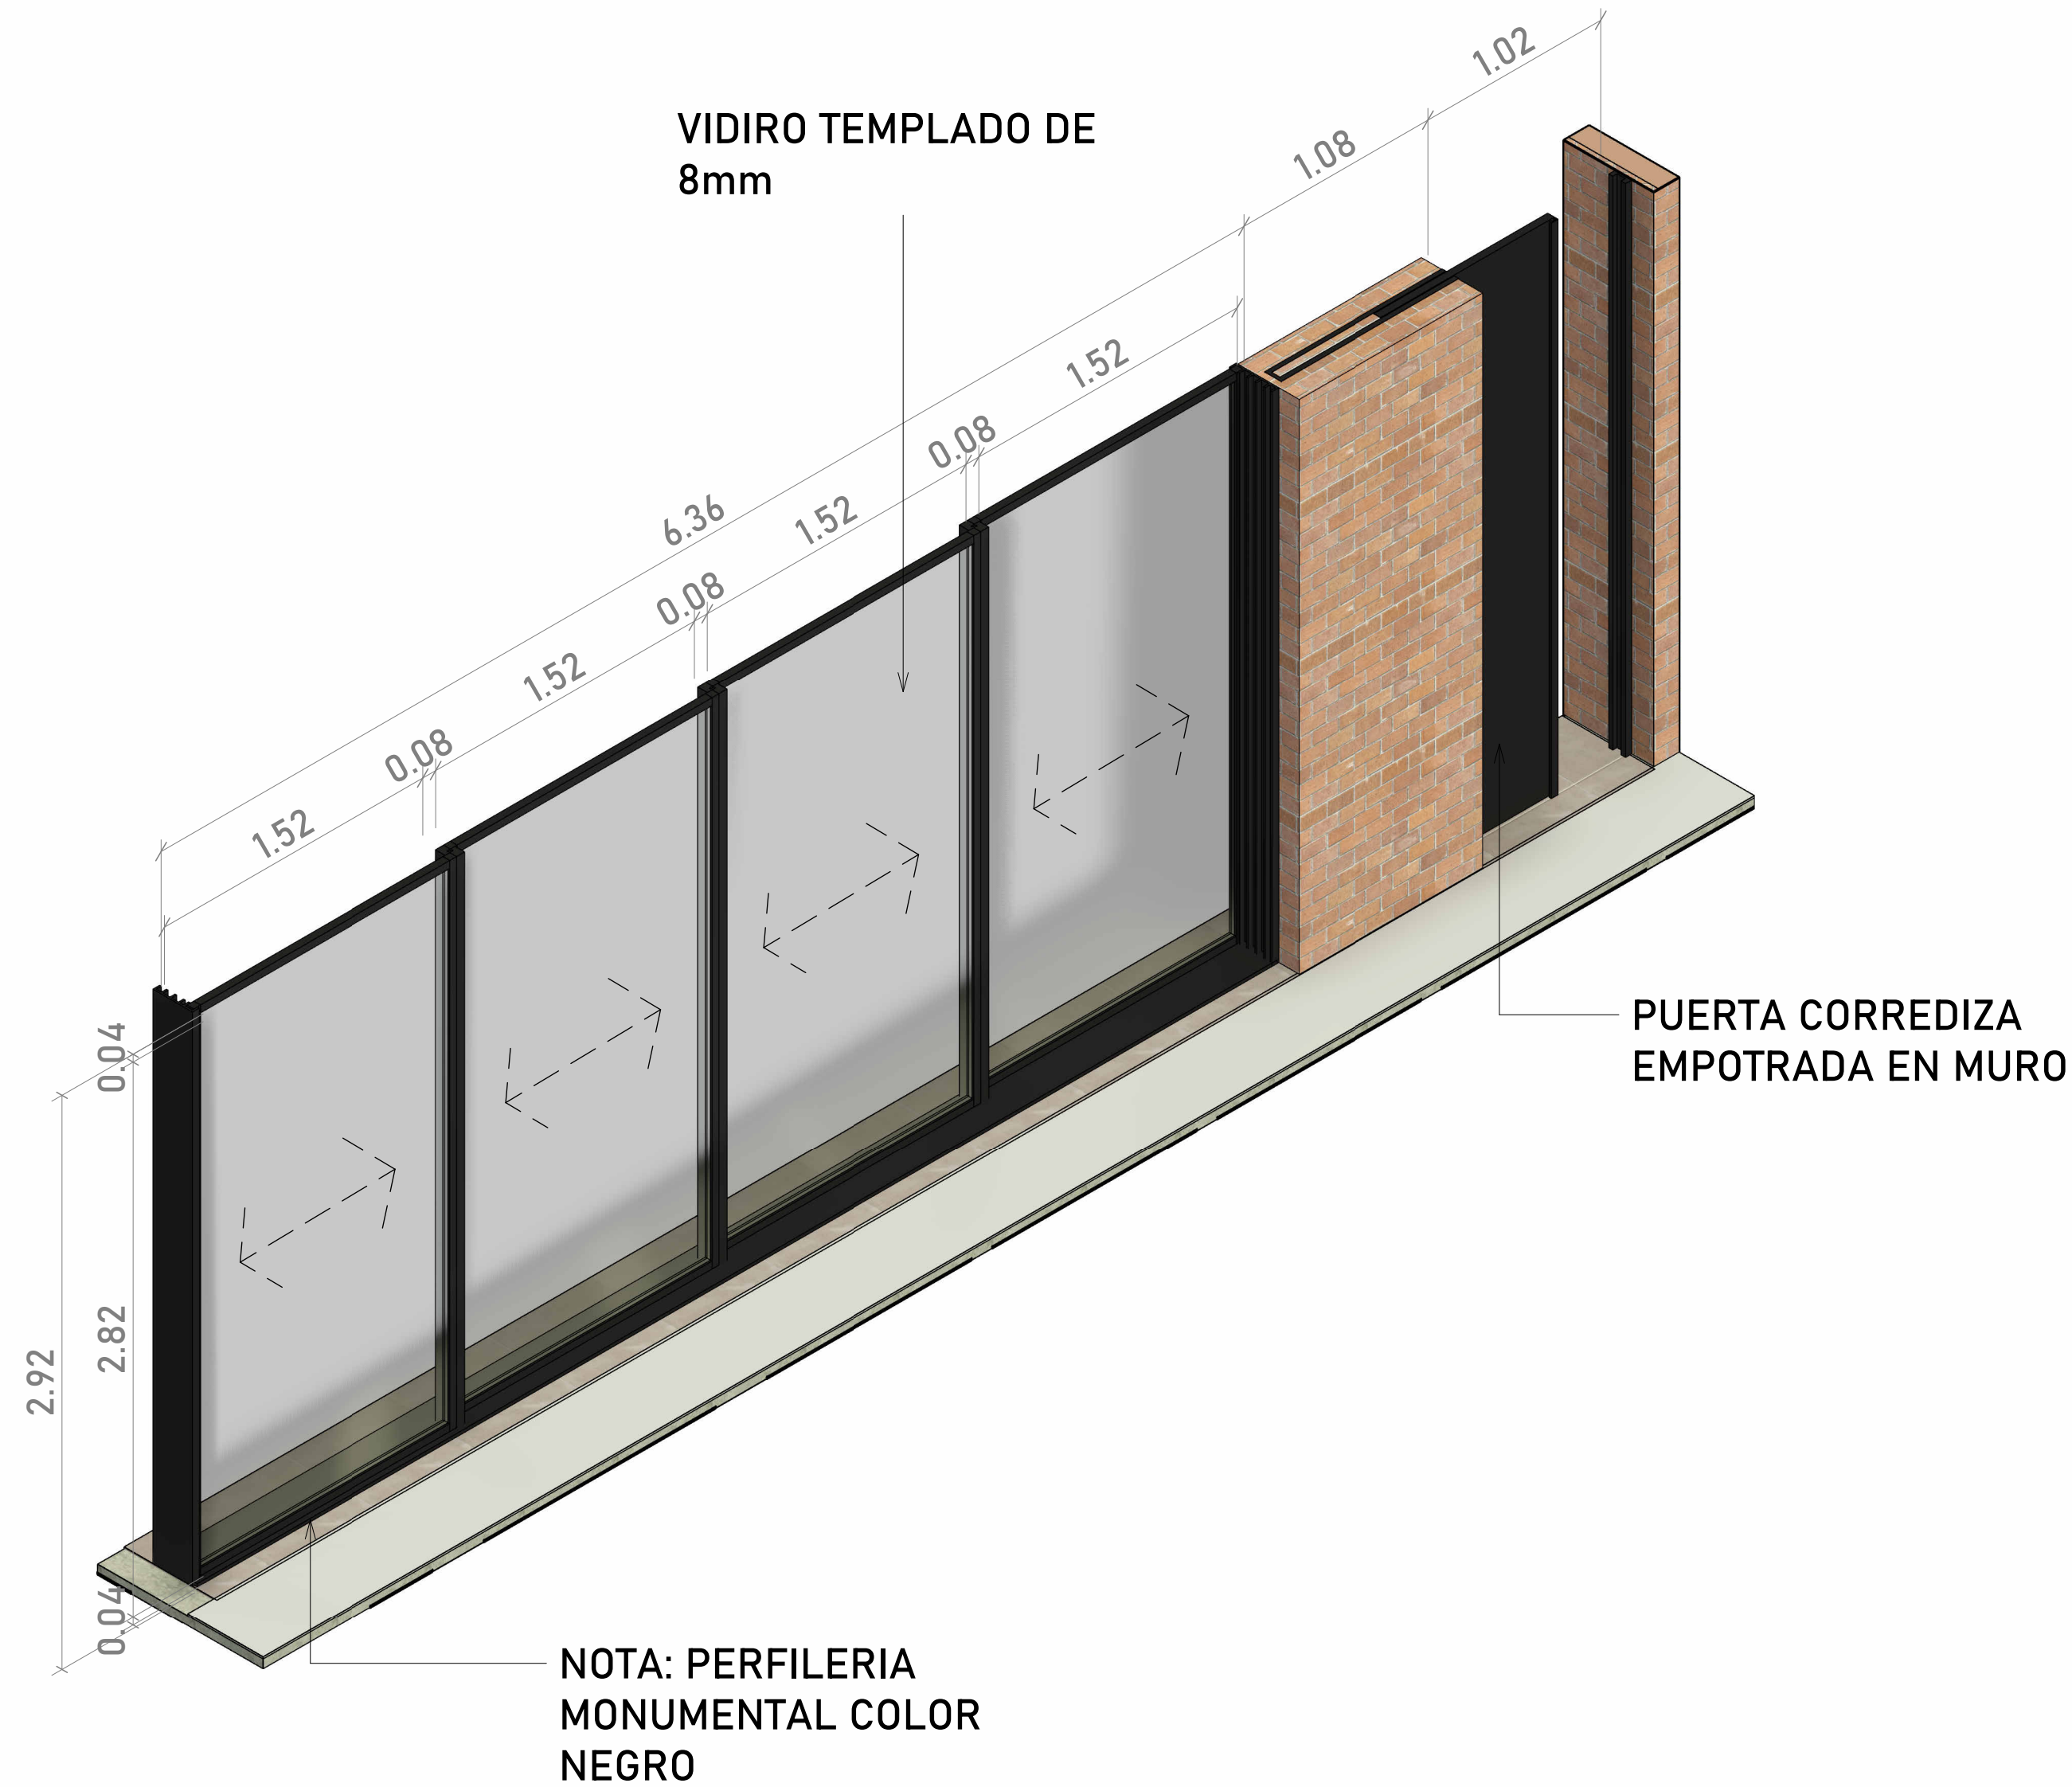

2

ISOMETRICO PUERTA CORREDIZA Y PUERTA BATIENTE


1: 25



1

PLANTA PERGOLA PERFILERIA METÁLICA


1: 25

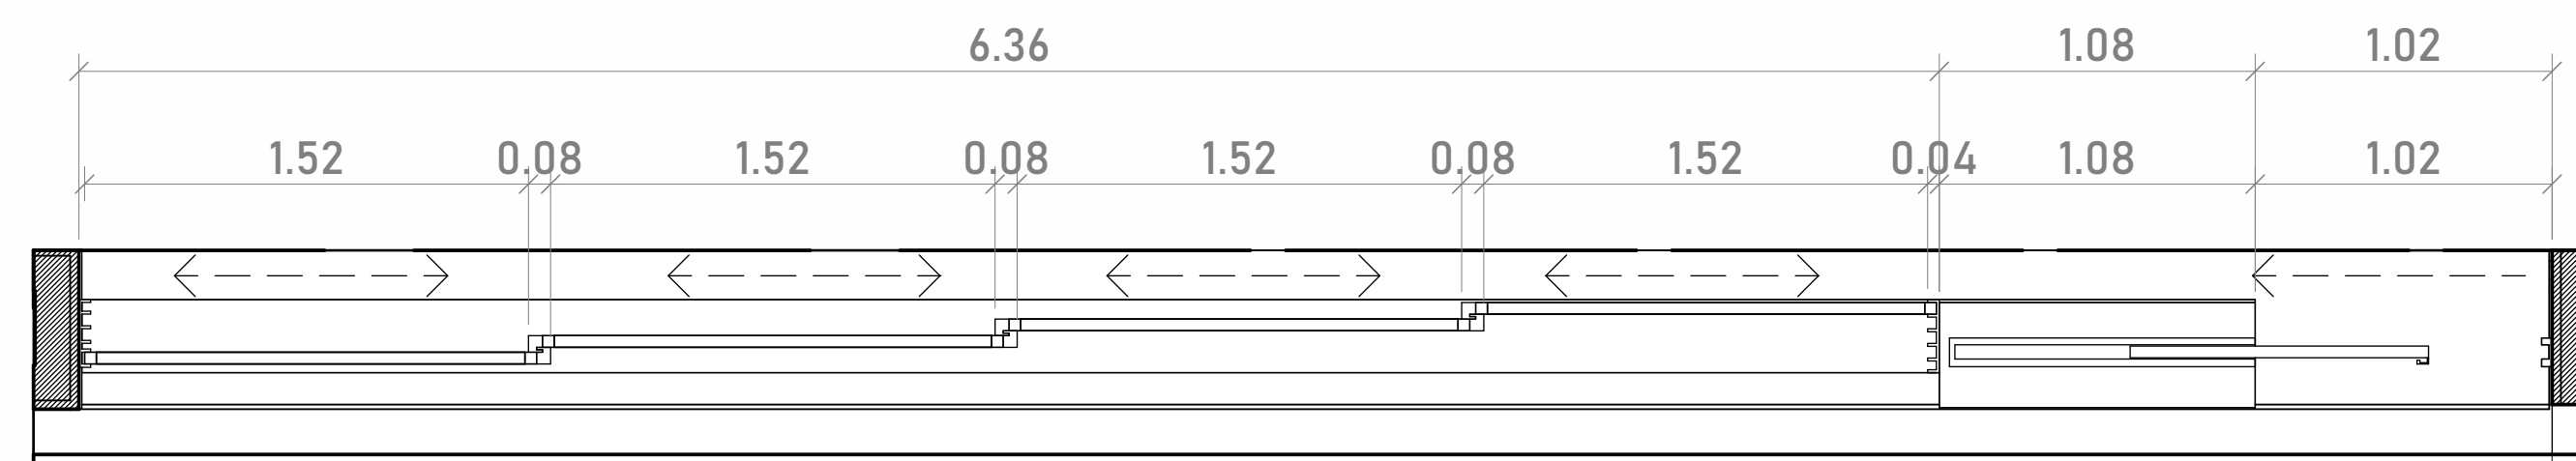

2


ALZADO PUERTA CORREDIZA Y PUERTA BATIENTE

1: 25

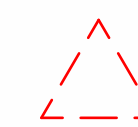


NOTA: TODAS LAS VISTAS EN ISOMETRICO ESTAN ORIENTADAS DESDE LA PARTE EXTERIOR

VIDRIO TEMPLADO
8mm

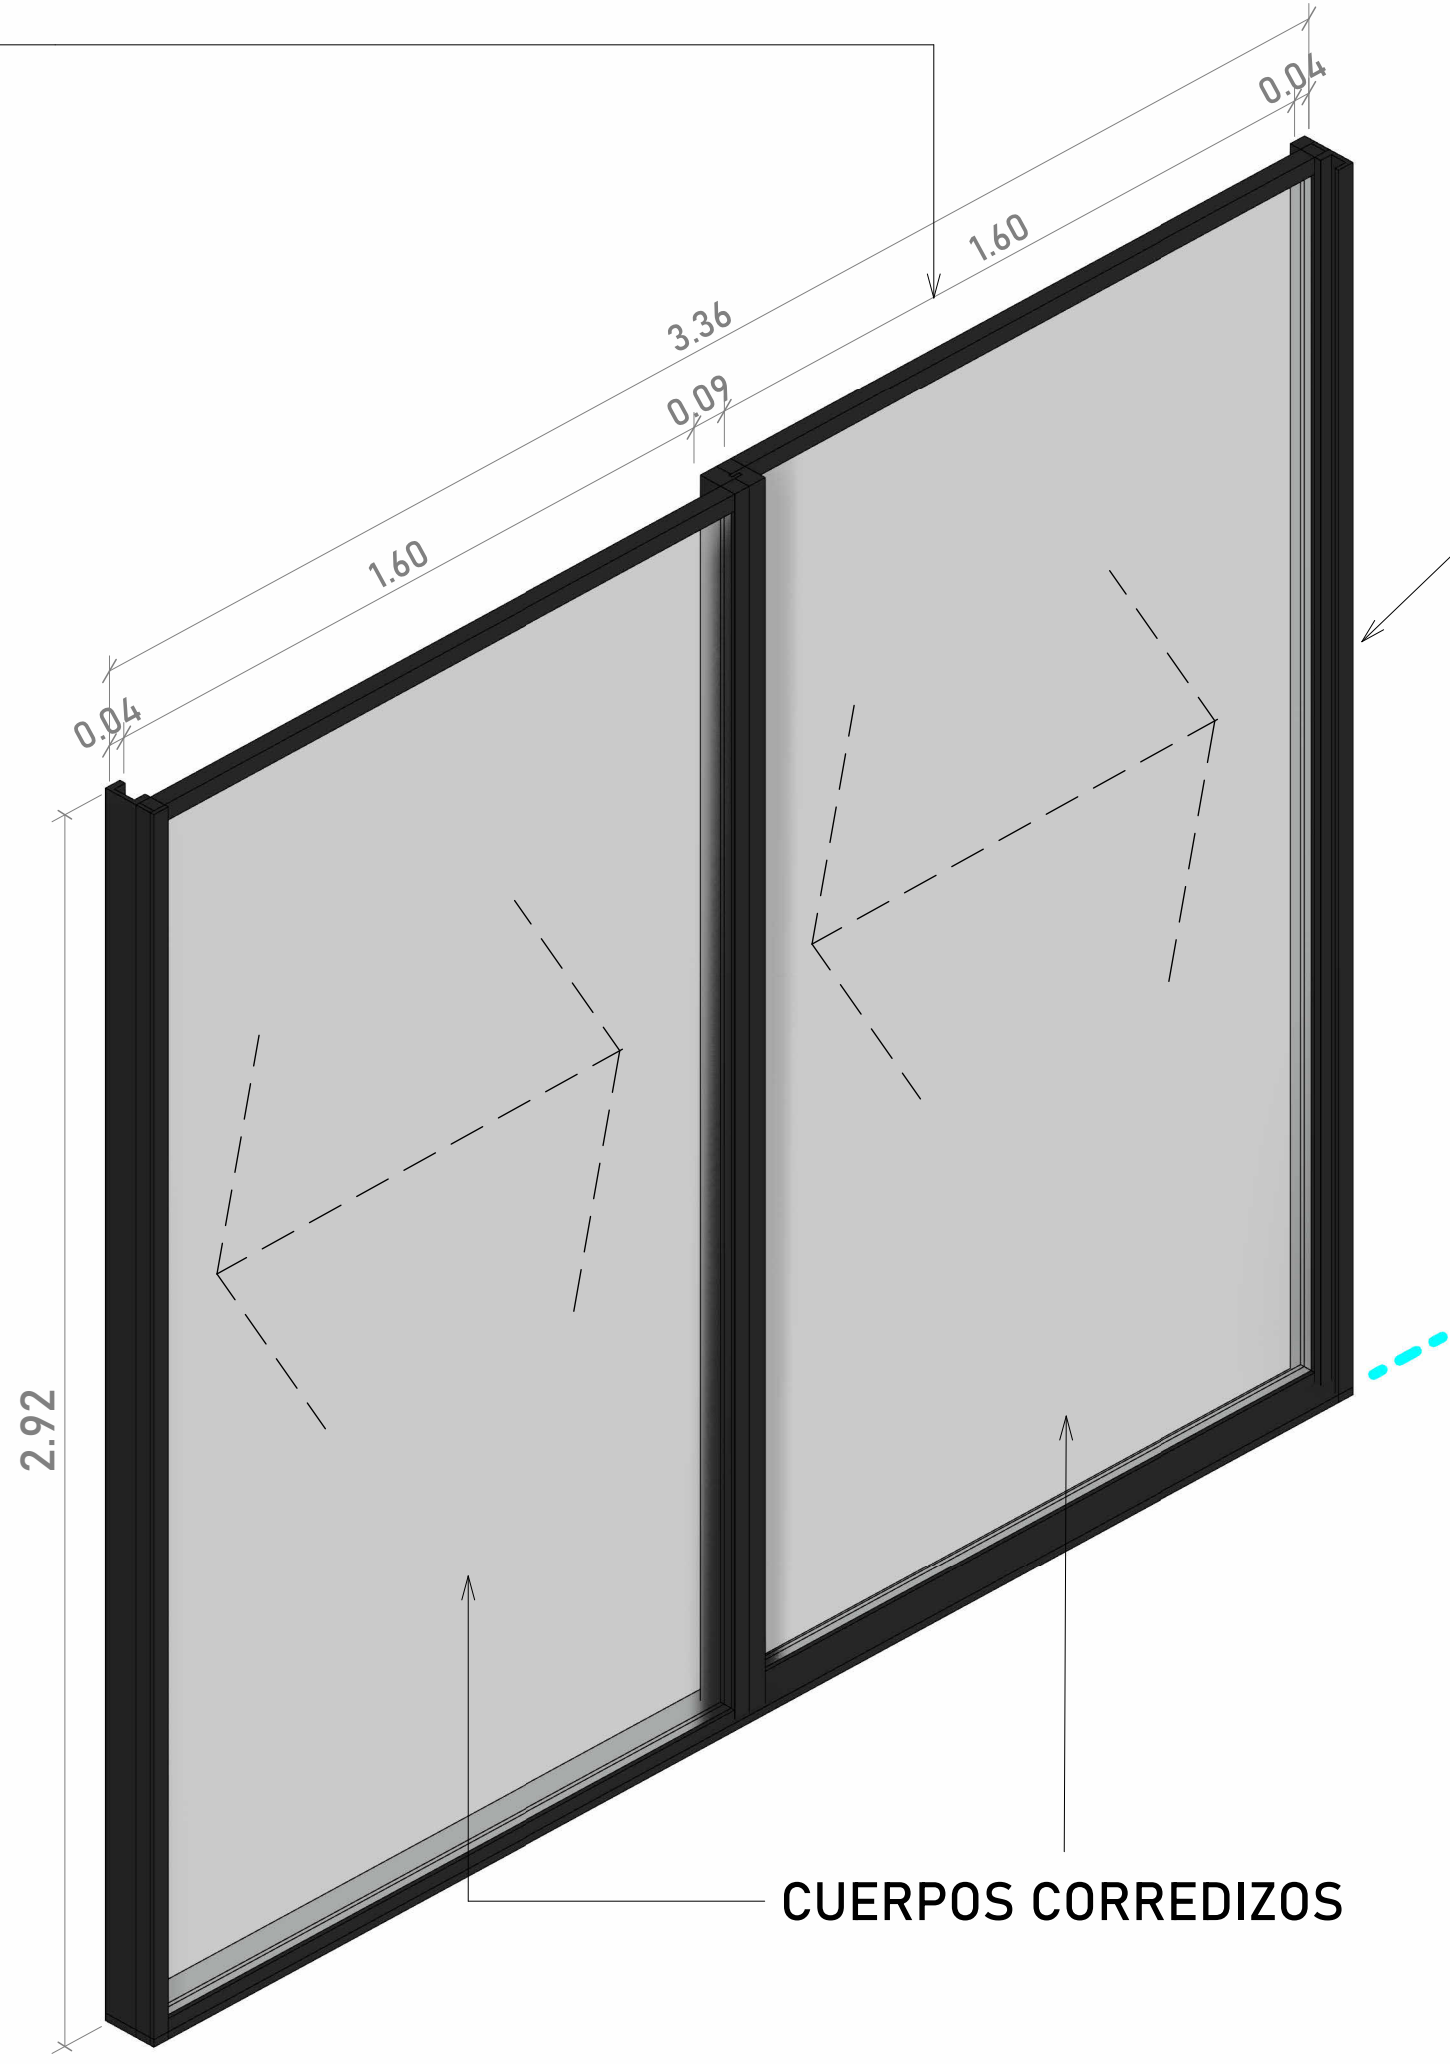

NOTA: PERFILERIA METÁLICA
NEGRA CADA NAVE DE 4x4

1 VENTANA CORREDIZA HABITACIÓN 2
1: 15

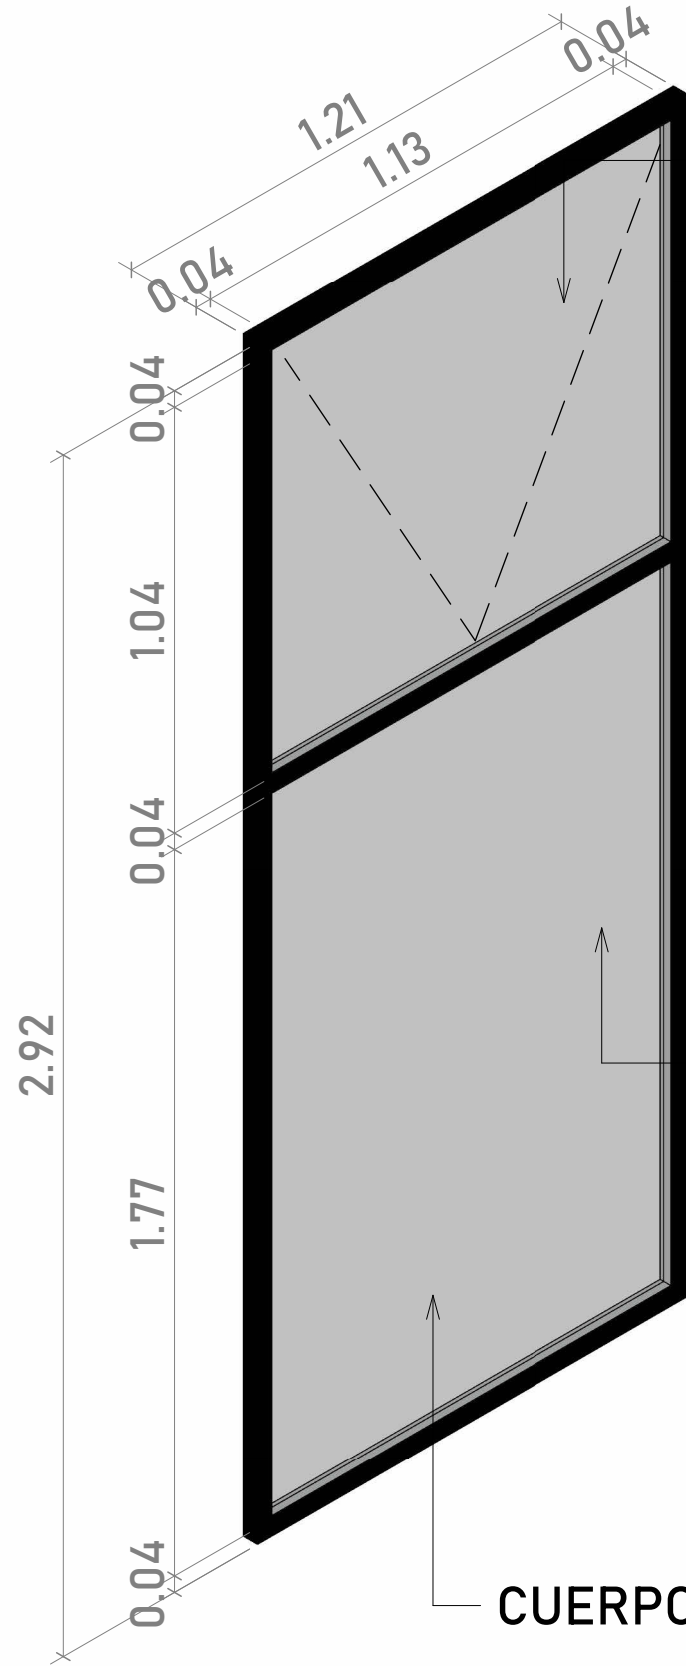


AMBOS CUERPOS PROYECTANTES
HACIA ARRIBA

NOTA: PERFILERIA
METÁLICA NEGRA 4x4

VIDRIO TEMPLADO 6mm

CUERPO FIJO

2 VENTANA DUCHA HABITACIÓN 2
1: 15

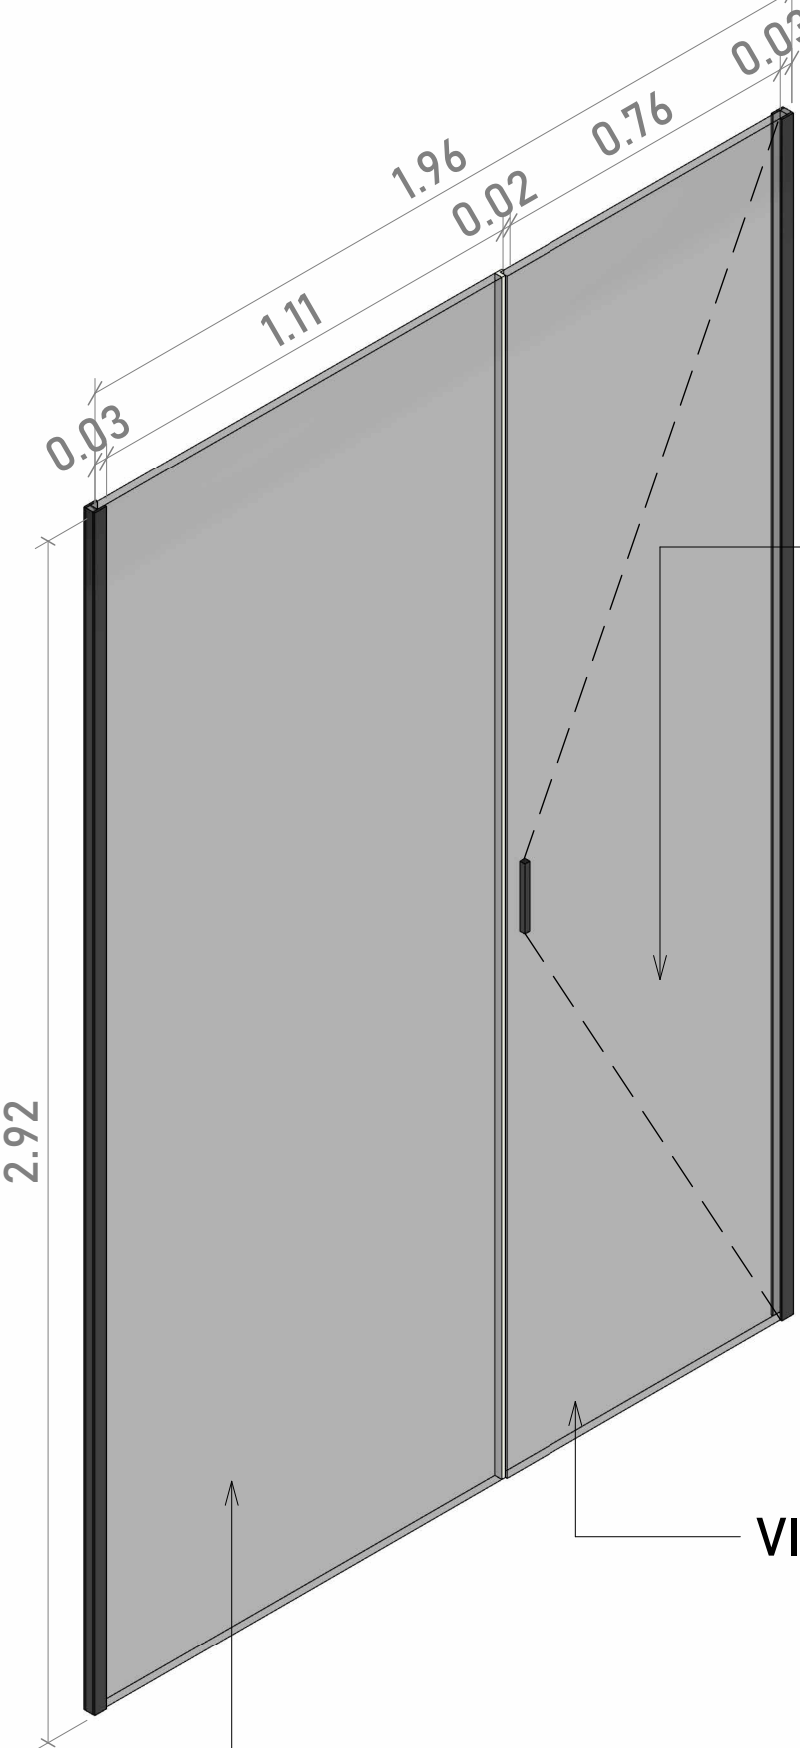


PUERTA BATIENTE


VIDRIO TEMPLADO 6mm

CUERPO FIJO


3 PUERTA CABINA DUCHA HAB 2
1: 15

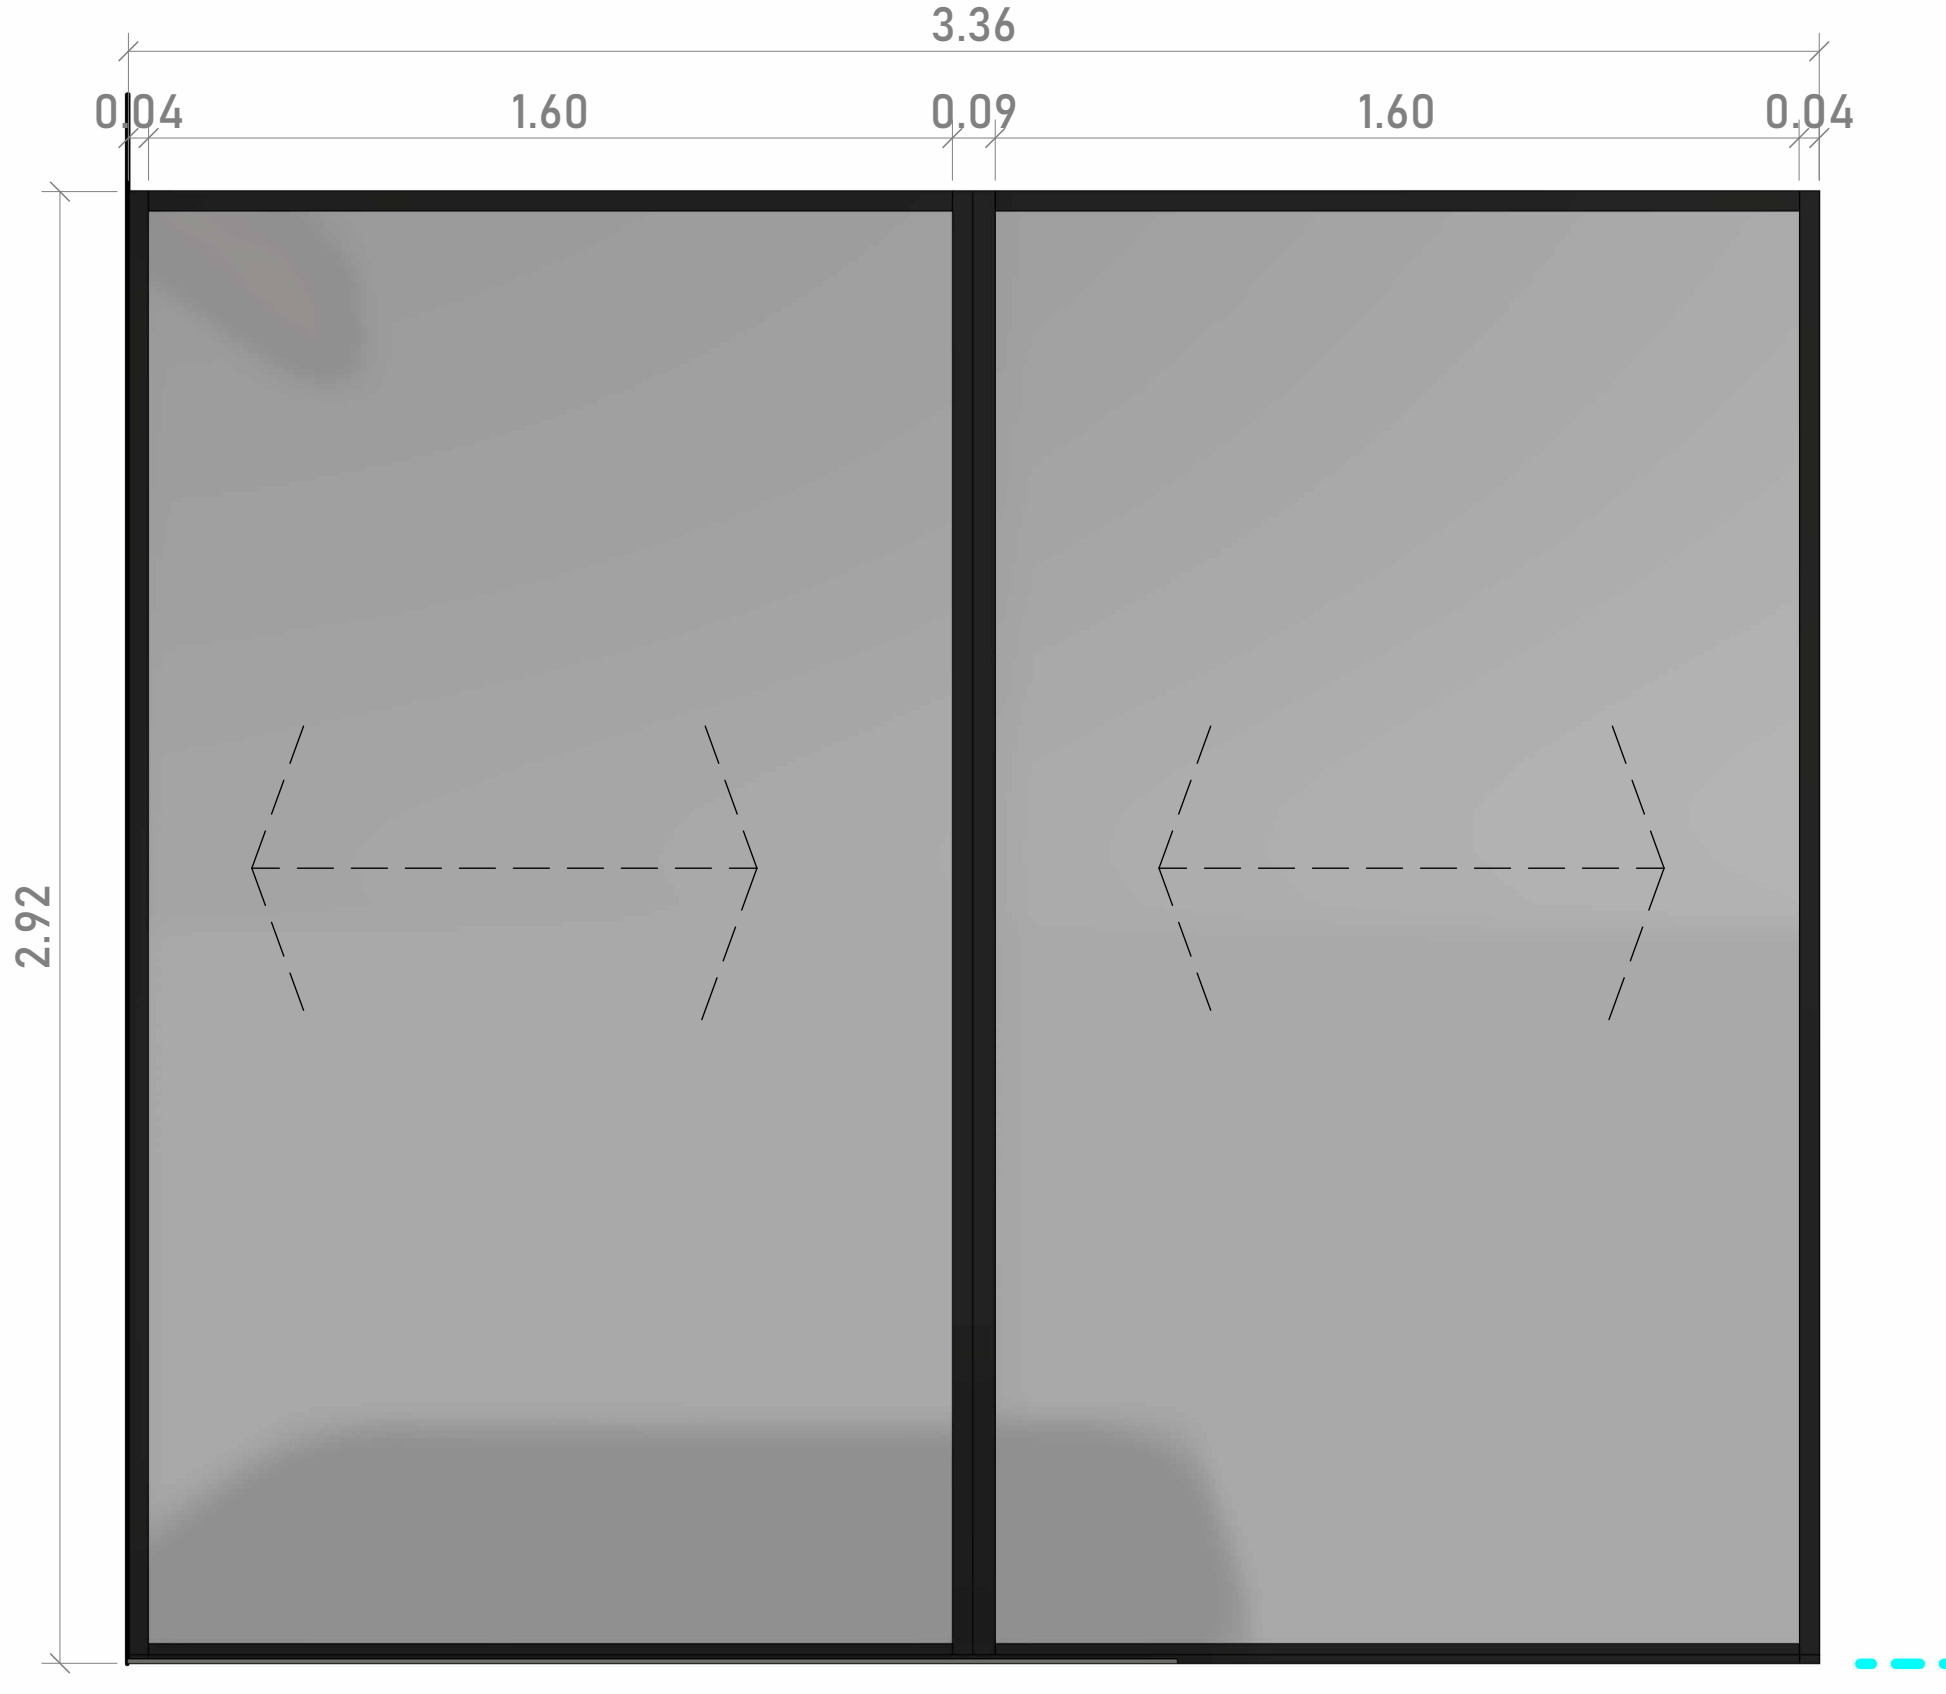

1 VENTANA CORREDIZA HABITACIÓN 2
1: 15

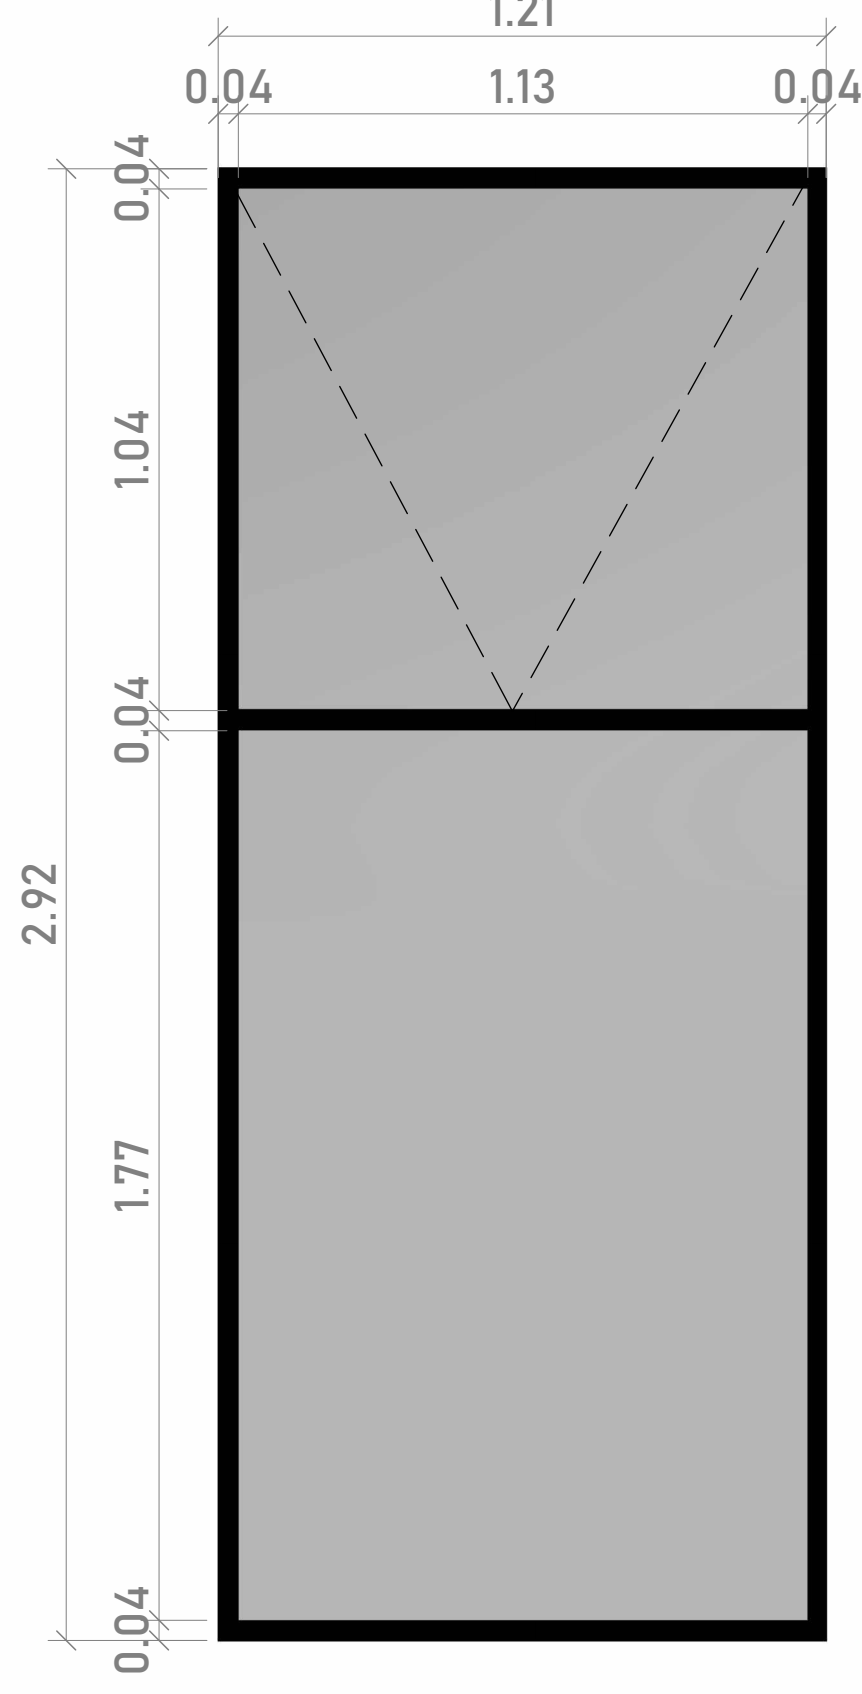

2 VENTANA DUCHA HABITACIÓN 2
1: 15

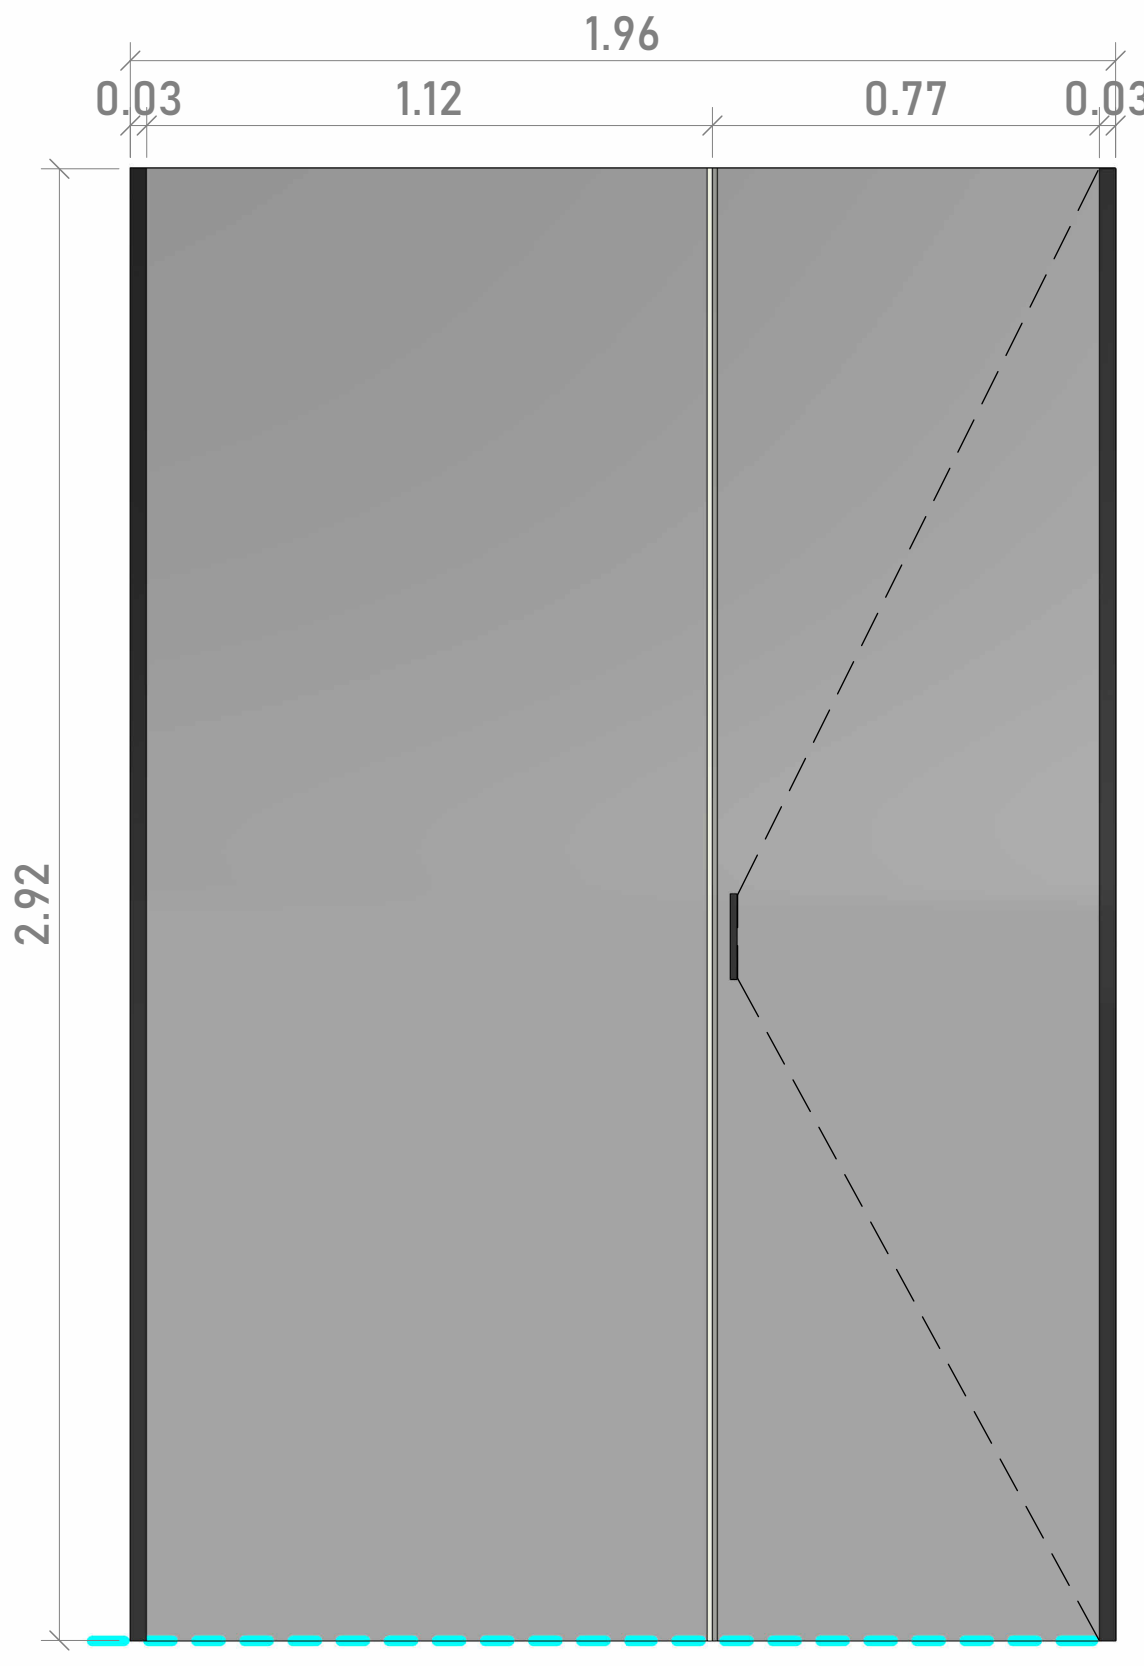

3 PUERTA CABINA DUCHA HAB 2
1: 15



NOTA: TODAS LAS VISTAS EN ISOMETRICO
ESTAN ORIENTADAS DESDE LA PARTE
INTERIOR DE LA HABITACIÓN

Proyecto:
HARAS

Observaciones:

Revisa:
ANA SOFIA ROLDAN

Verifica:
DANIELA ARIZA RAMIREZ

Aprueba:
DANIELA ARIZA RAMIREZ

Cliente:
SANDRA MEJIA VELEZ Y EDWIN ALFREDO
ACOSTA

Diseño:
DANIELA ARIZA RAMIREZ

Cálculos estructurales:
12/05/25

Archivo de Referencia:
20251212_DISEÑO HARAS

Contiene:
CARP METÁLICA VENTANAS
HAB 2

Escala:

Fecha:

2025/22/12

Dibujo:

JORDY PINEDA BELLIDO

Plancha N°:

A 4

De:

9

Firmas:

Proyecto:
HARAS

Matrícula inmobiliaria:
No 020-238645

Parcelación:
Parcelación Haras
Campestre – P.H.

Número de lote:
Lote No. 4 Llanogrande

Observaciones:
Según NSR-10

Revisa:
ANA SOFIA ROLDAN

Verifica:
DANIELA ARIZA RAMIREZ

Aprueba:
DANIELA ARIZA RAMIREZ

Cliente:
SANDRA MEJIA VELEZ Y
EDWIN ALFREDO ACOSTA

Diseño:
DANIELA ARIZA RAMIREZ

Cálculos estructurales:
12/05/25

Archivo de Referencia:
20251212_DISEÑO HARAS

Contiene:
CARP METÁLICA HAB PPAL

Escala:
1:10


Fecha:
2025/22/12

Dibujo:
JORDY PINEDA BELLIDO


Plancha N°:
A 5

De:
9

Firmas:

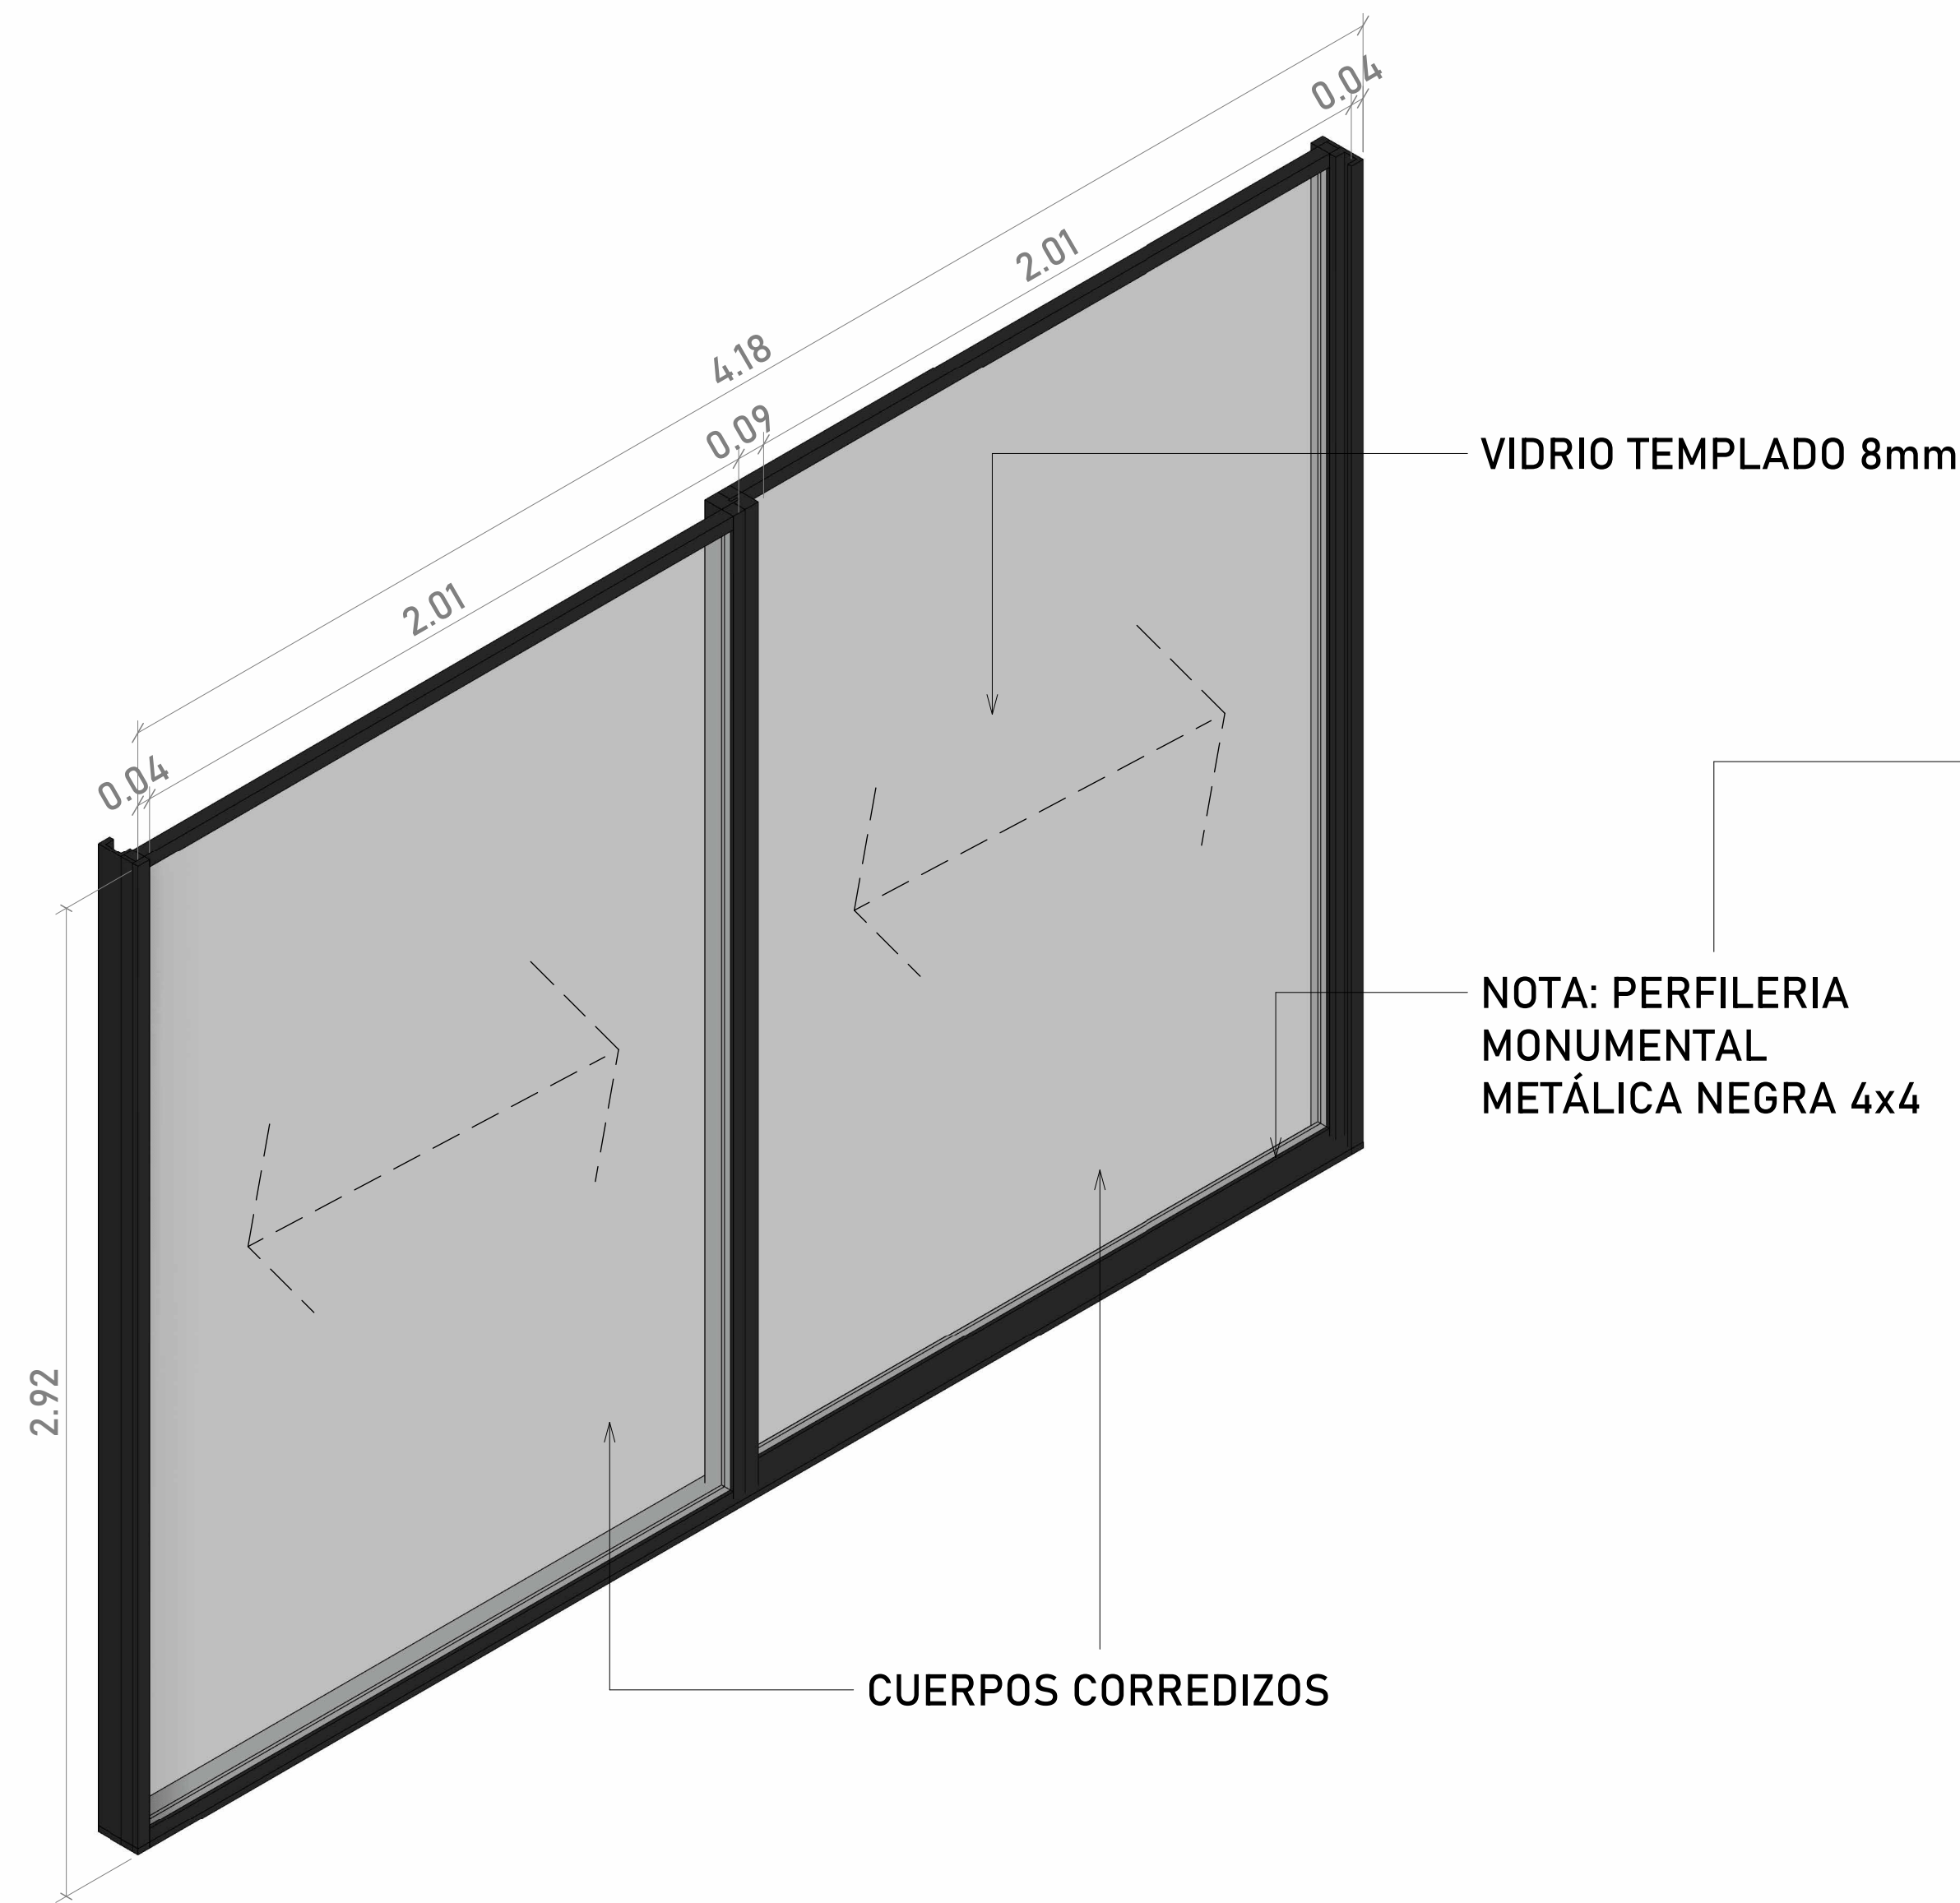


1 VENTANA CORREDIZA 1 HABITACIÓN PPAL
1: 25

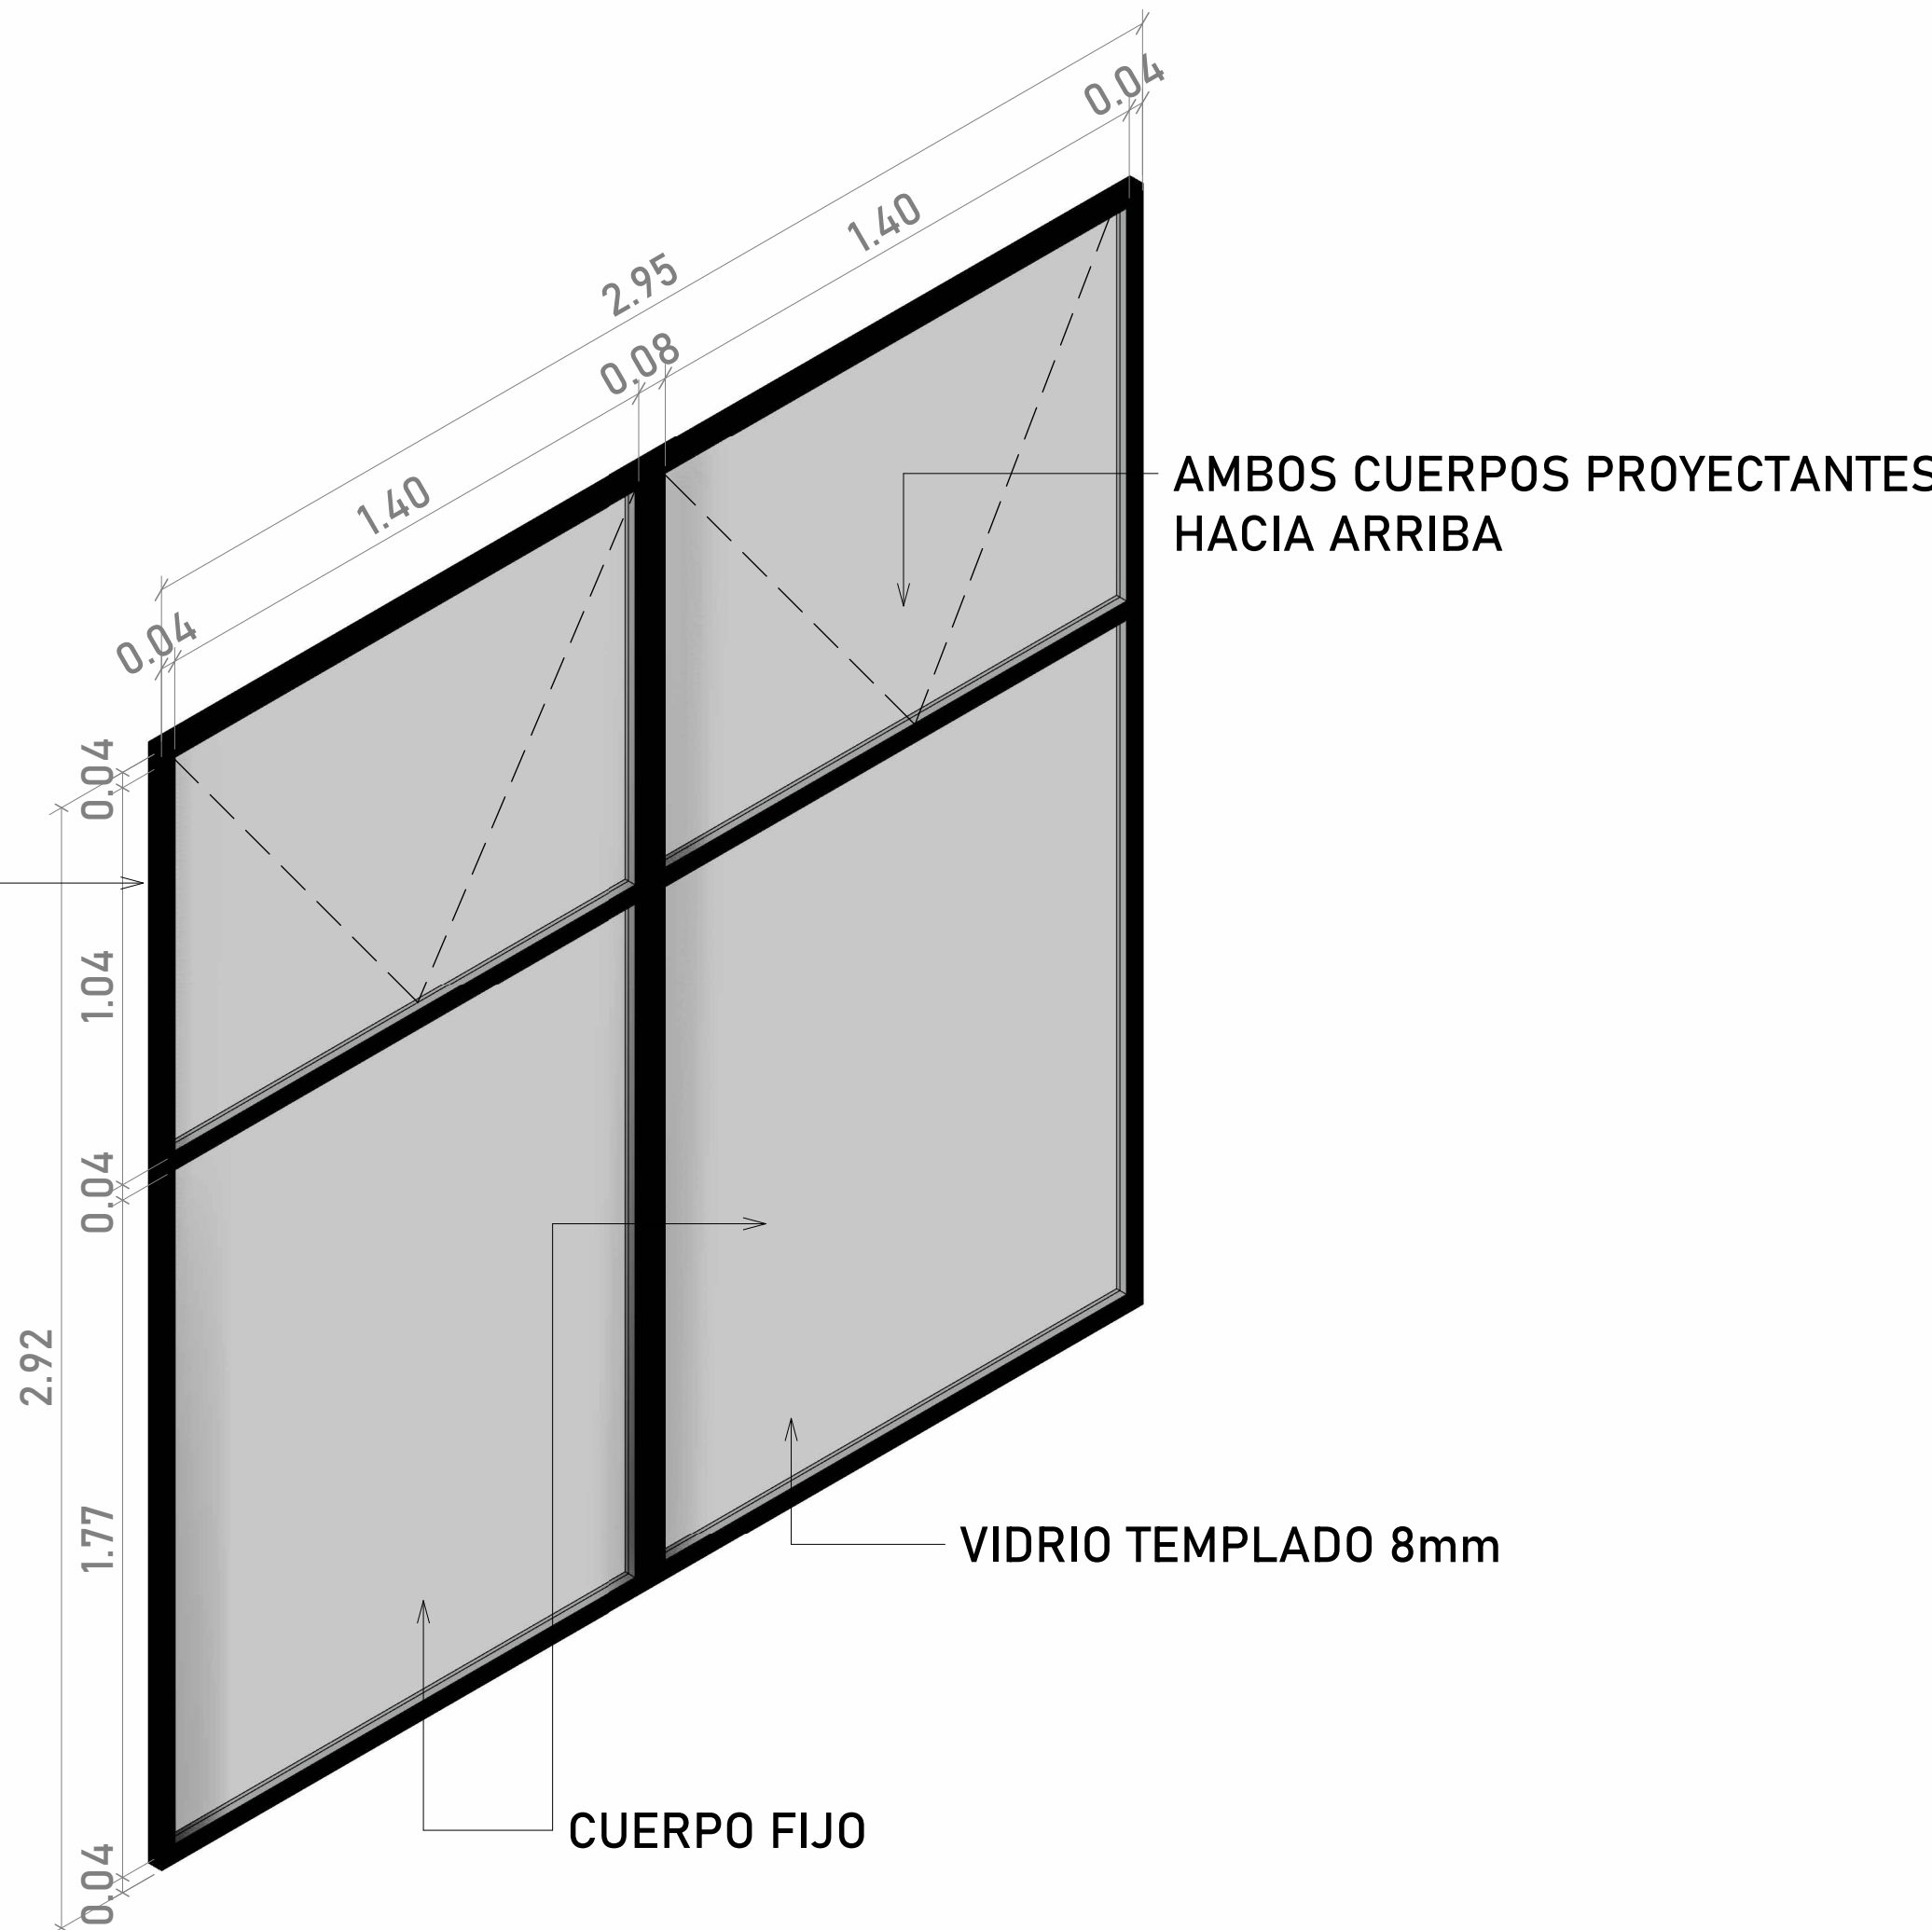


2 VENTANA DUCHA HABITACIÓN PPAL
1: 25




3 VIDRIERA CORREDIZA 2 HABITACIÓN PPAL
1: 25

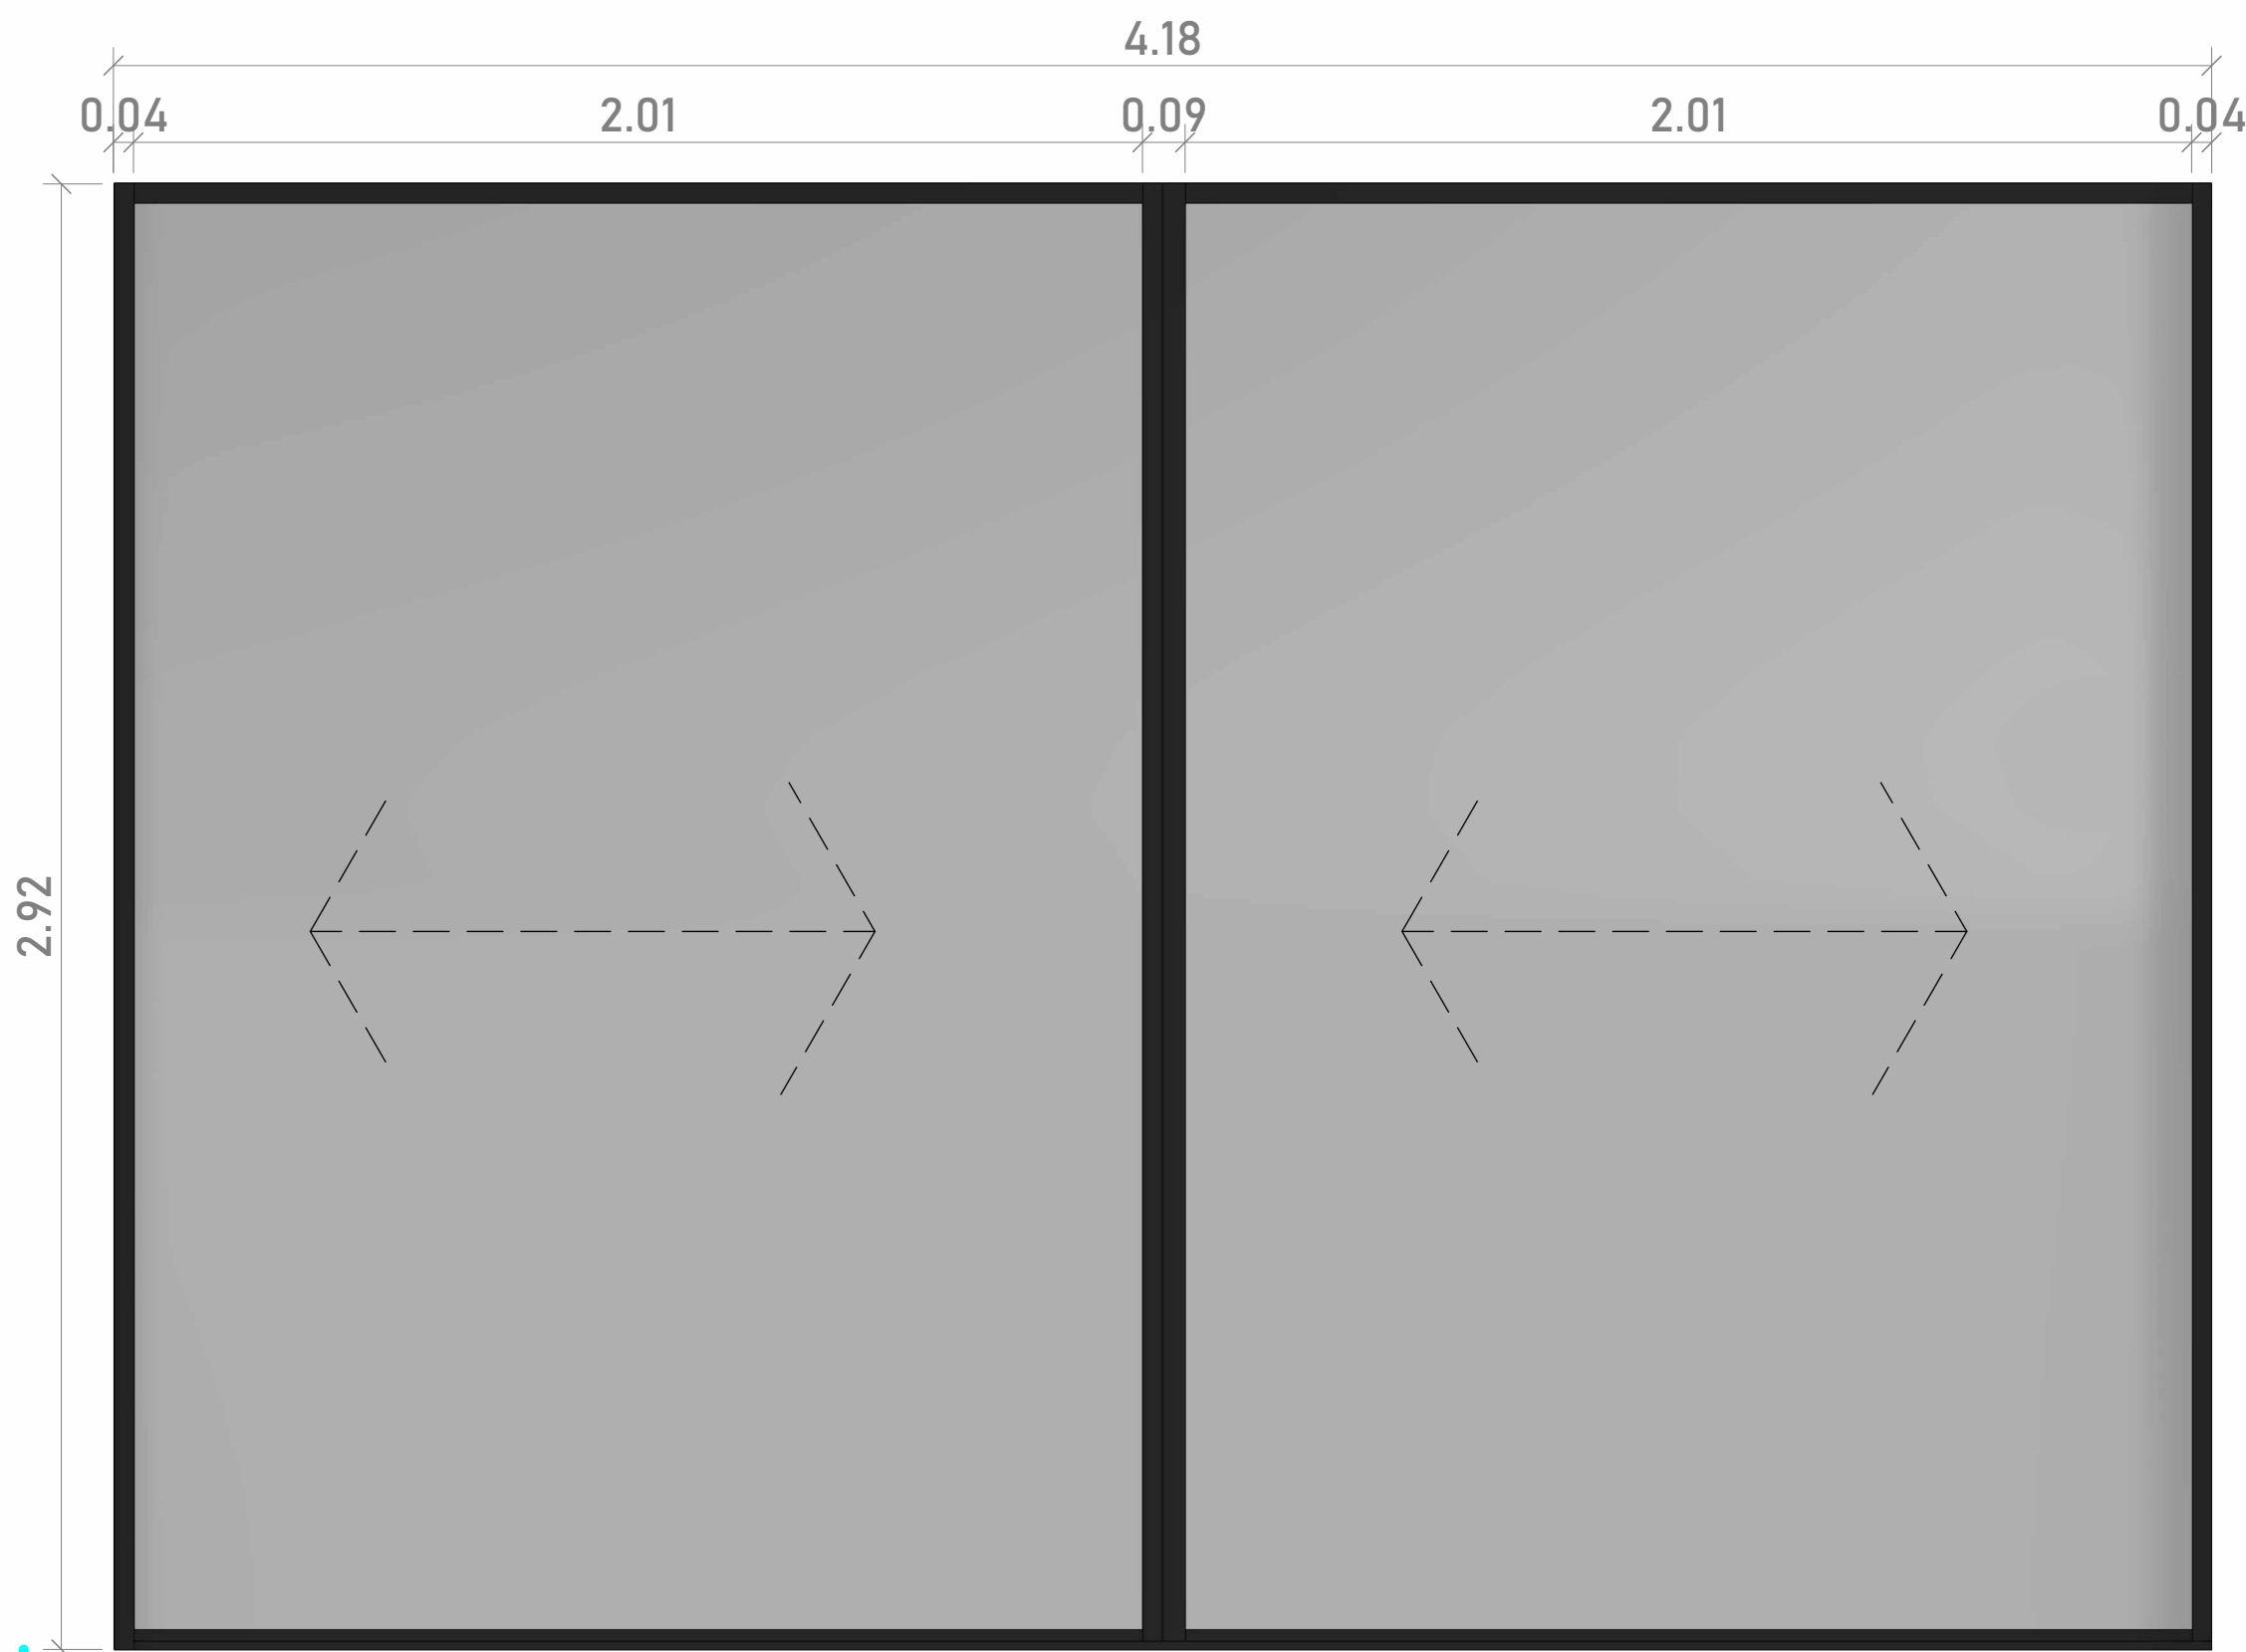


1 VENTANA CORREDIZA 1 HABITACIÓN PPAL
1: 25

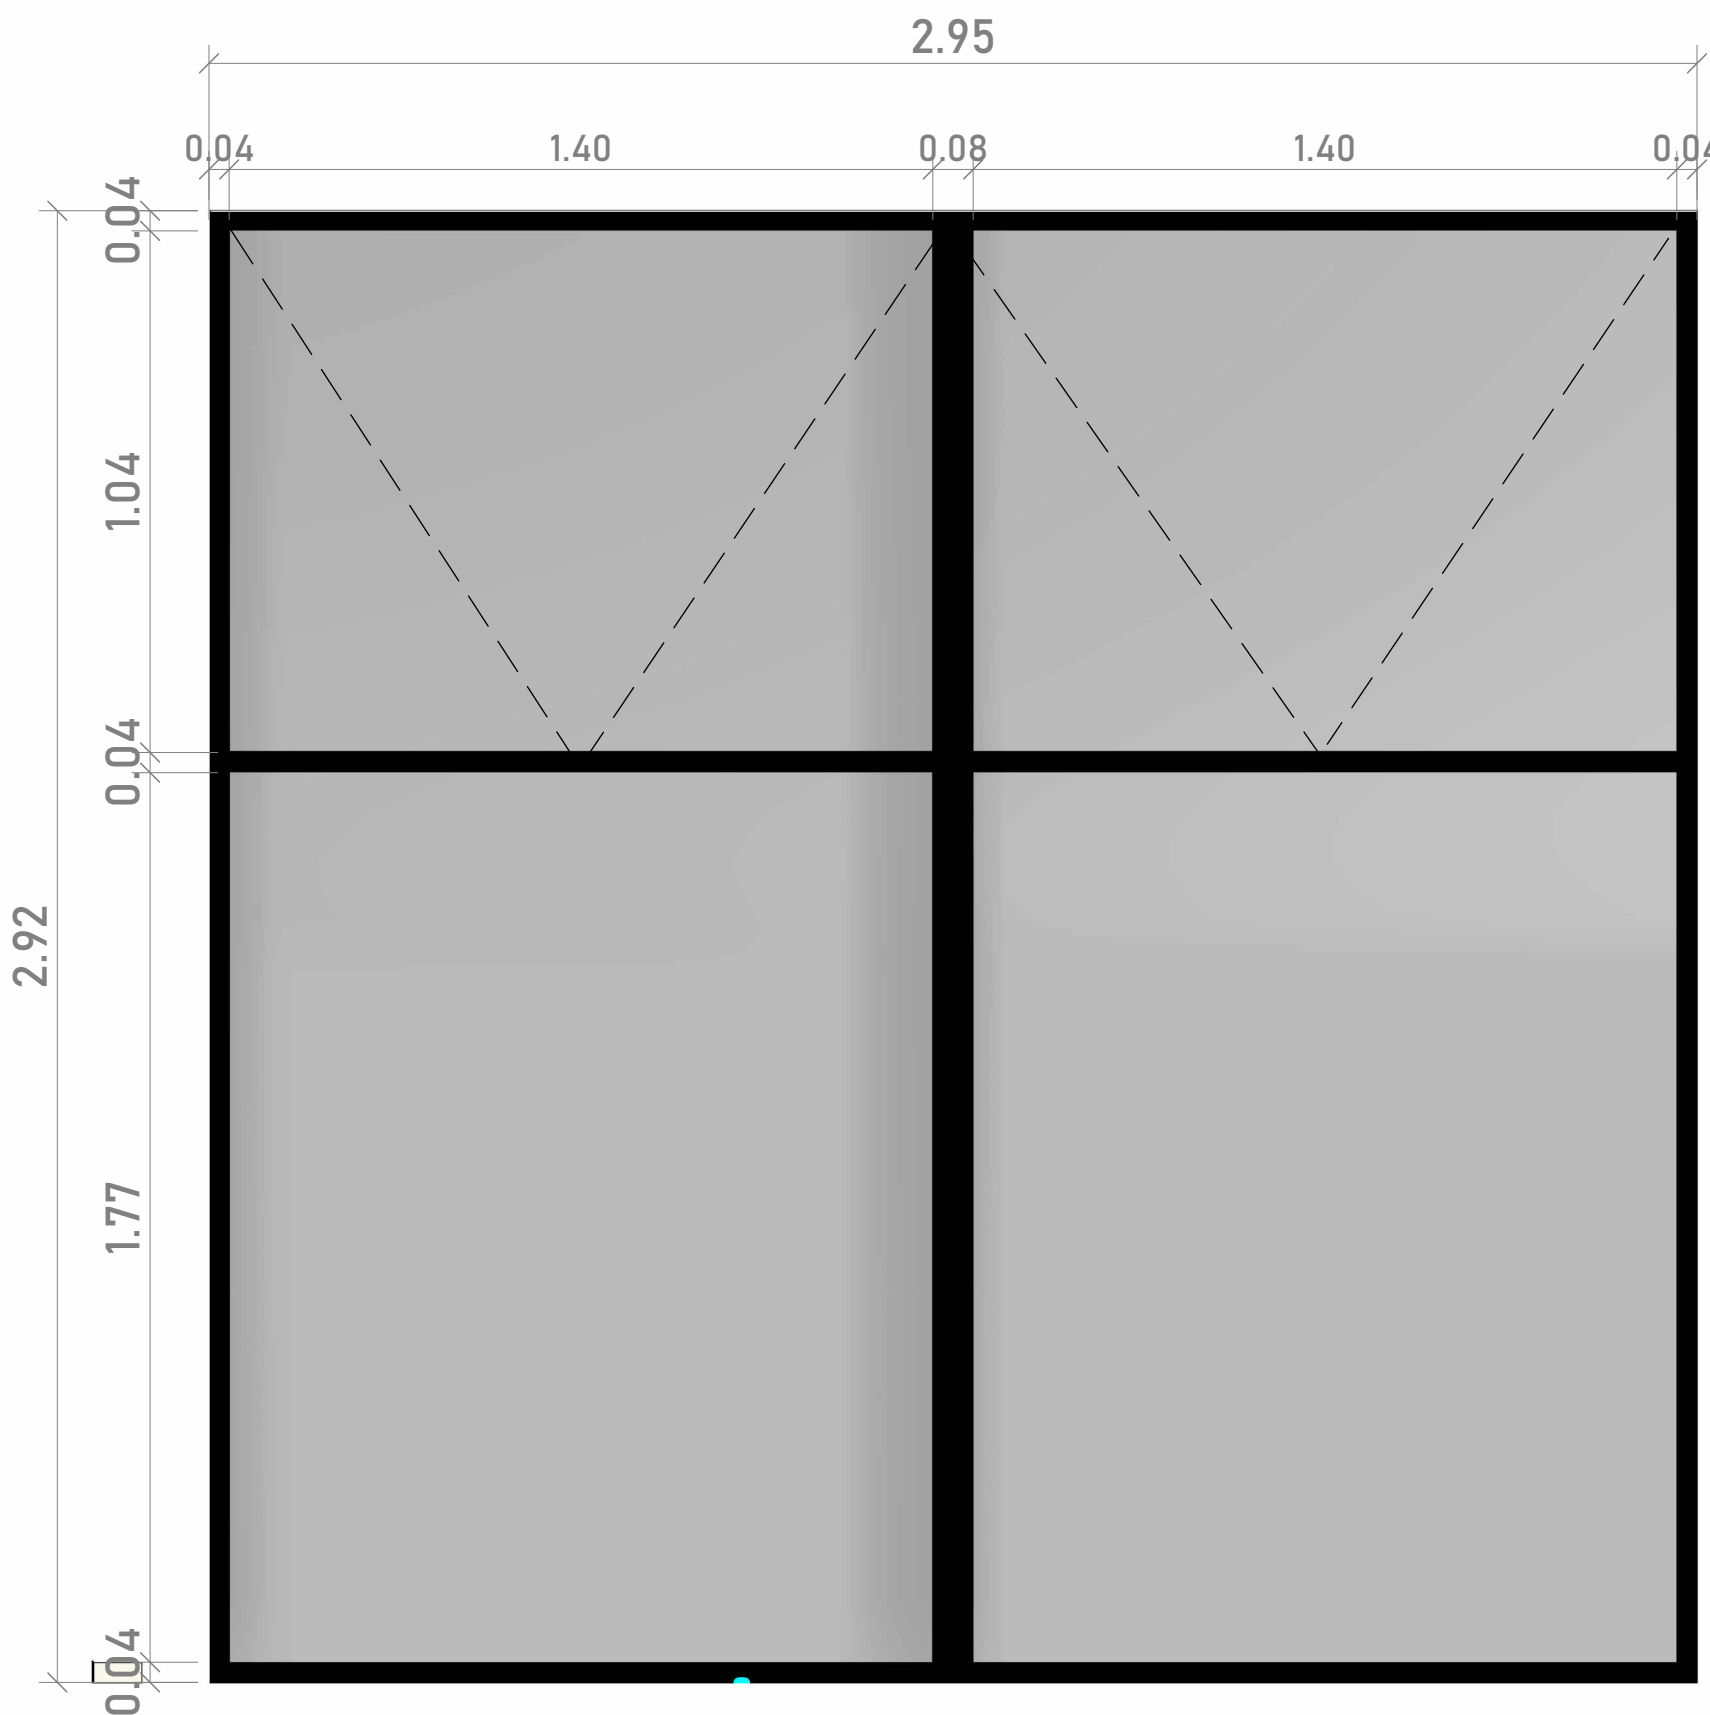


2 VENTANA DUCHA HABITACIÓN PPAL
1: 25

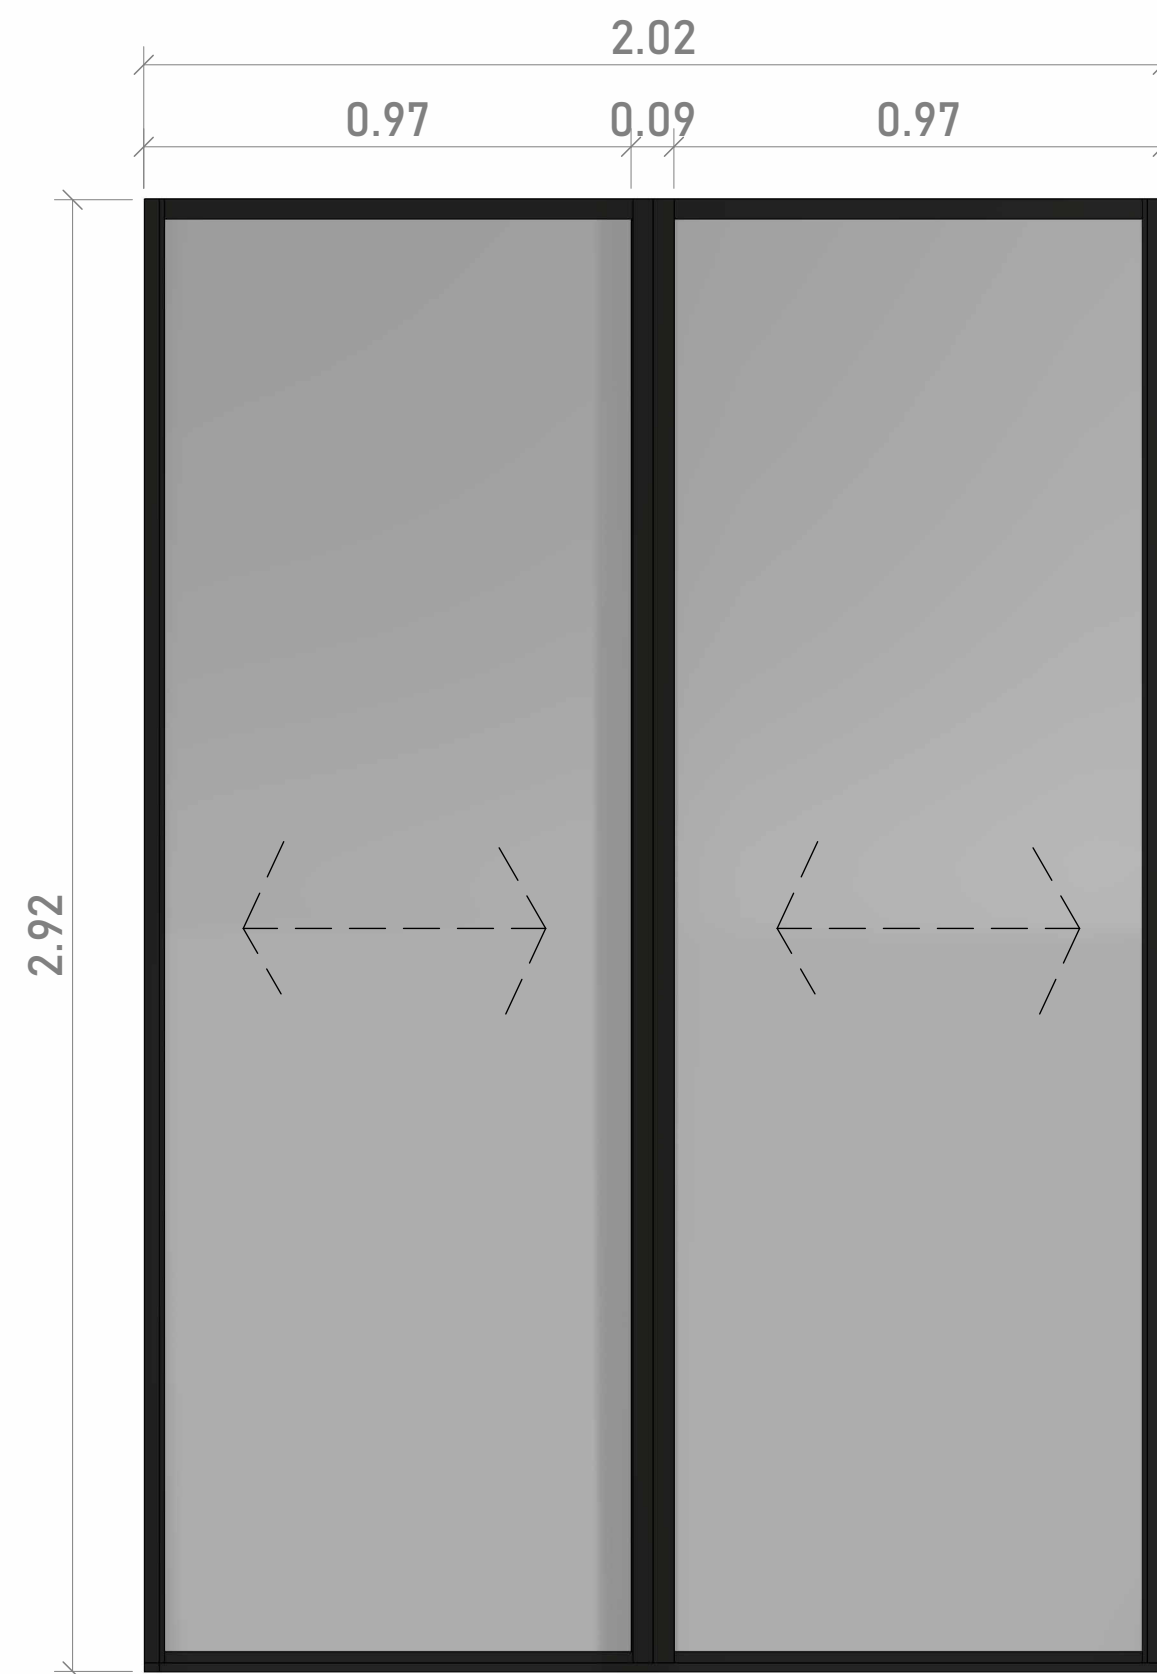


3 VIDRIERA CORREDIZA 2 HABITACIÓN PPAL
1: 25

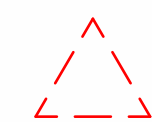


NOTA: TODAS LAS VISTAS EN ISOMETRICO
ESTAN ORIENTADAS DESDE LA PARTE
INTERIOR DE LA HABITACIÓN

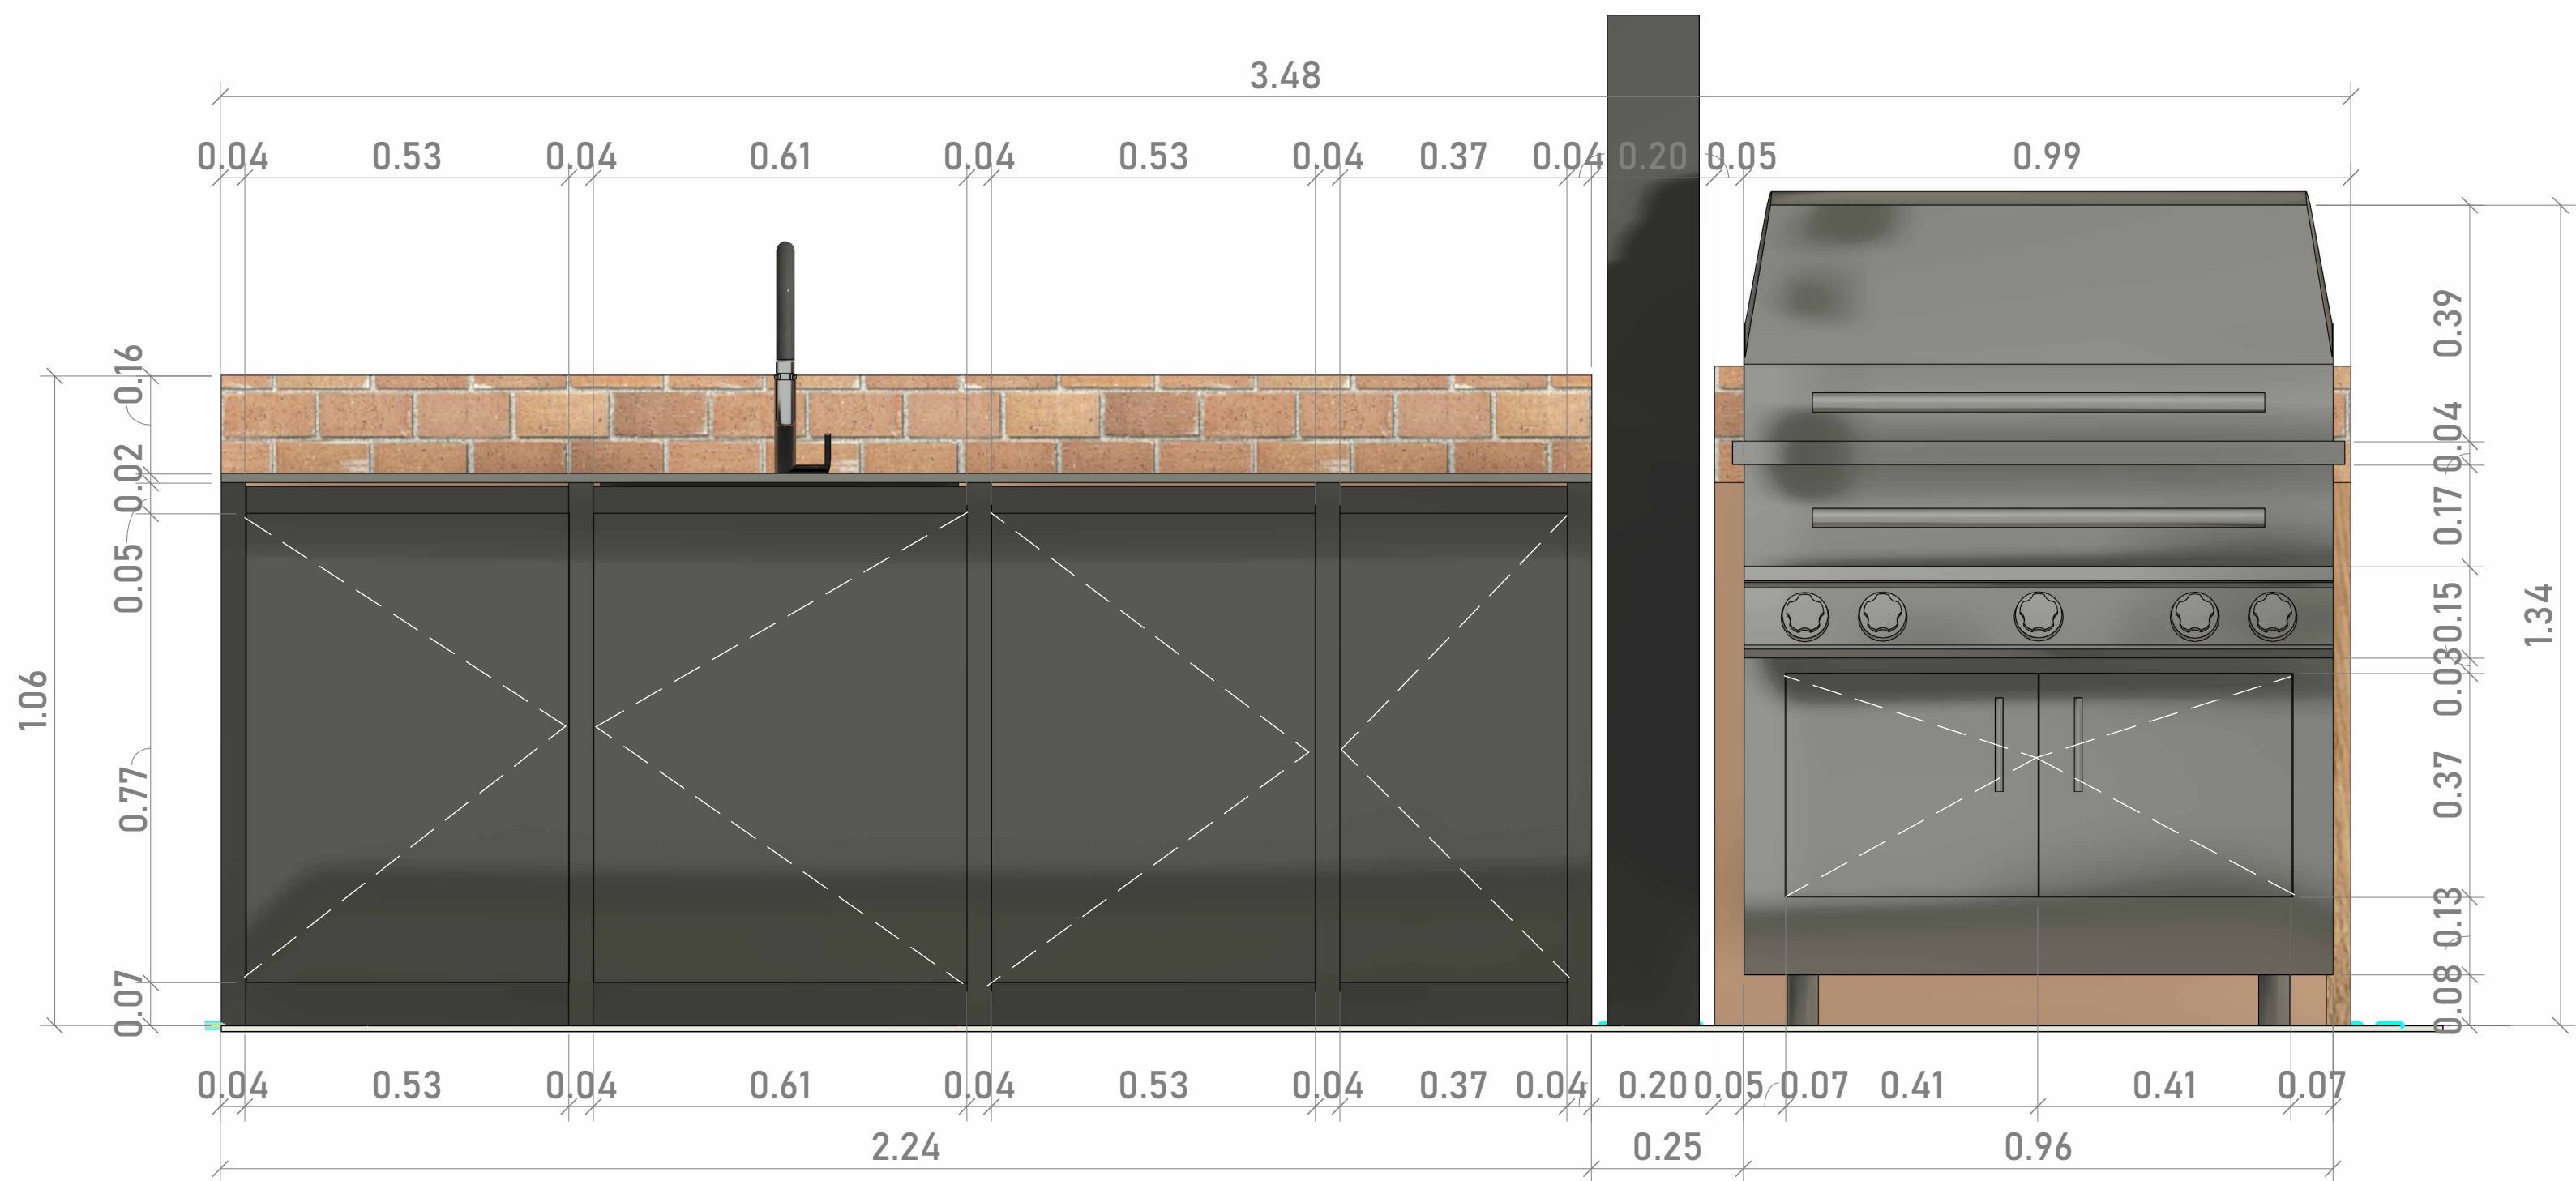

1 ALZADO MUEBLE BBQ EN METAL
1: 10

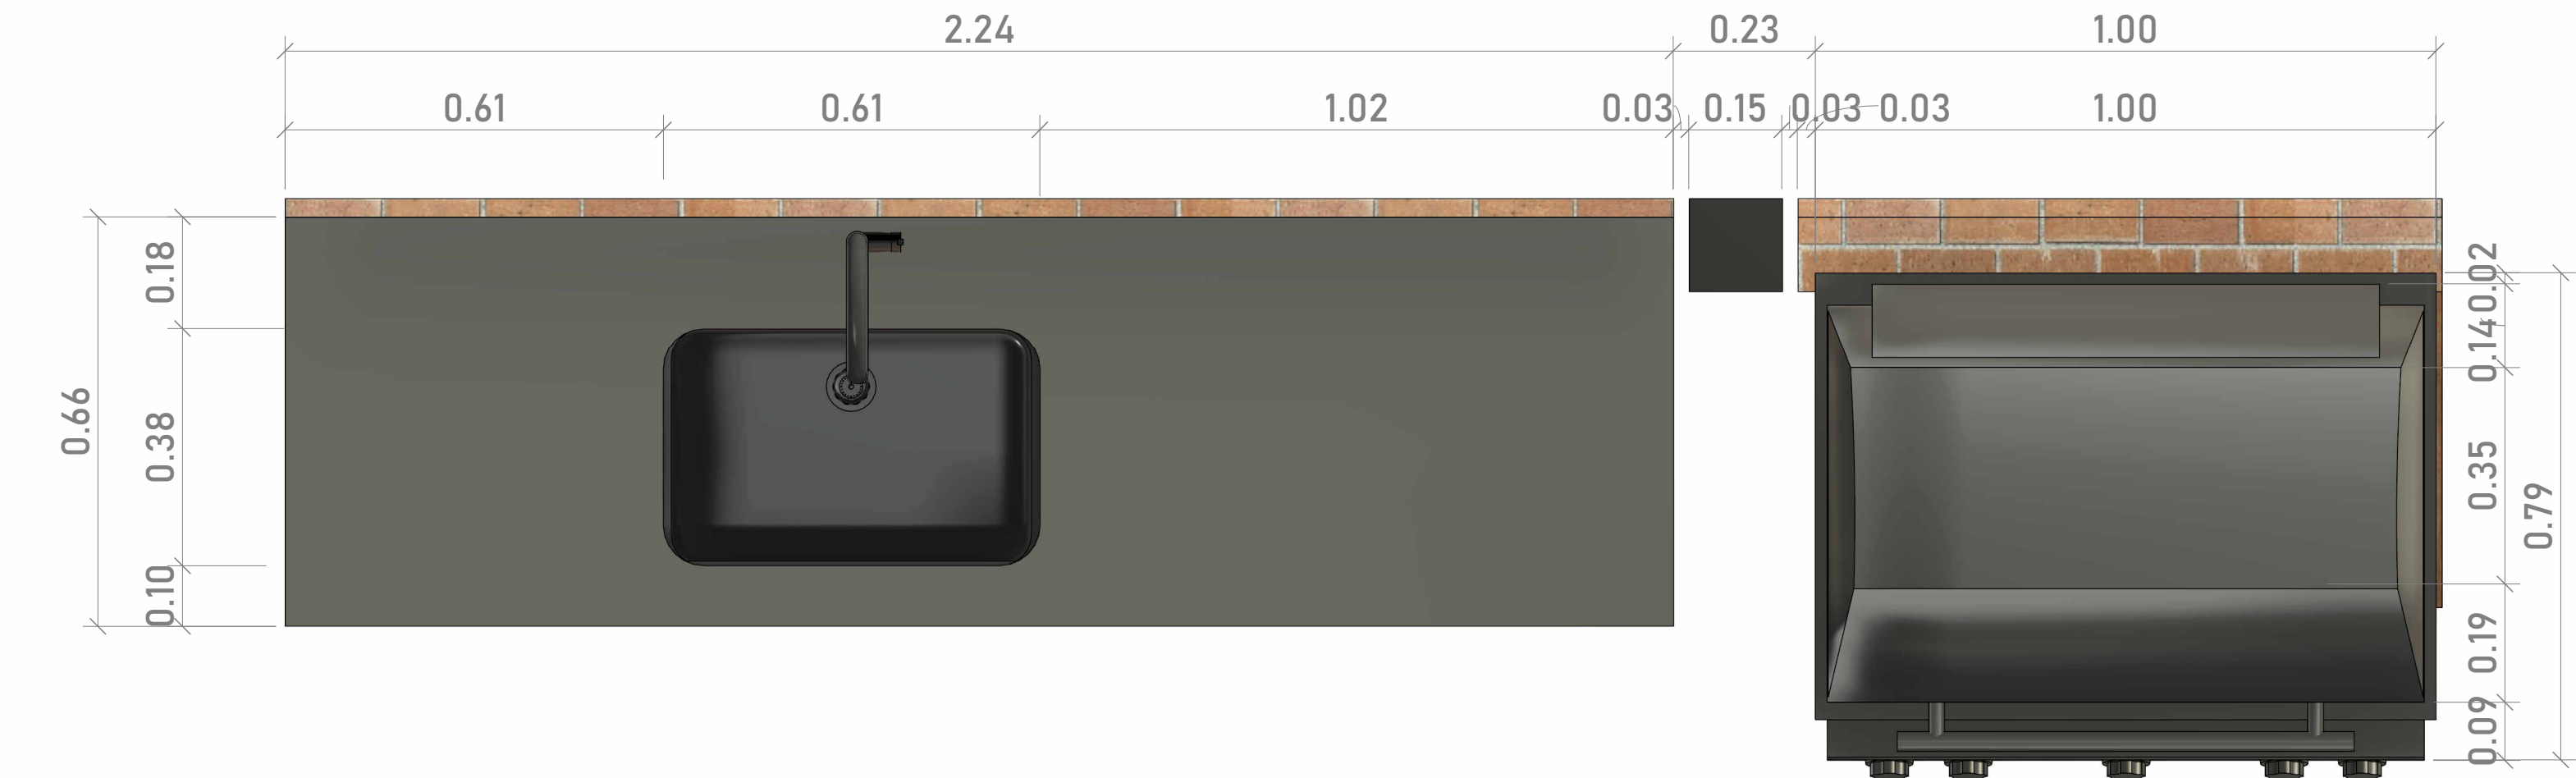


2 PLANTA MUEBLE BBQ EN METAL
1: 10

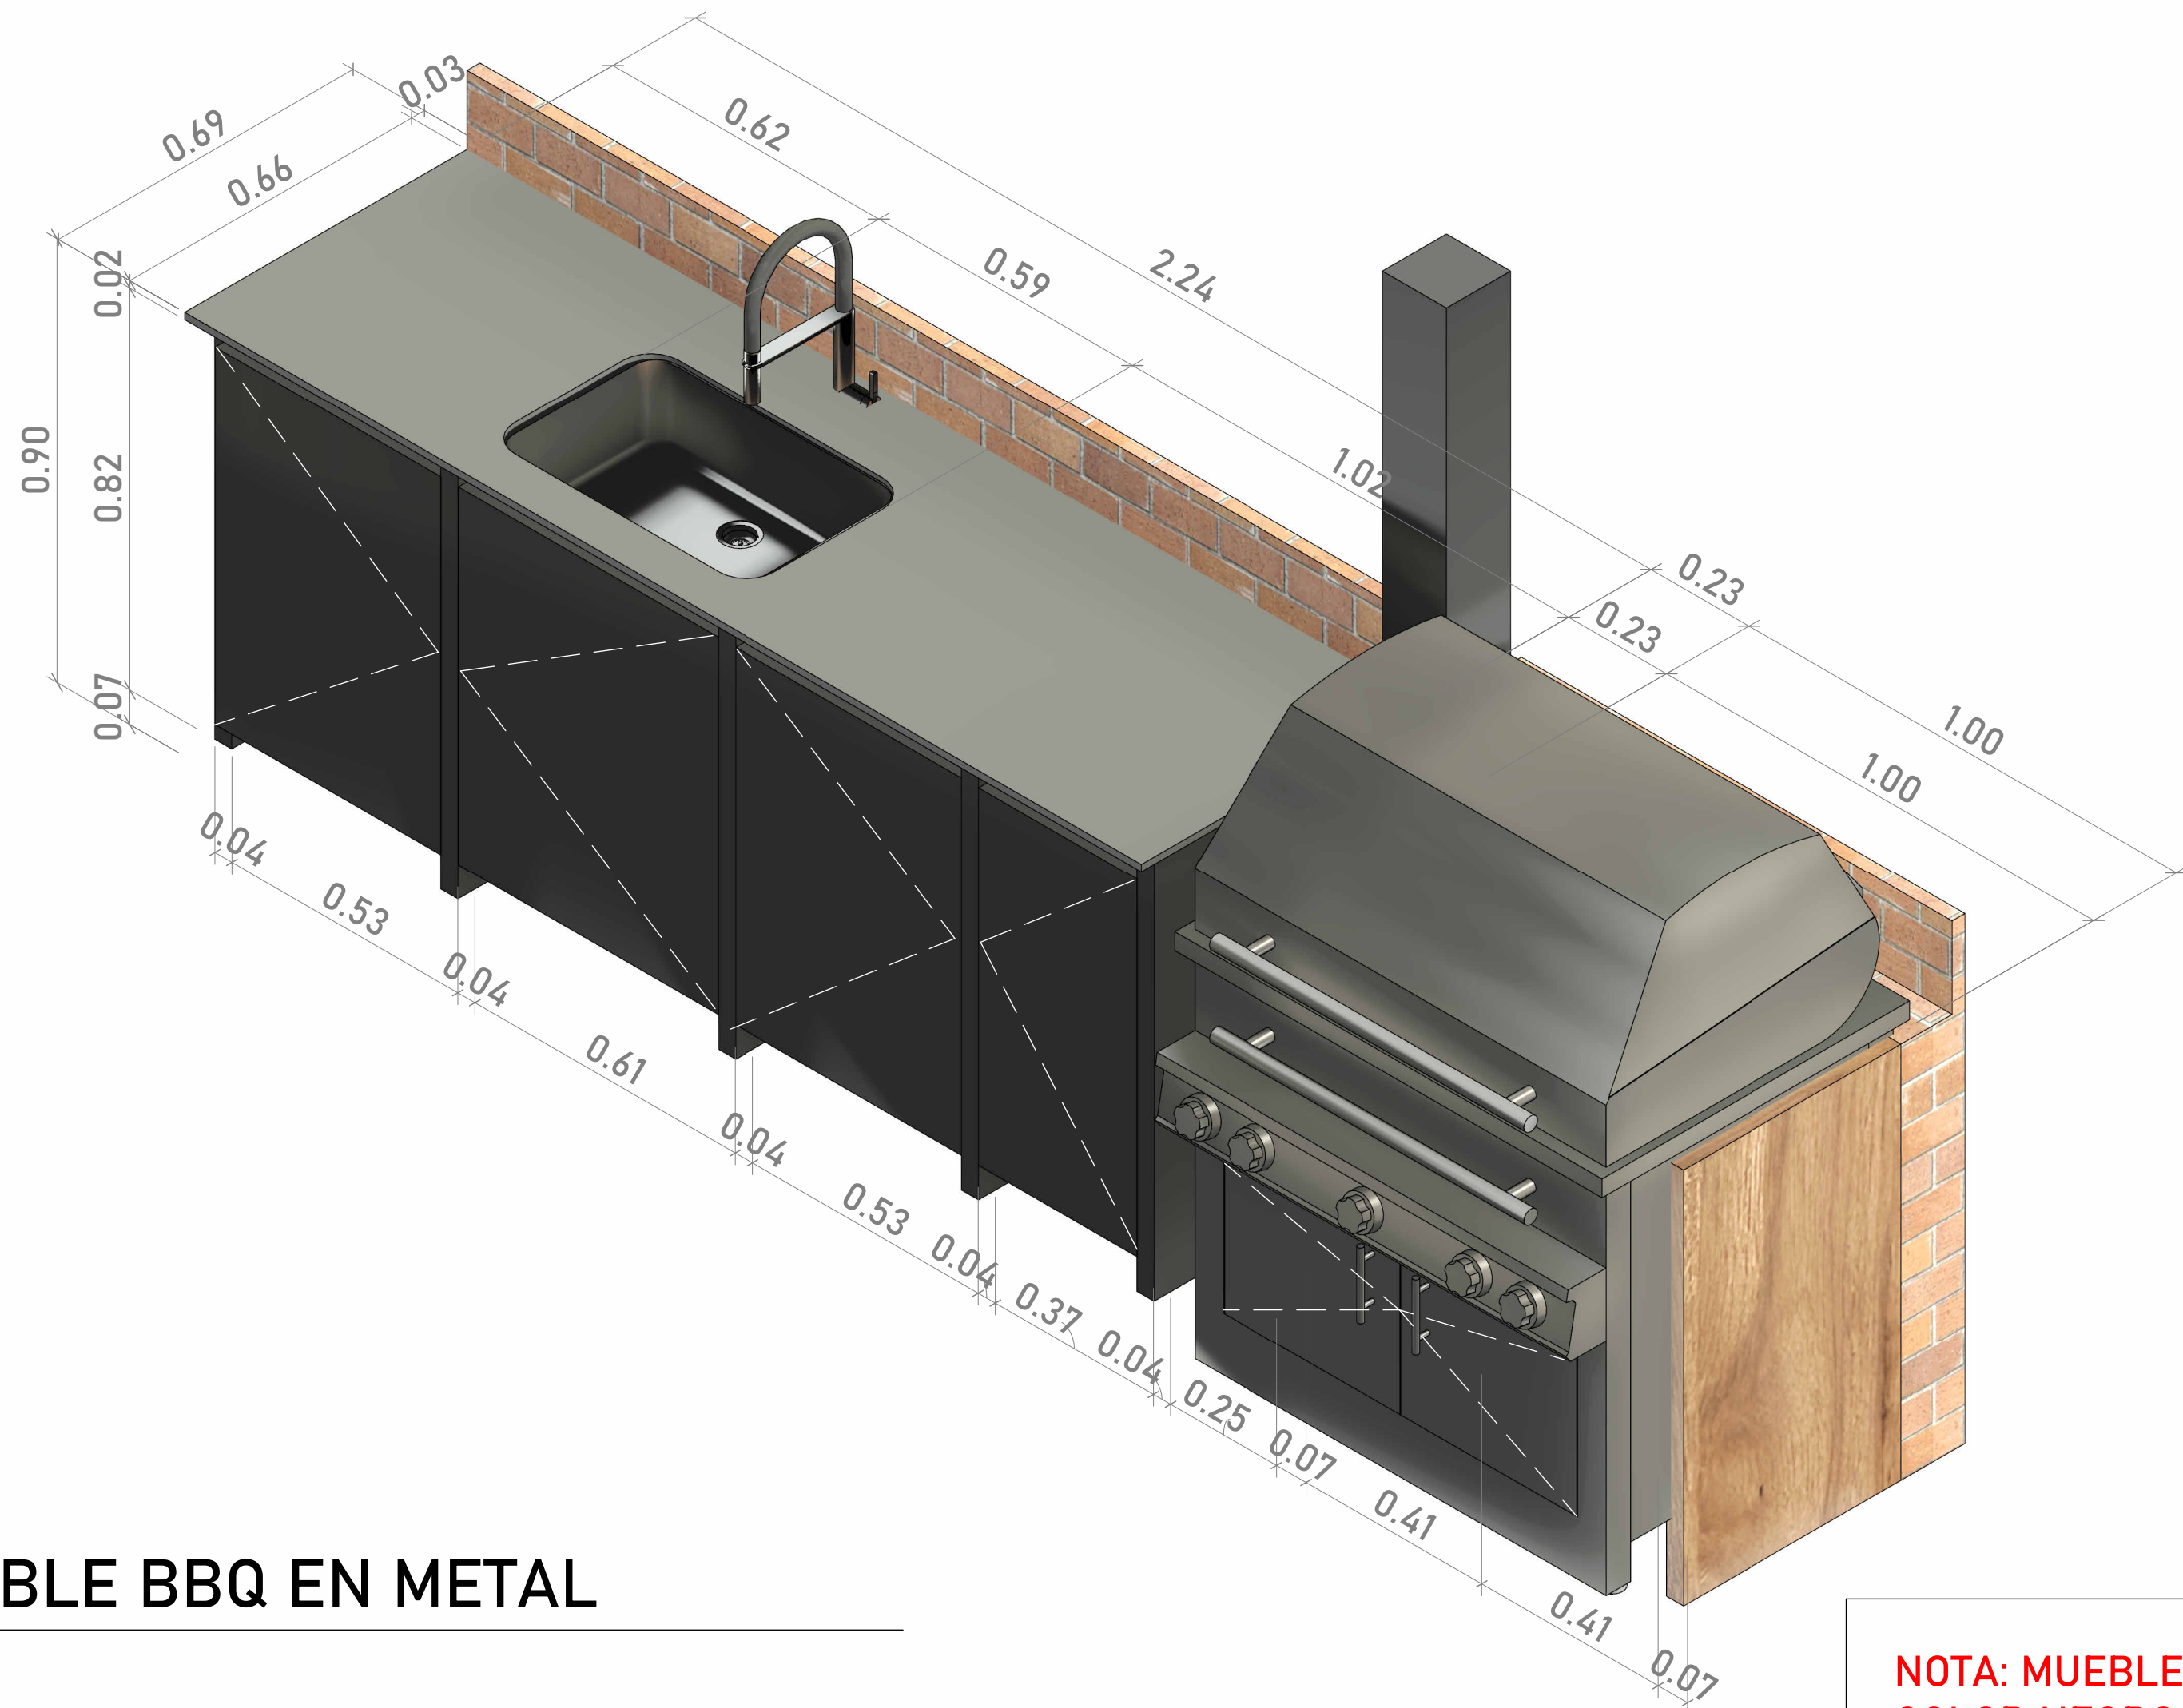

3 VISTA MUEBLE BBQ EN METAL
1: 10


NOTA: MUEBLE BBQ EN METAL
COLOR NEGRO

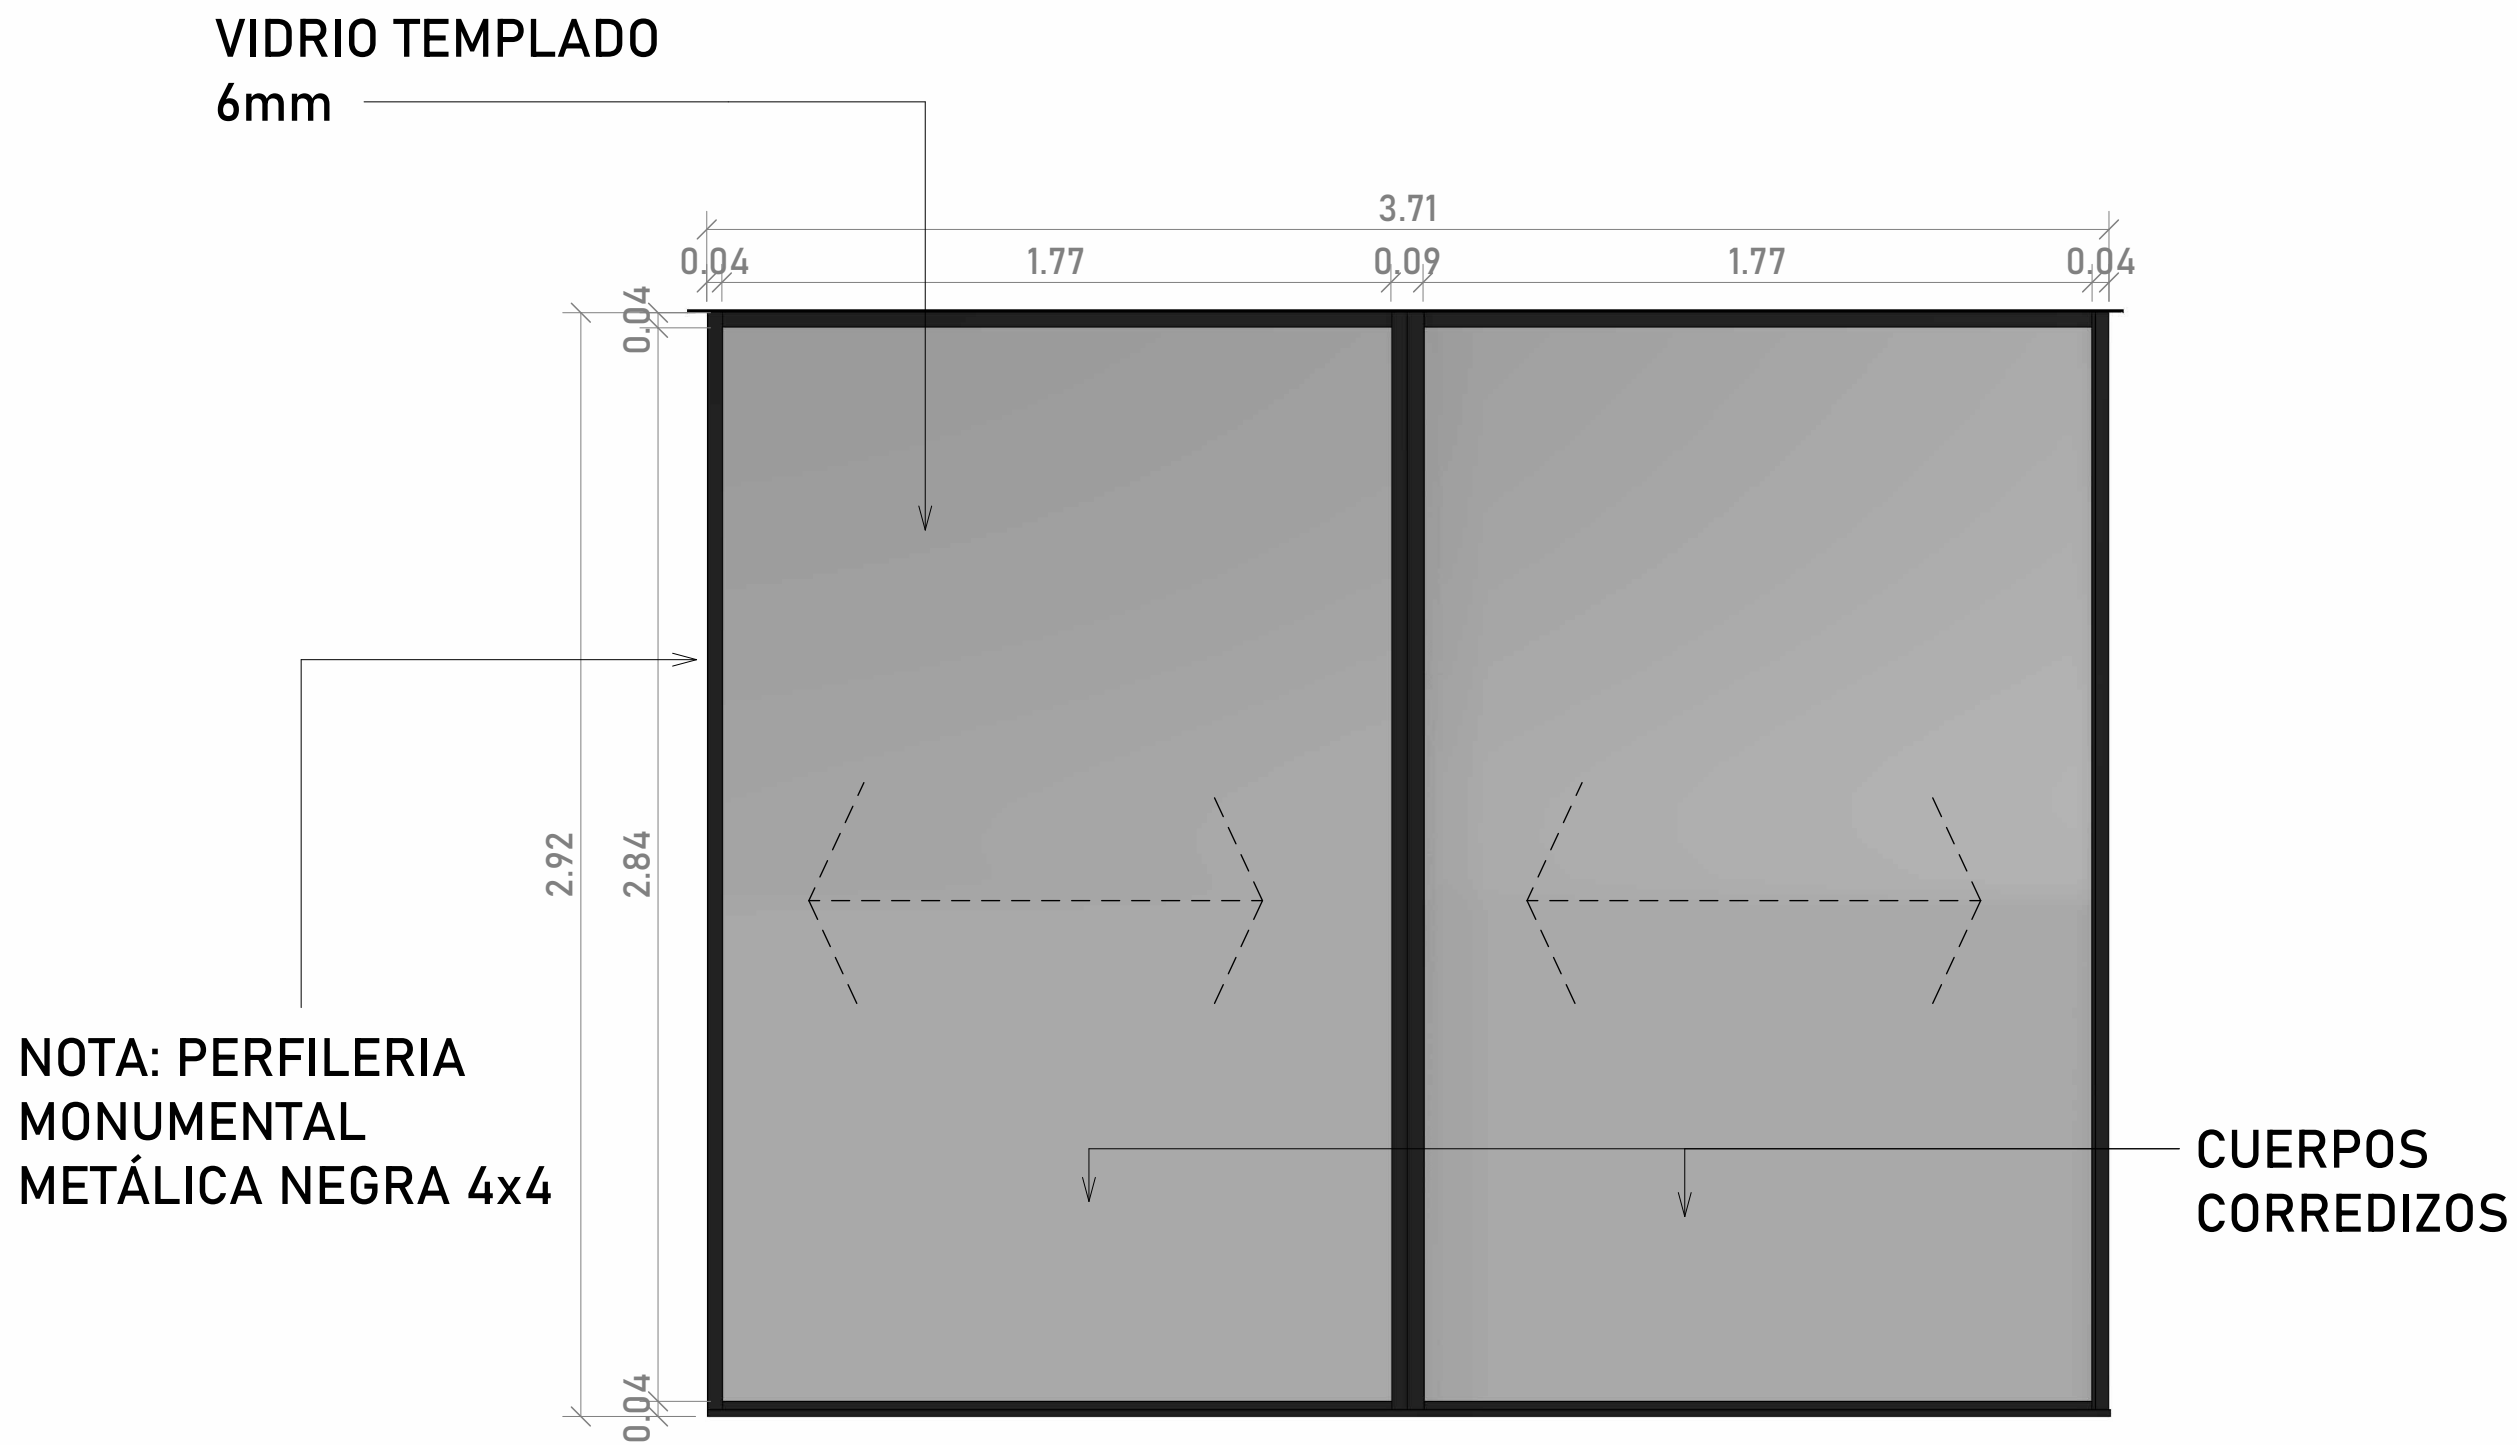

NOTA: PERFILERIA
MONUMENTAL
METÁLICA NEGRA 4x4

CUERPOS
CORREDIZOS

1 ALZADO VENTANA CORREDIZA SALA TV
1: 20

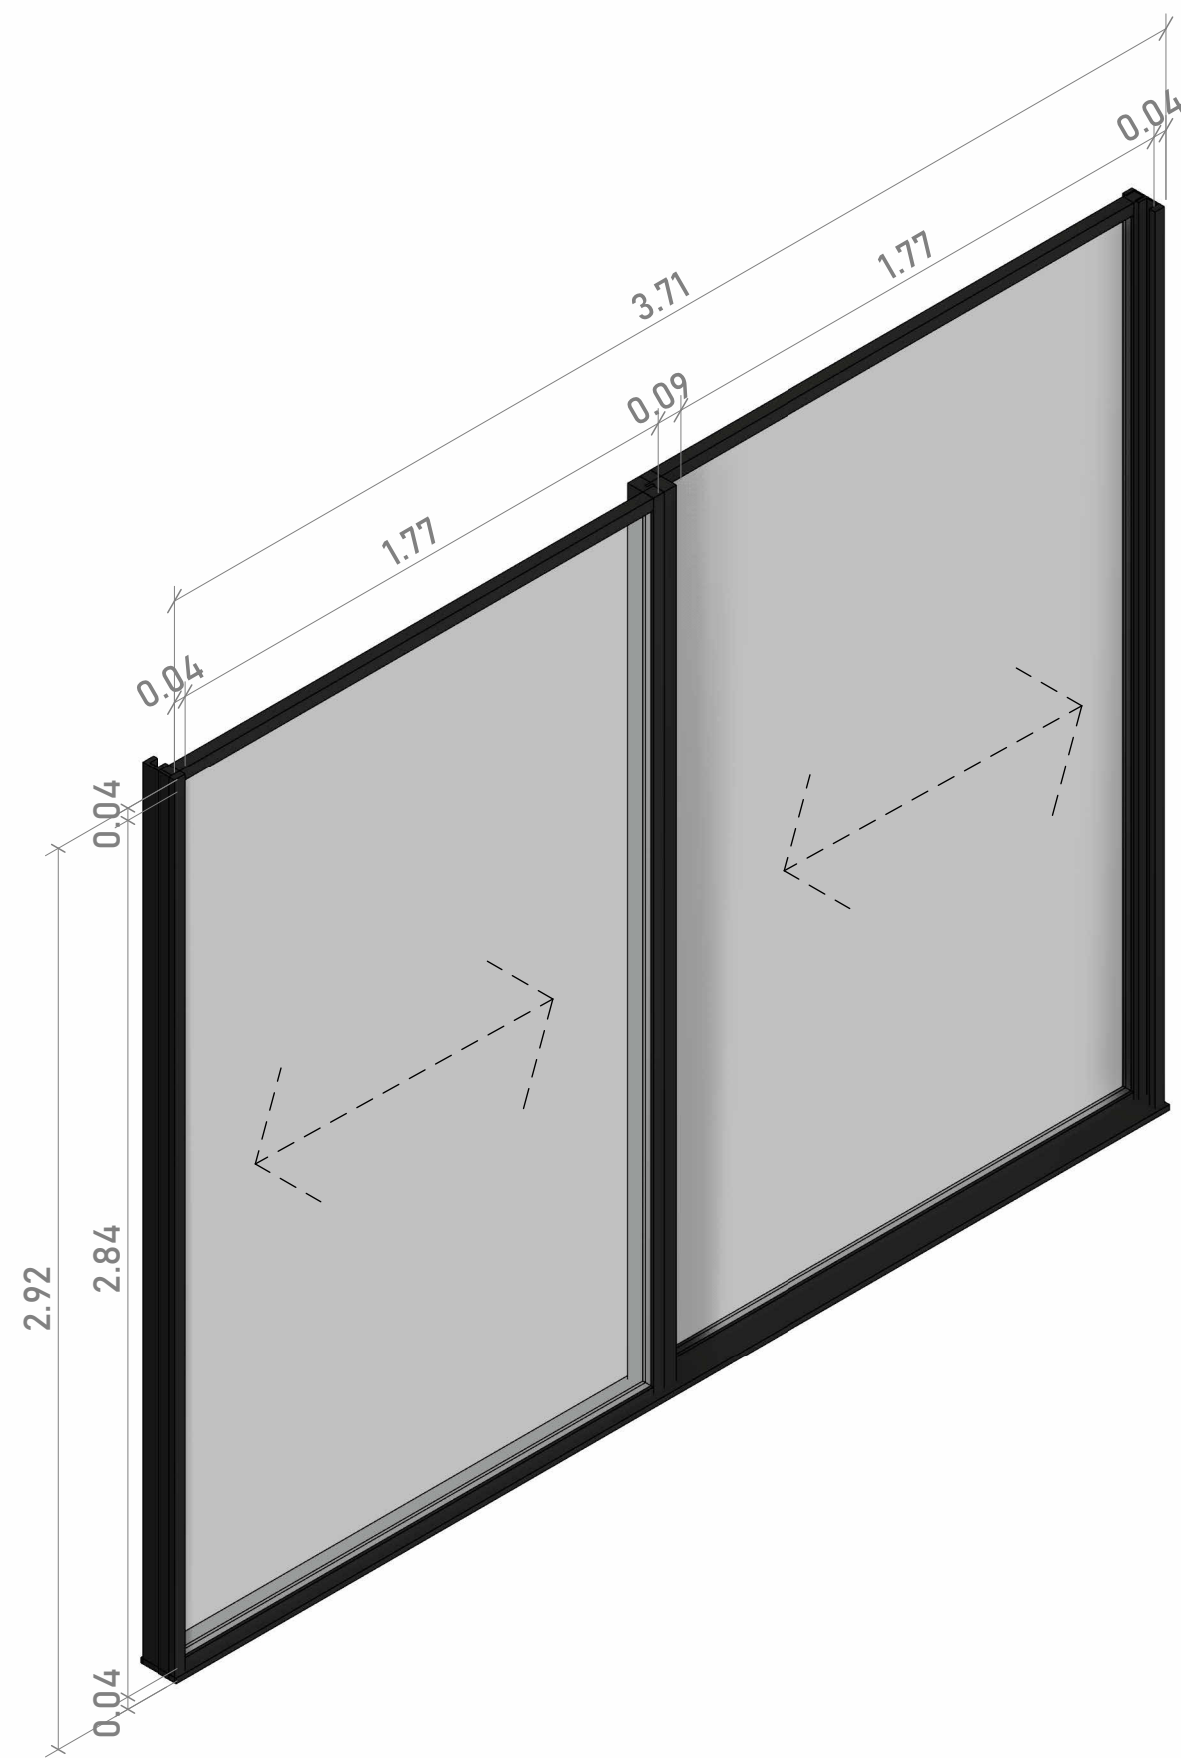

2 VISTA VENTANA CORREDIZA SALA TV
1: 20

Proyecto:

HARAS

Matrícula inmobiliaria:

No 020-238645

Parcelación:

Parcelación Haras
Campestre – P.H.

Número de lote:

Lote No. 4 Llanogrande

Observaciones:

Según NSR-10

Revisa:

ANA SOFIA ROLDAN

Verifica:

DANIELA ARIZA RAMIREZ

Aprueba:

DANIELA ARIZA RAMIREZ

Ciente:

SANDRA MEJIA VELEZ Y
EDWIN ALFREDO ACOSTA

Diseño:

DANIELA ARIZA RAMIREZ

Cálculos estructurales:

12/11/25

Archivo de Referencia:

20251212_DISEÑO HARAS

Contiene:

MUEBLE BBQ

Escala:

1:10

Fecha:

2025/22/12

Dibujo:

JORDY PINEDA BELLIDO


Plancha N°:

A 6

De:

9

Firmas:

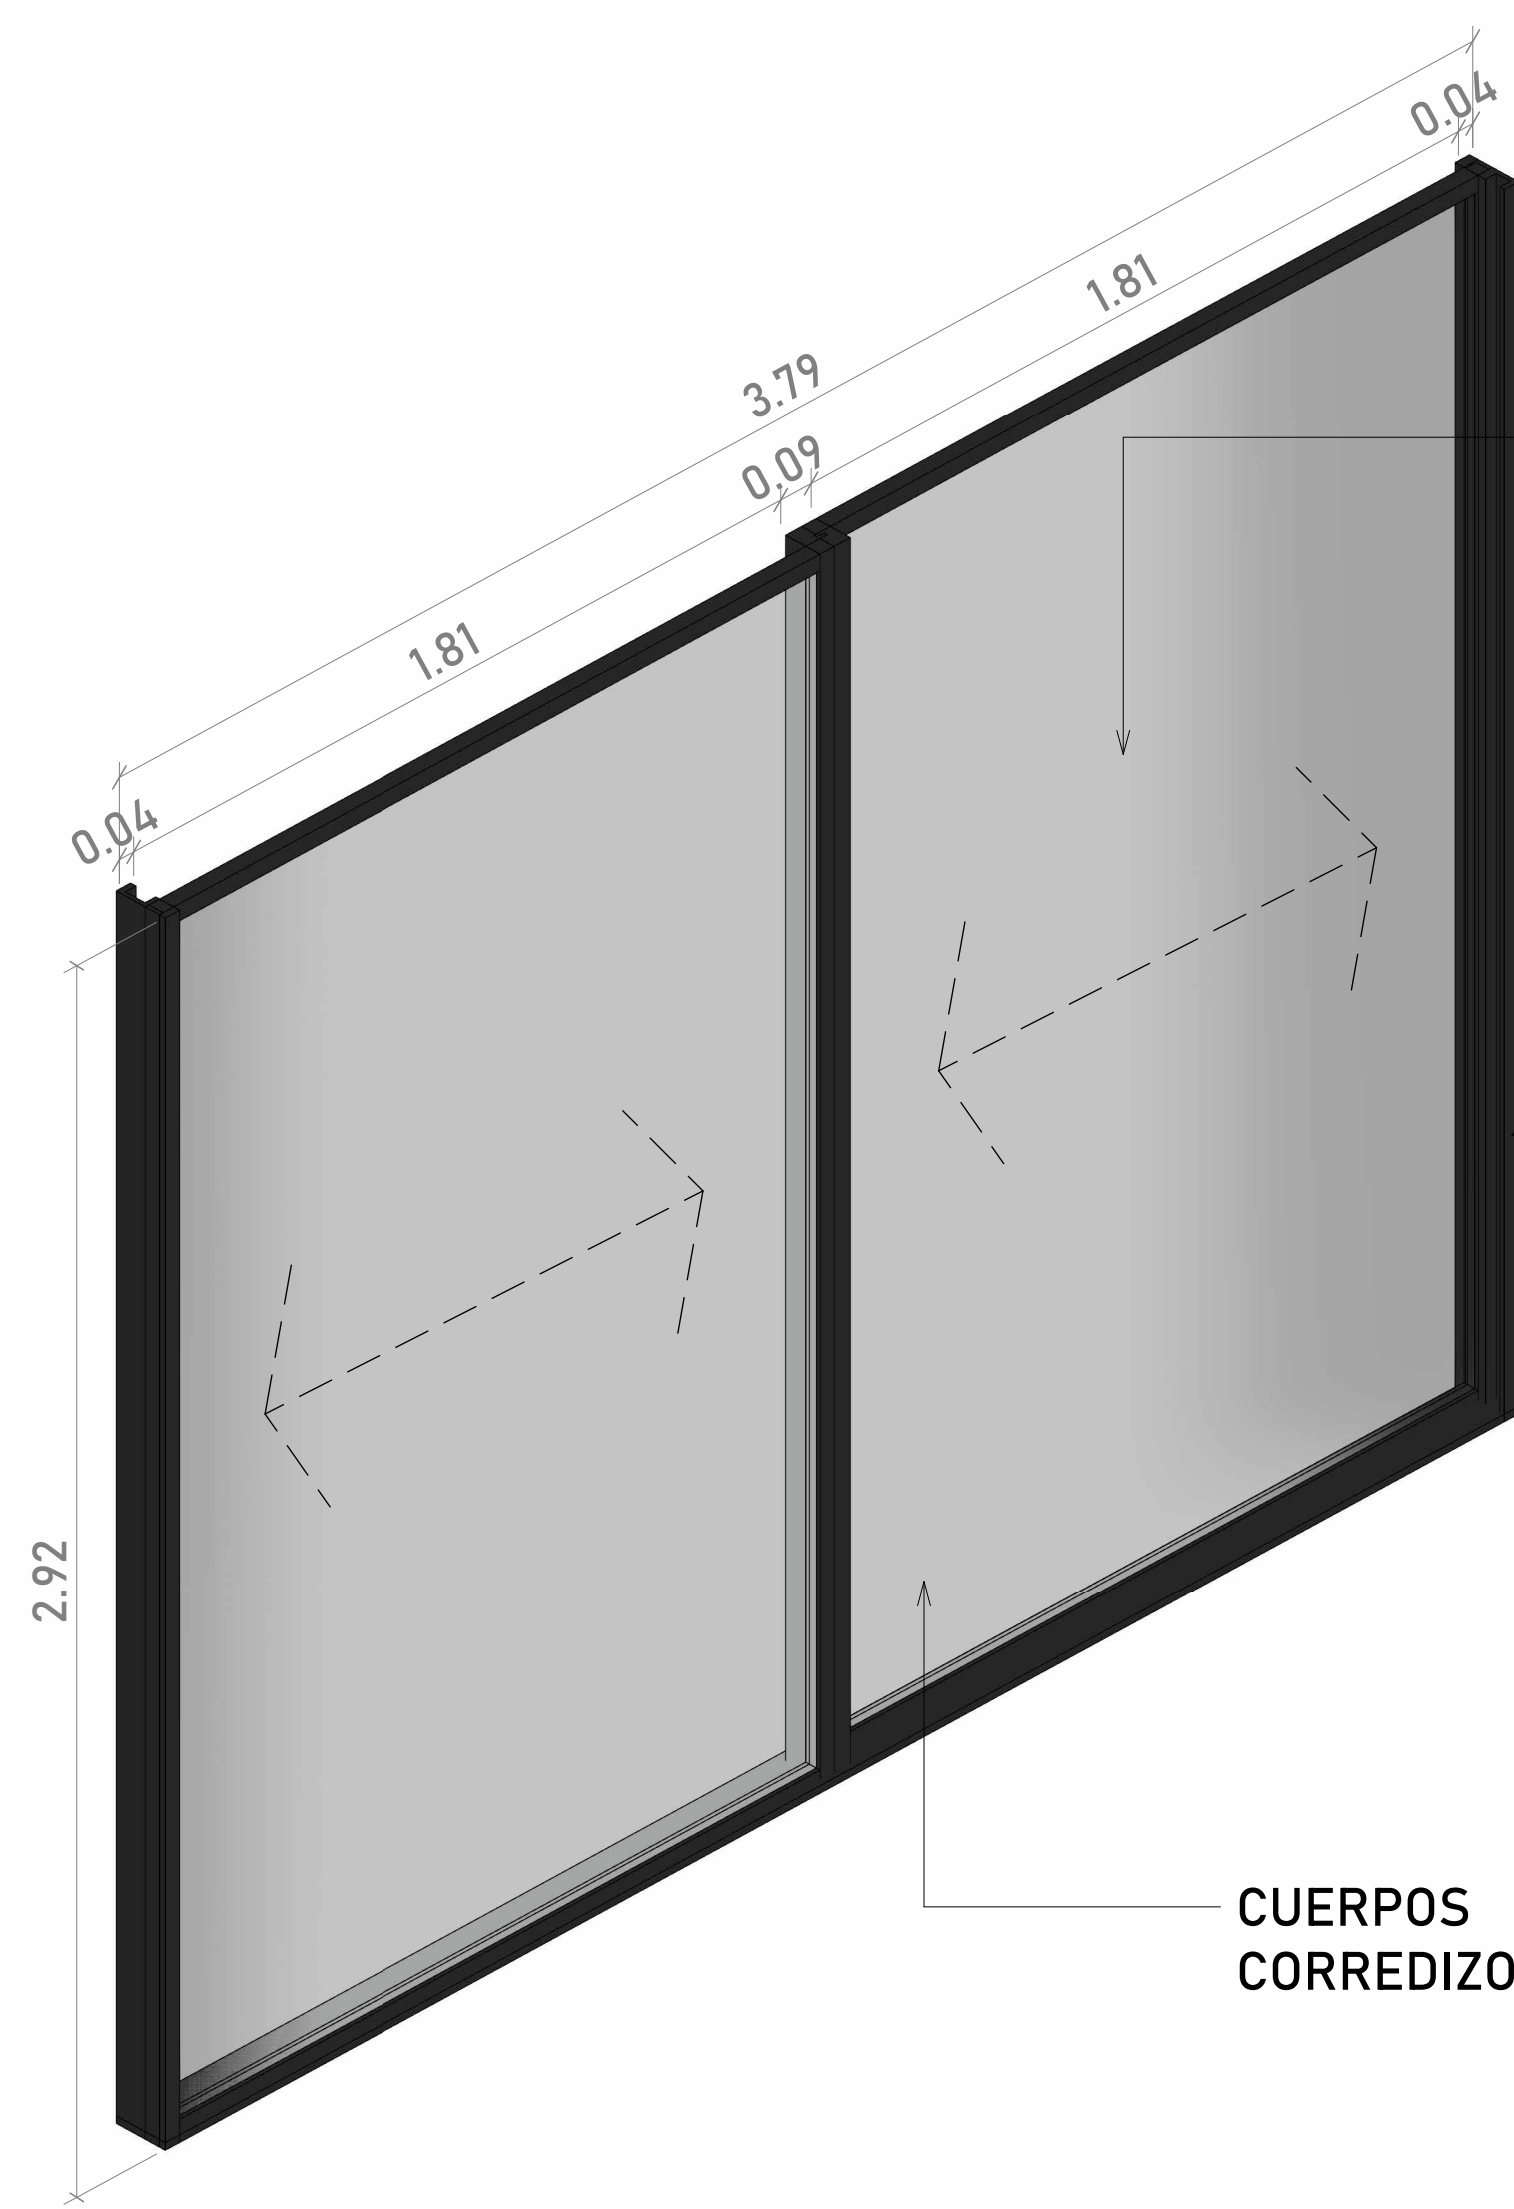


VIDRIO
TEMPLADO
8mm

NOTA:
PERFILERIA
MONUMENTAL
METÁLICA
NEGRA 4x4

CUERPOS
CORREDIZOS

1 VENTANA CORREDIZA HABITACIÓN 3
1: 25

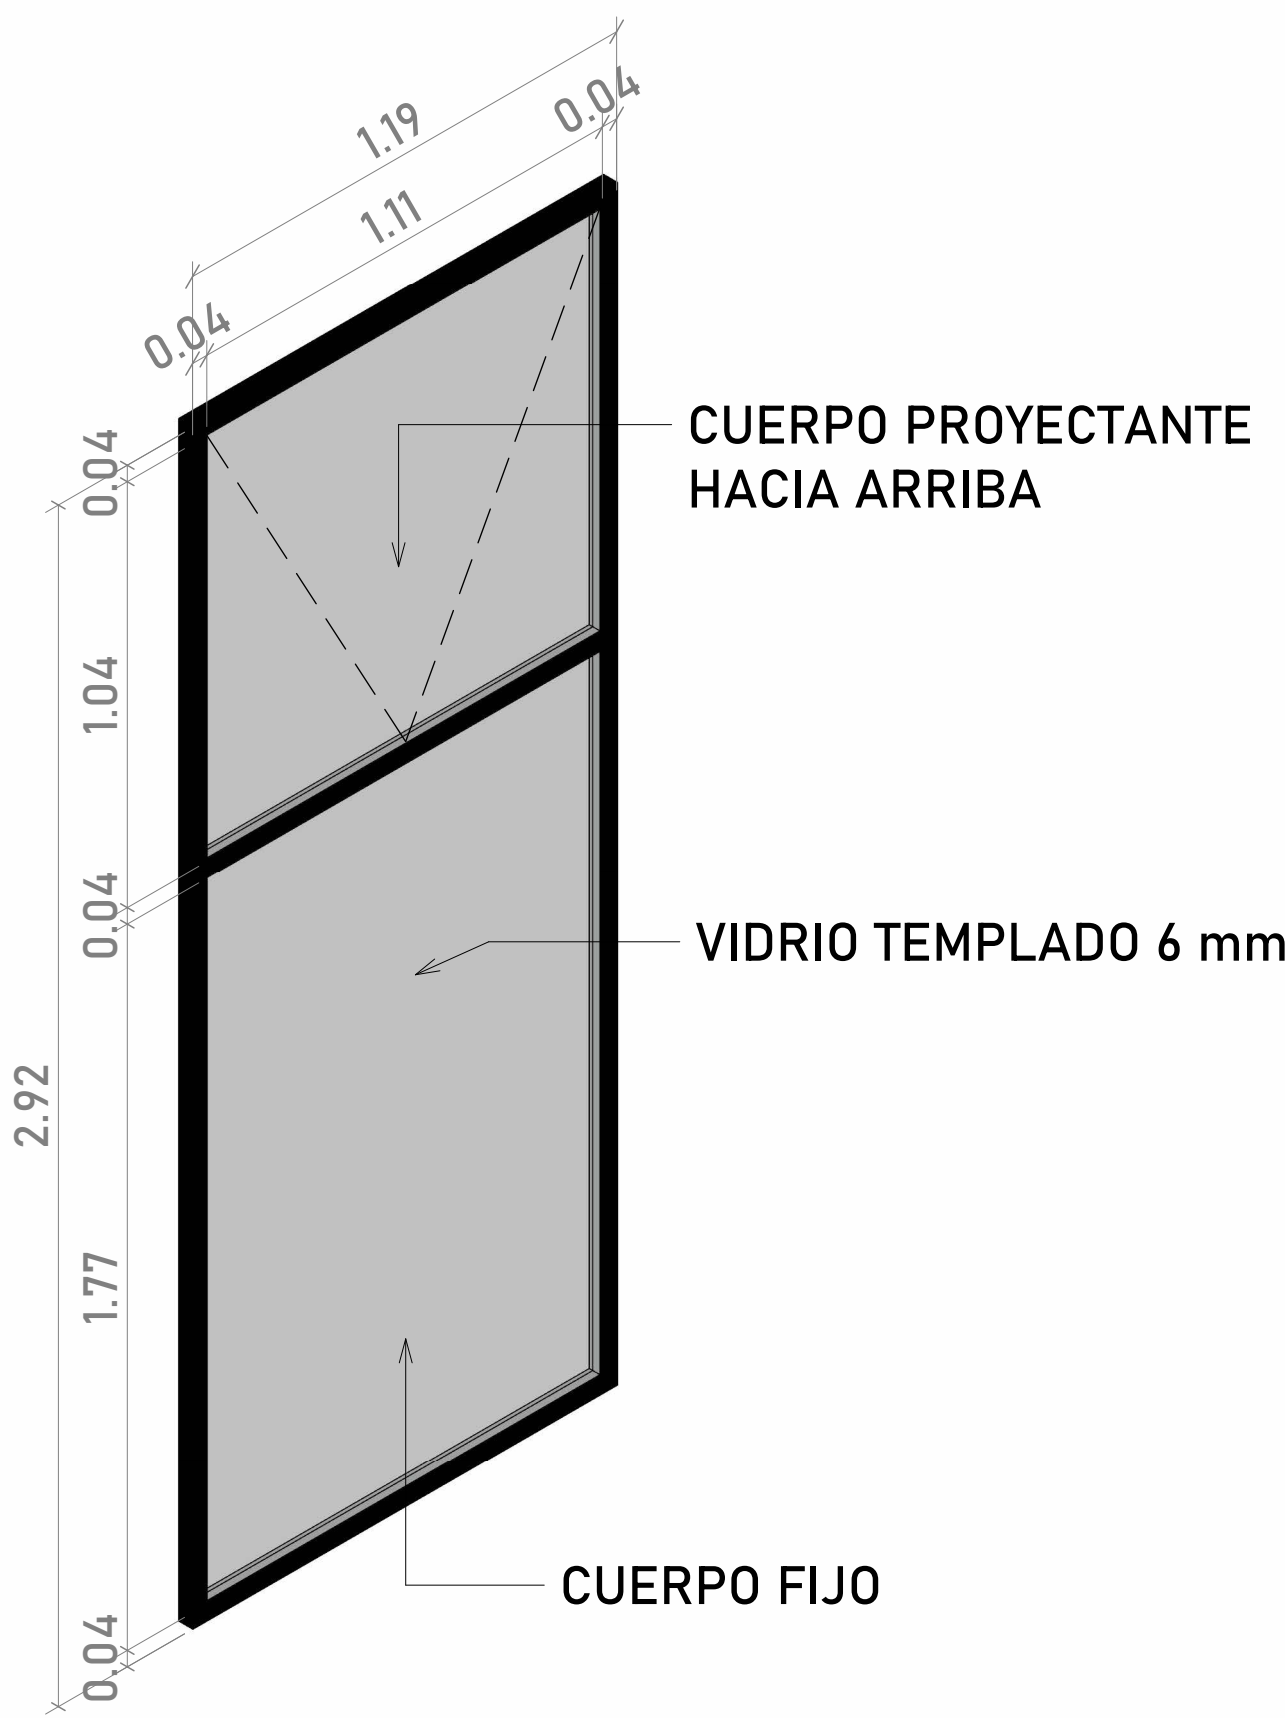


CUERPO PROYECTANTE
HACIA ARRIBA

VIDRIO TEMPLADO 6 mm

CUERPO FIJO

2 VENTANA DUCHA HABITACIÓN 3
1: 25

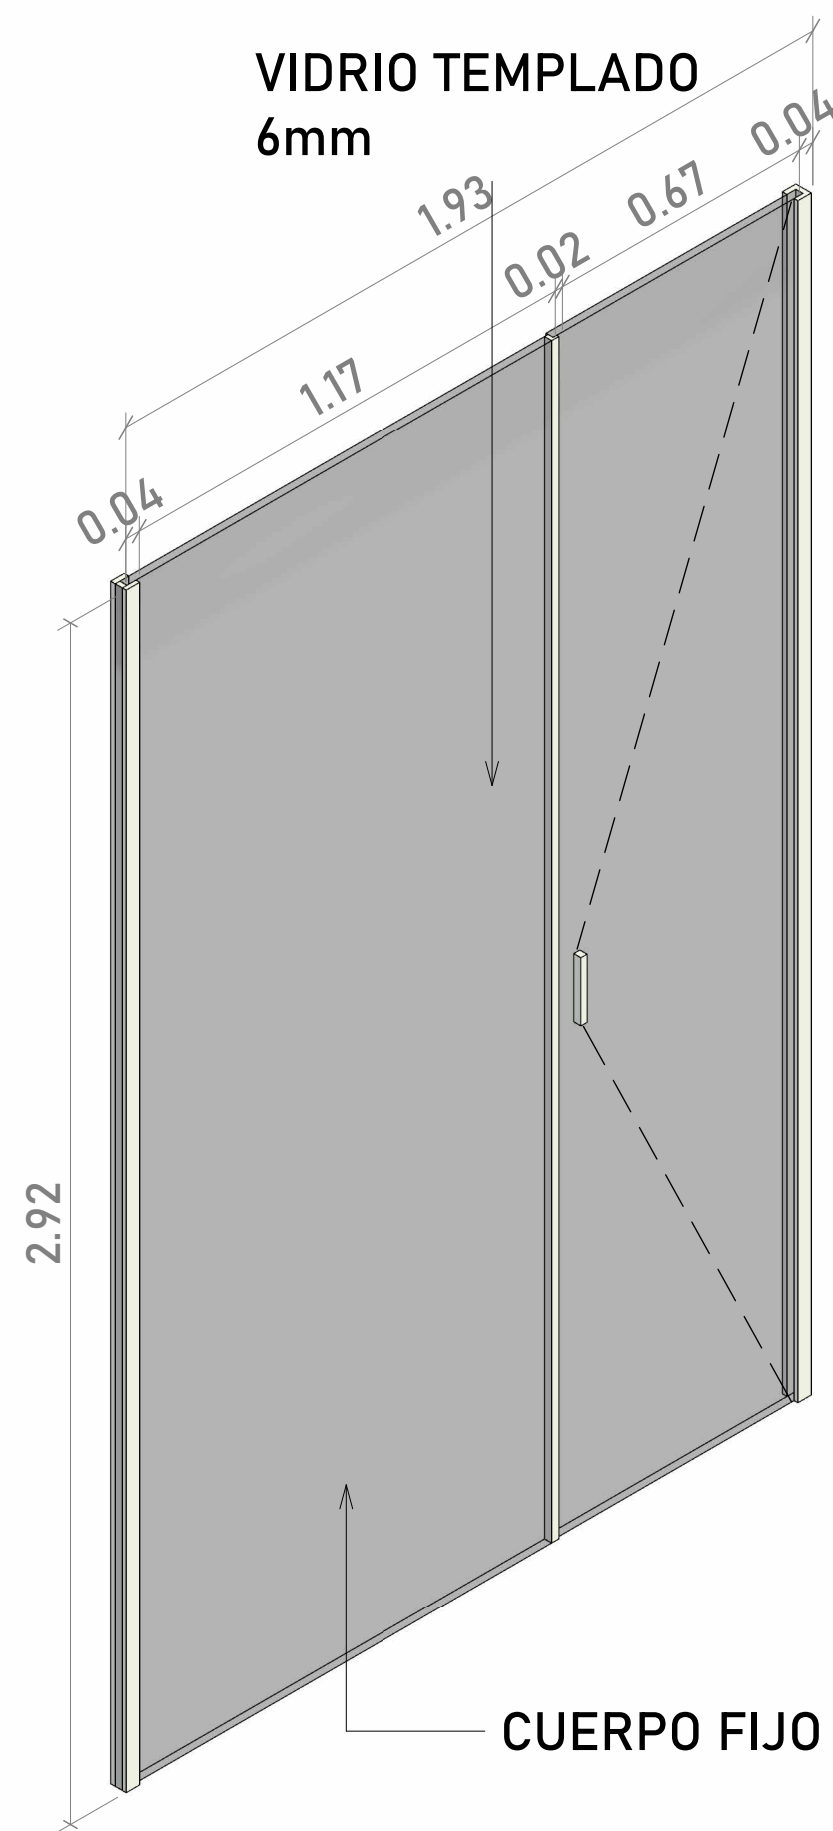


VIDRIO TEMPLADO
6mm

CUERPO FIJO


3 CABINA DUCHA HABITACIÓN 3
1: 25

NOTA: PUERTA CORREDIZA
EMPOTRADA EN MURO

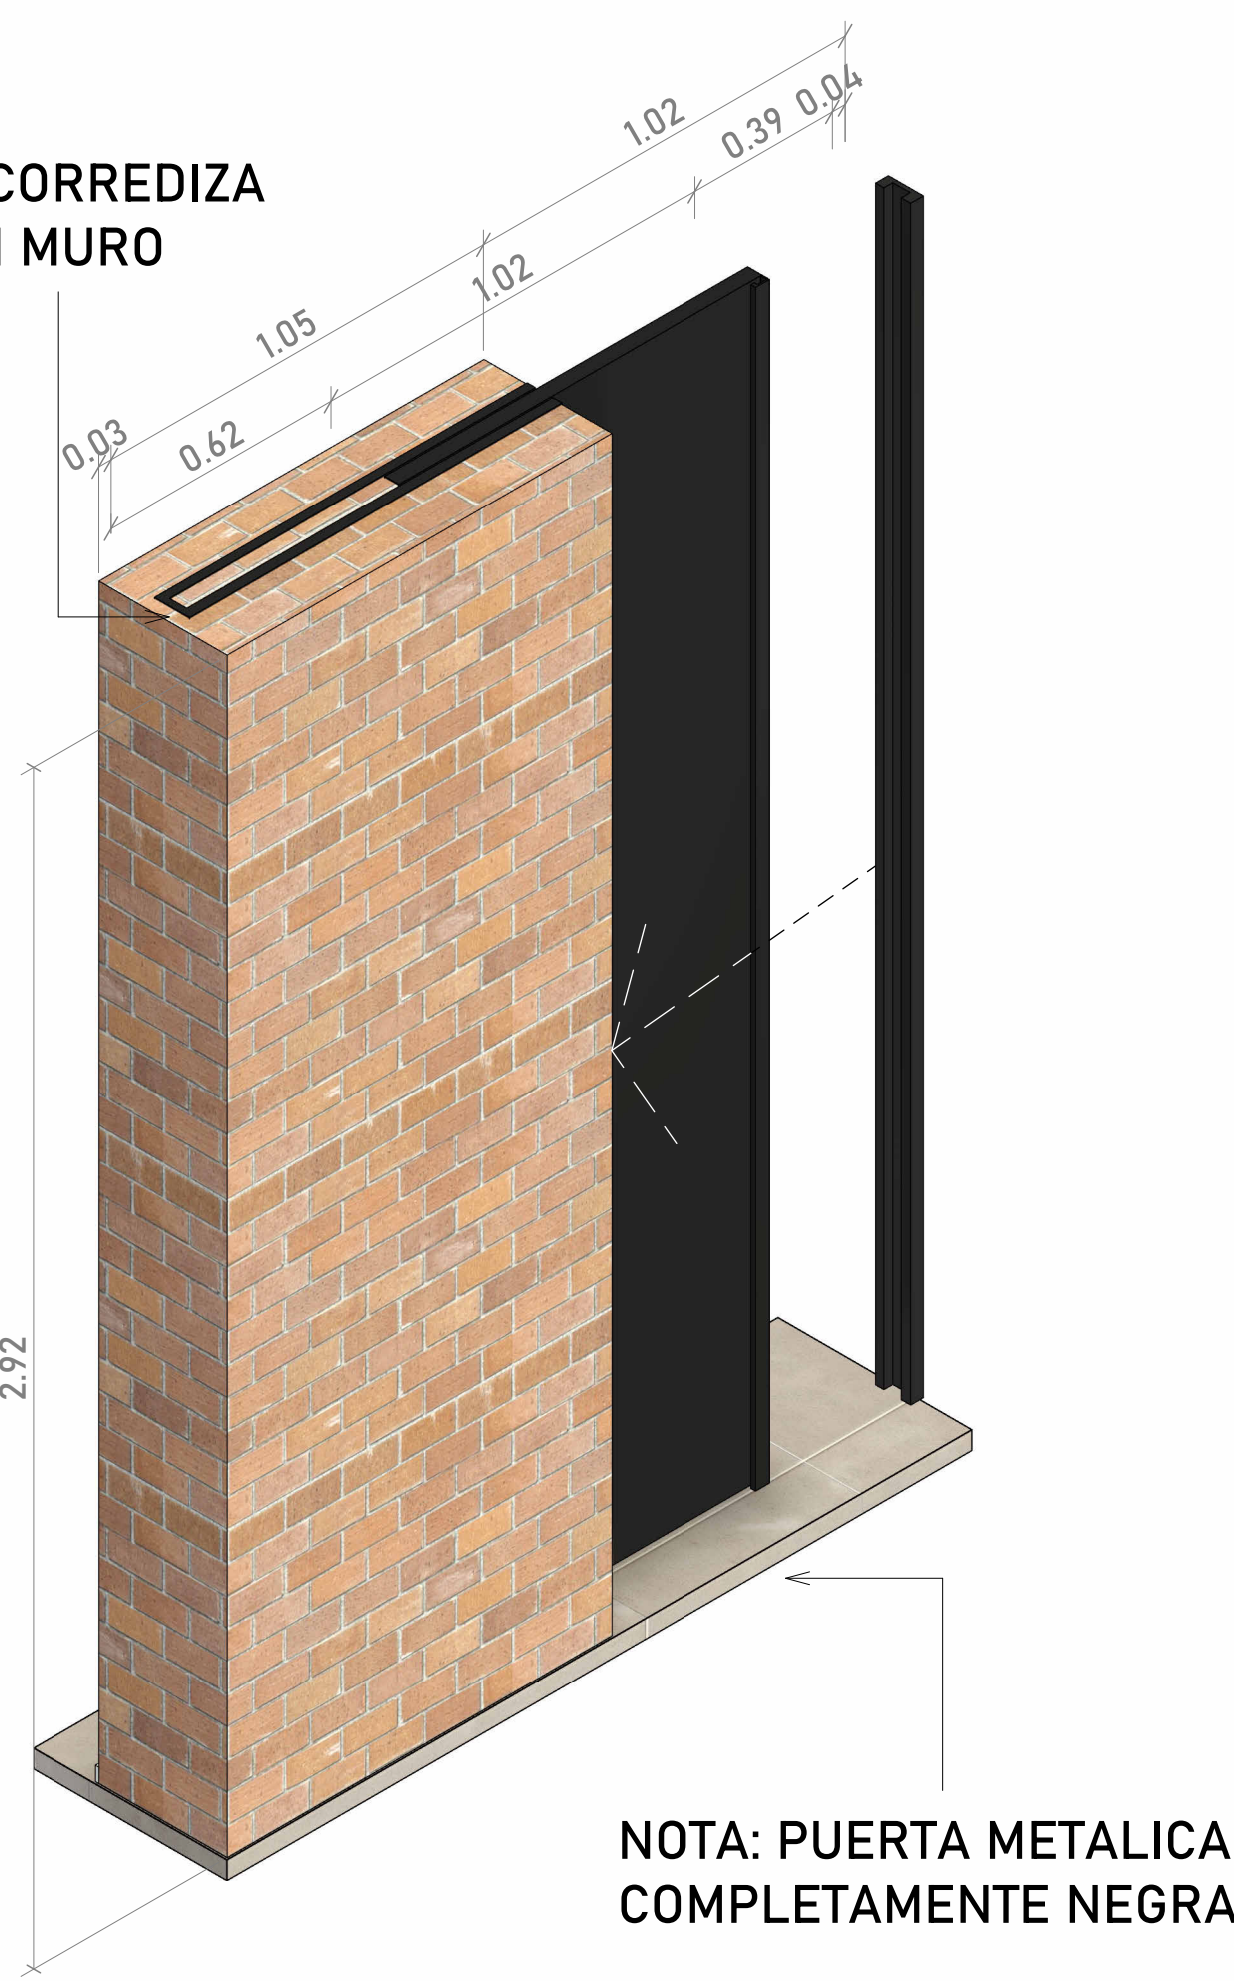


NOTA: PUERTA METALICA
COMPLETAMENTE NEGRA


4 PUERTA EMPOTRADA SALA
1: 25

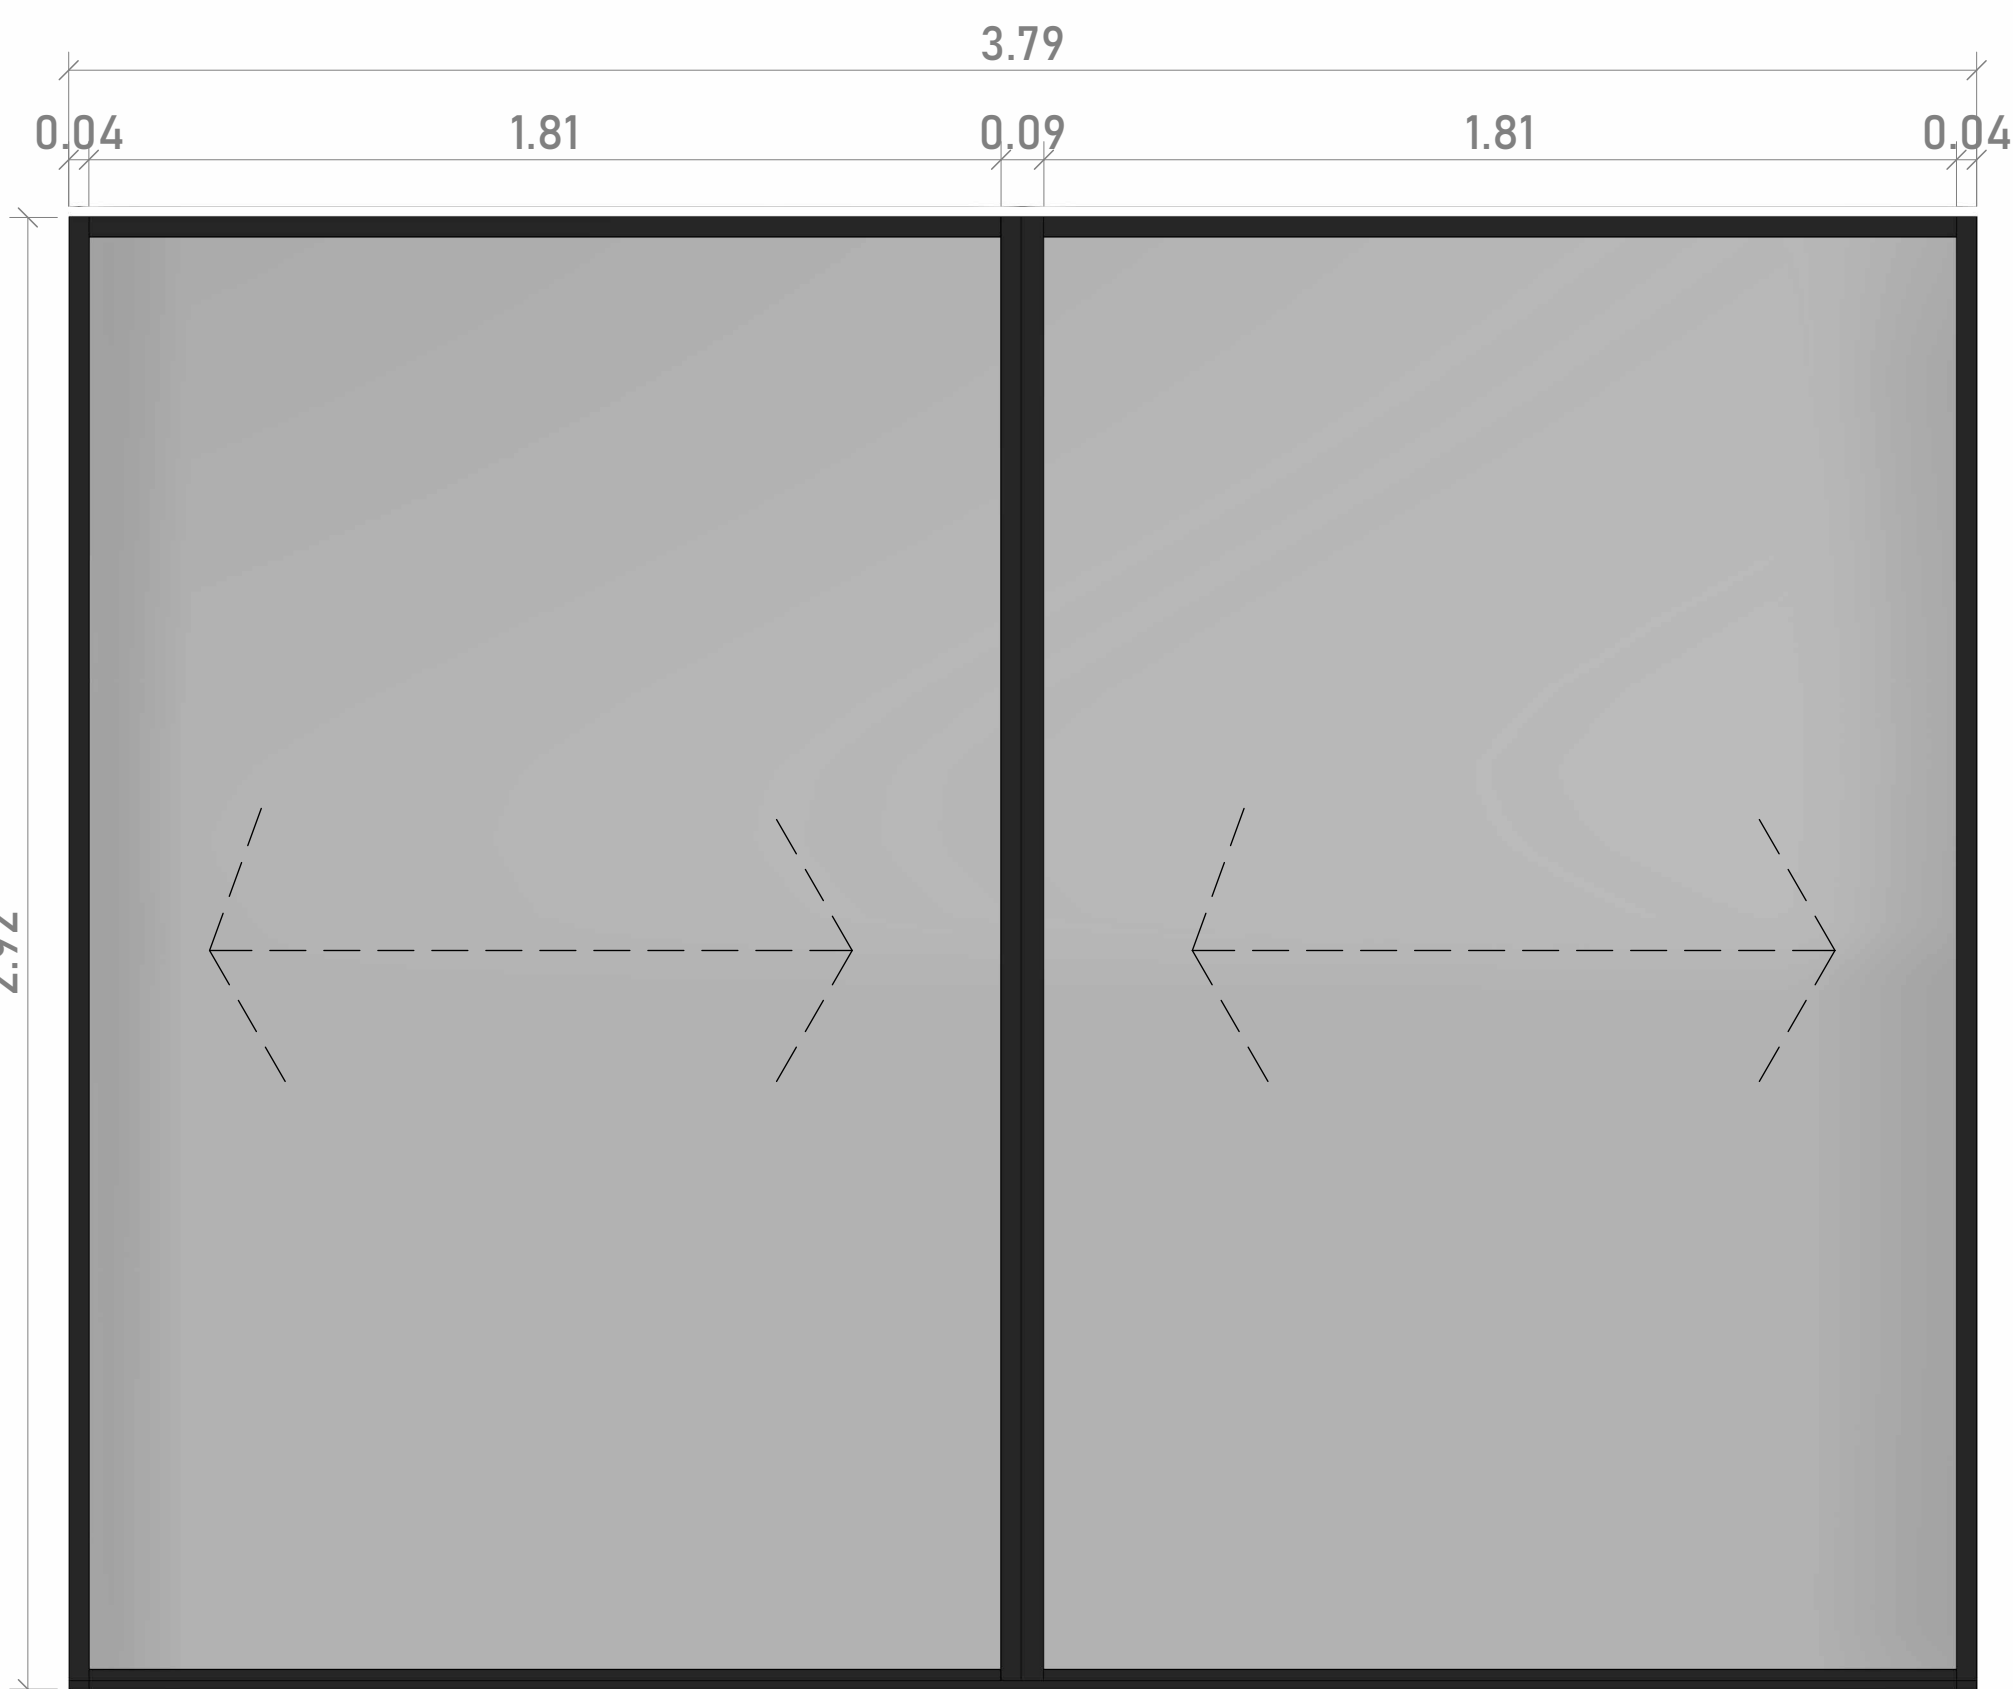


1 VENTANA CORREDIZA HABITACIÓN 3
1: 25

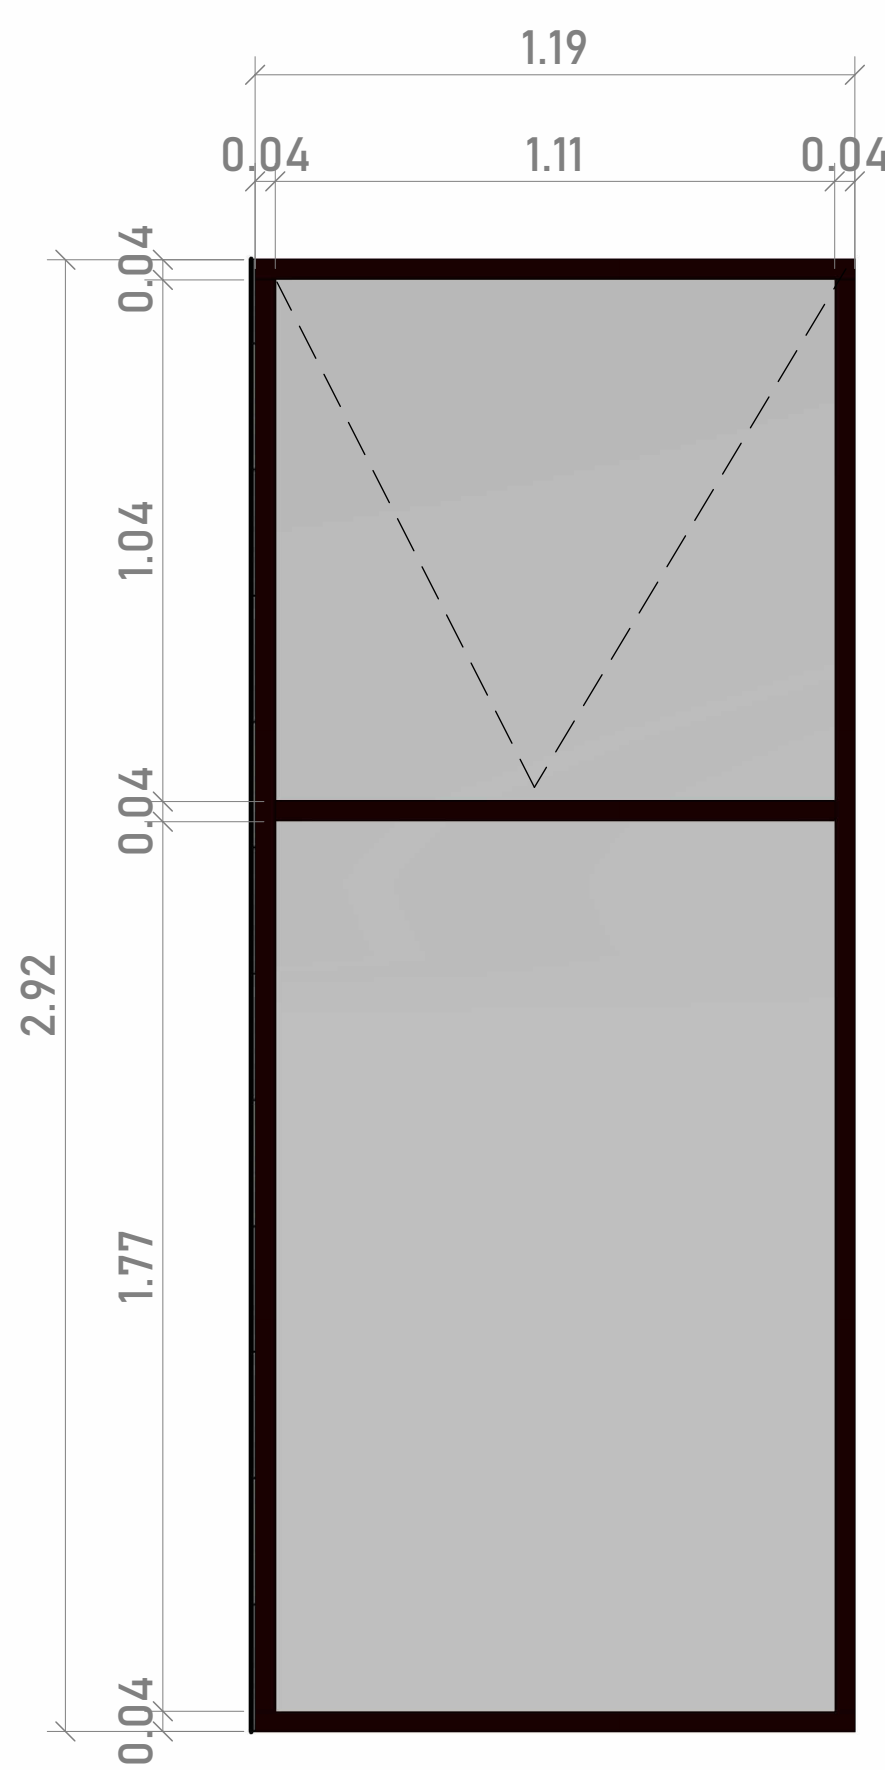


2 VENTANA DUCHA HABITACIÓN 3
1: 25

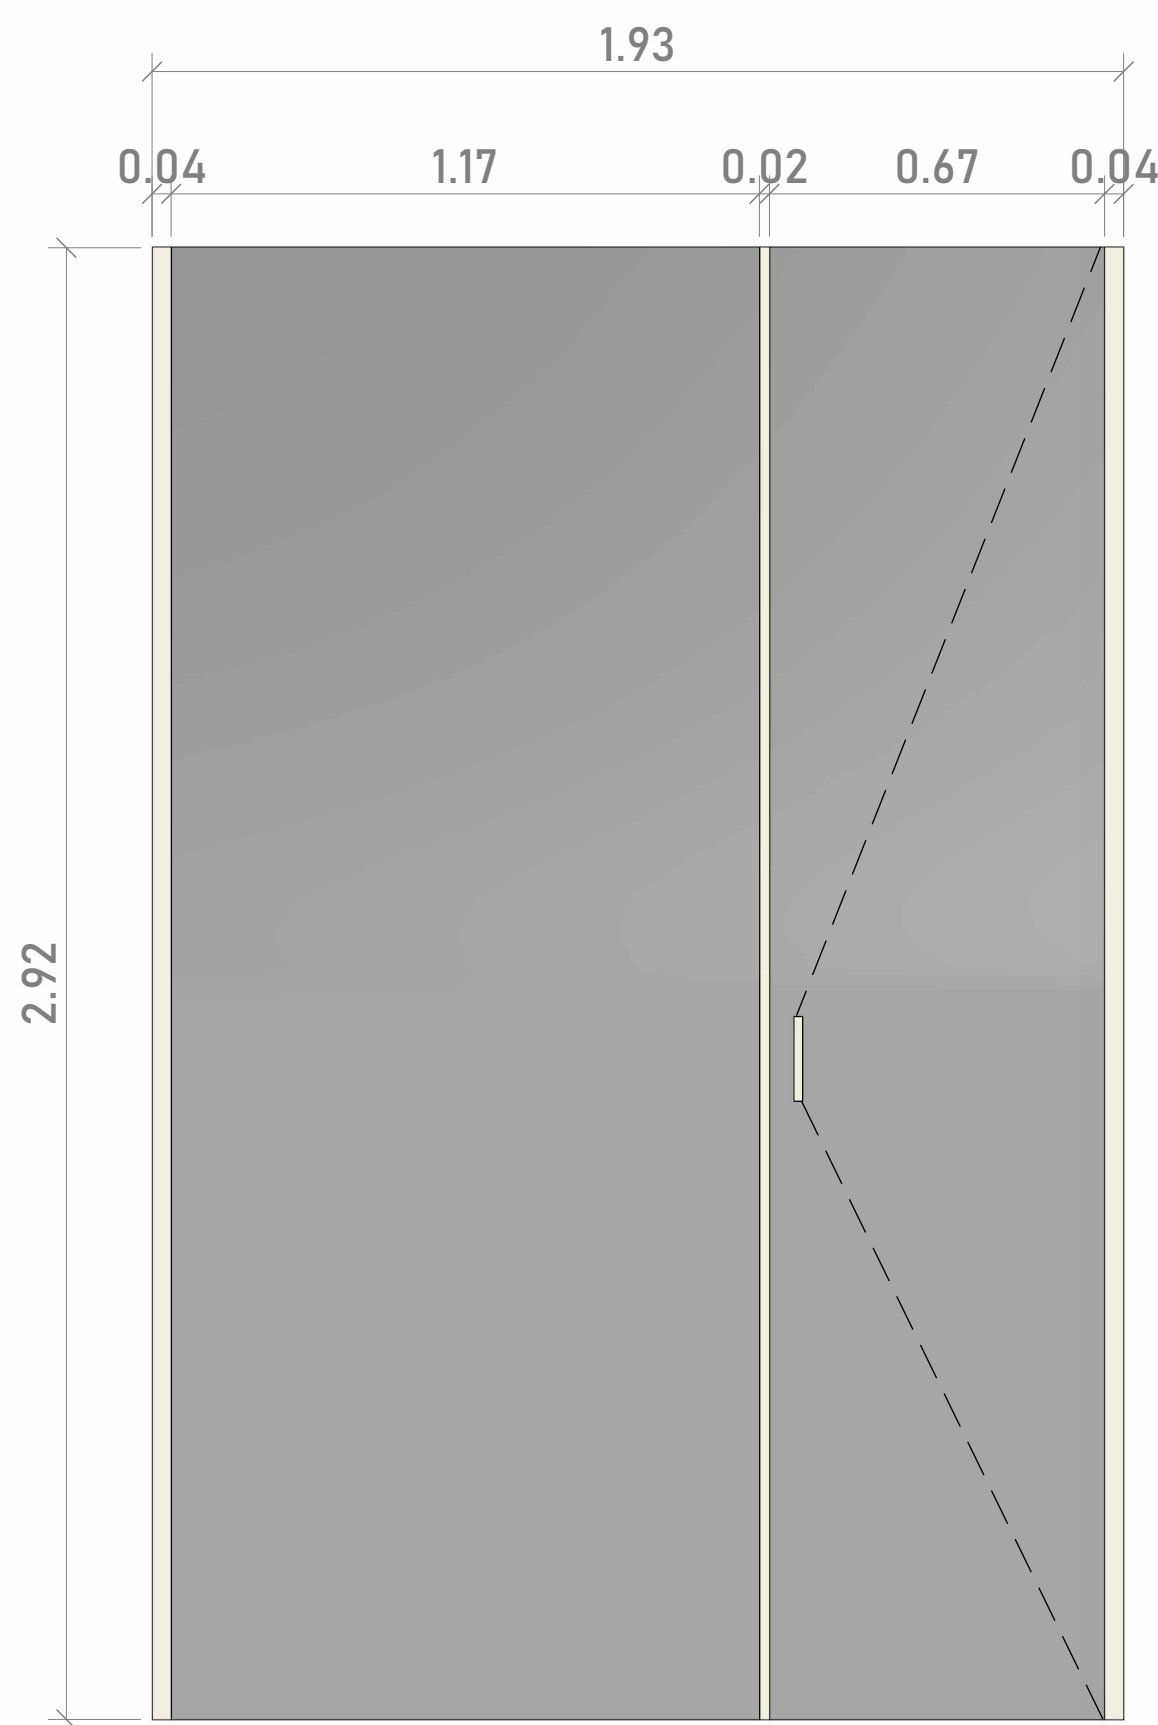

3 CABINA DUCHA HABITACIÓN 3
1: 25

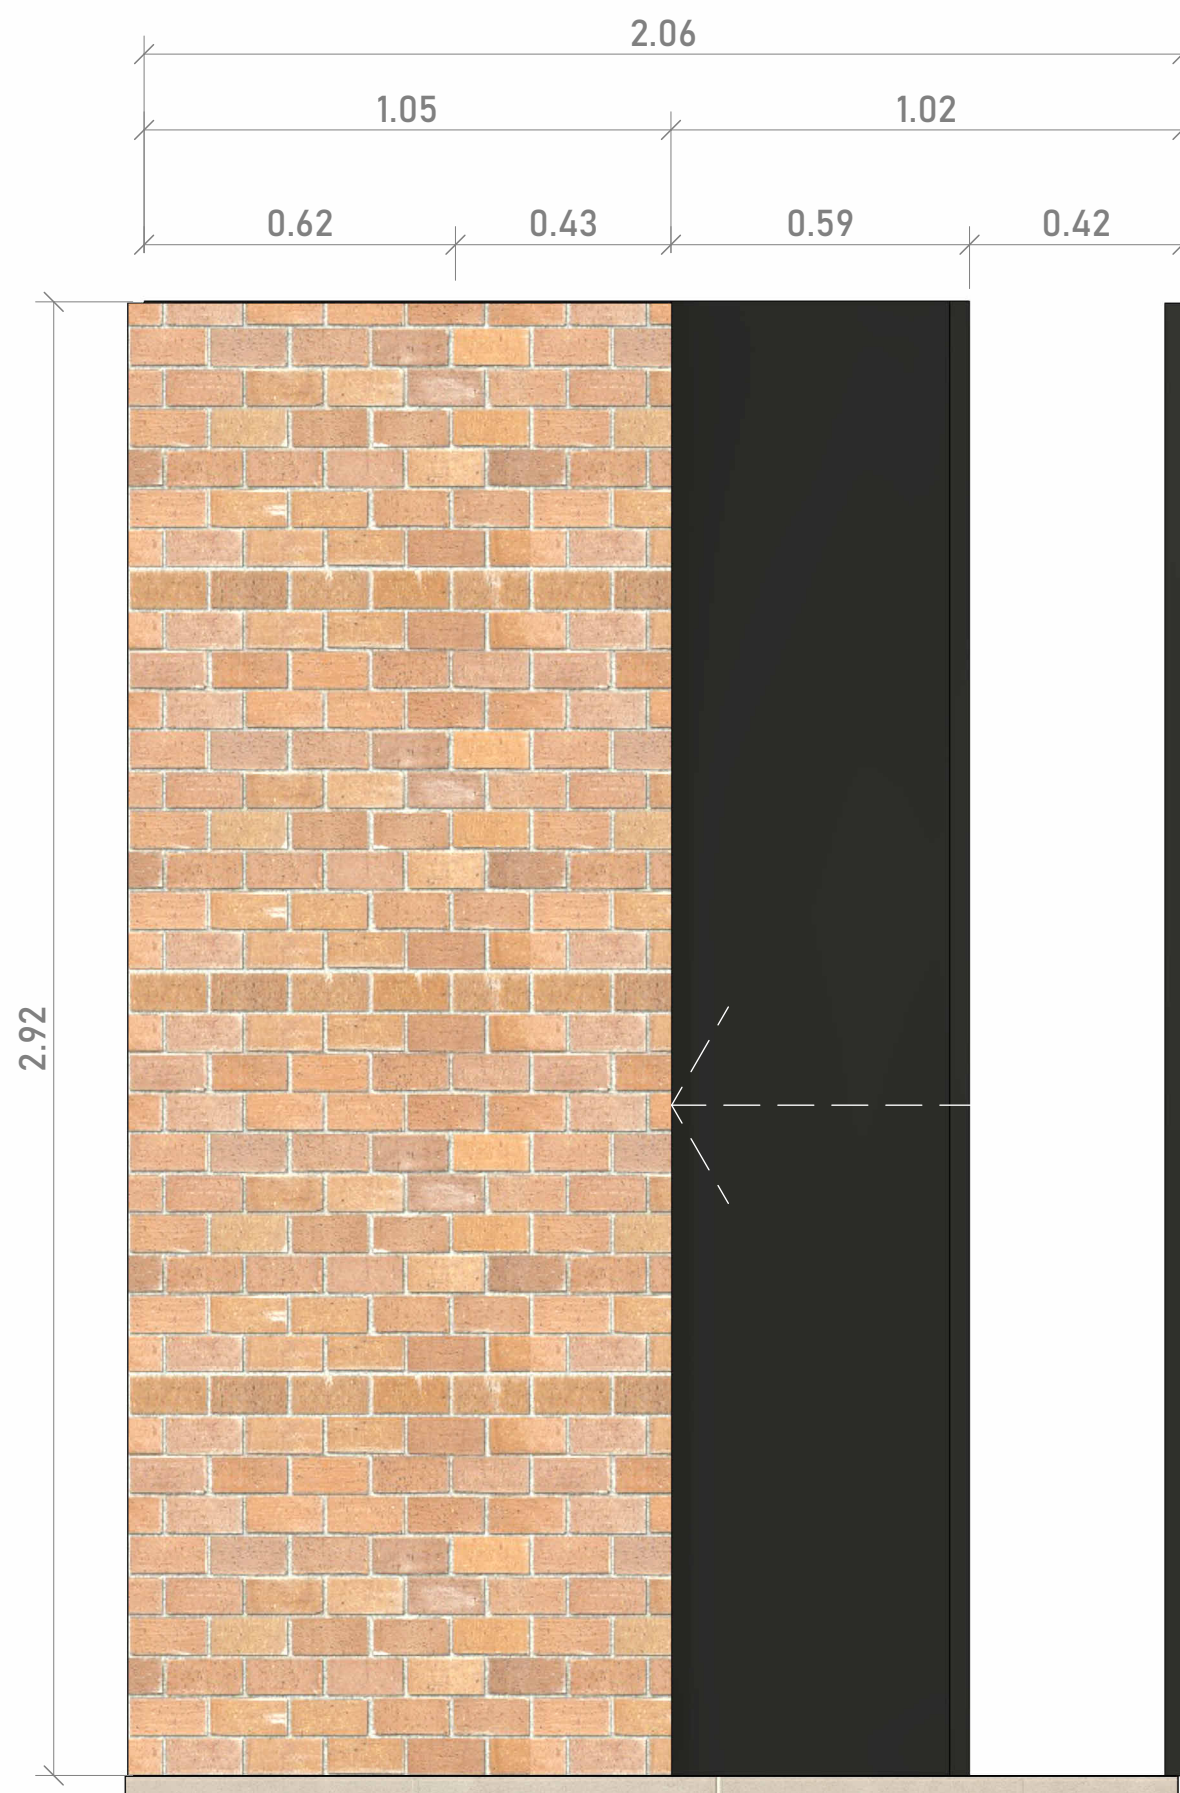

4 PUERTA EMPOTRADA SALA
1: 25

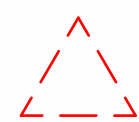

NOTA: TODAS LAS VISTAS EN ISOMETRICO
ESTÁN ORIENTADAS DE ADENTRO HACIA
AFUERA


idea/base. ARQUITECTOS	
Proyecto: HARAS	
Matrícula inmobiliaria: No 020-238645	
Parcelación: Parcelación Haras Campestre – P.H.	
Número de lote: Lote No. 4 Llanogrande	
Observaciones: Según NSR-10	
Revisa: ANA SOFIA ROLDAN	
Verifica: DANIELA ARIZA RAMIREZ	
Aprueba: DANIELA ARIZA RAMIREZ	
Cliente: SANDRA MEJIA VELEZ Y EDWIN ALFREDO ACOSTA	
Diseño: DANIELA ARIZA RAMIREZ	
Cálculos estructurales: 12/05/25	
Archivo de Referencia: 20251212_DISEÑO HARAS	
Contiene: CARP METÁLICA HAB 3	
Escala: 1:10	Fecha: 2025/22/12
Dibujo: JORDY PINEDA BELLIDO	
Plancha Nº: A 7	De: 9
Firmas:	




1 ESPEJO BAÑO SOCIAL
ESC 1:15




2 ESPEJO VESTIER HABITACIÓN PPAL
ESC 1:10

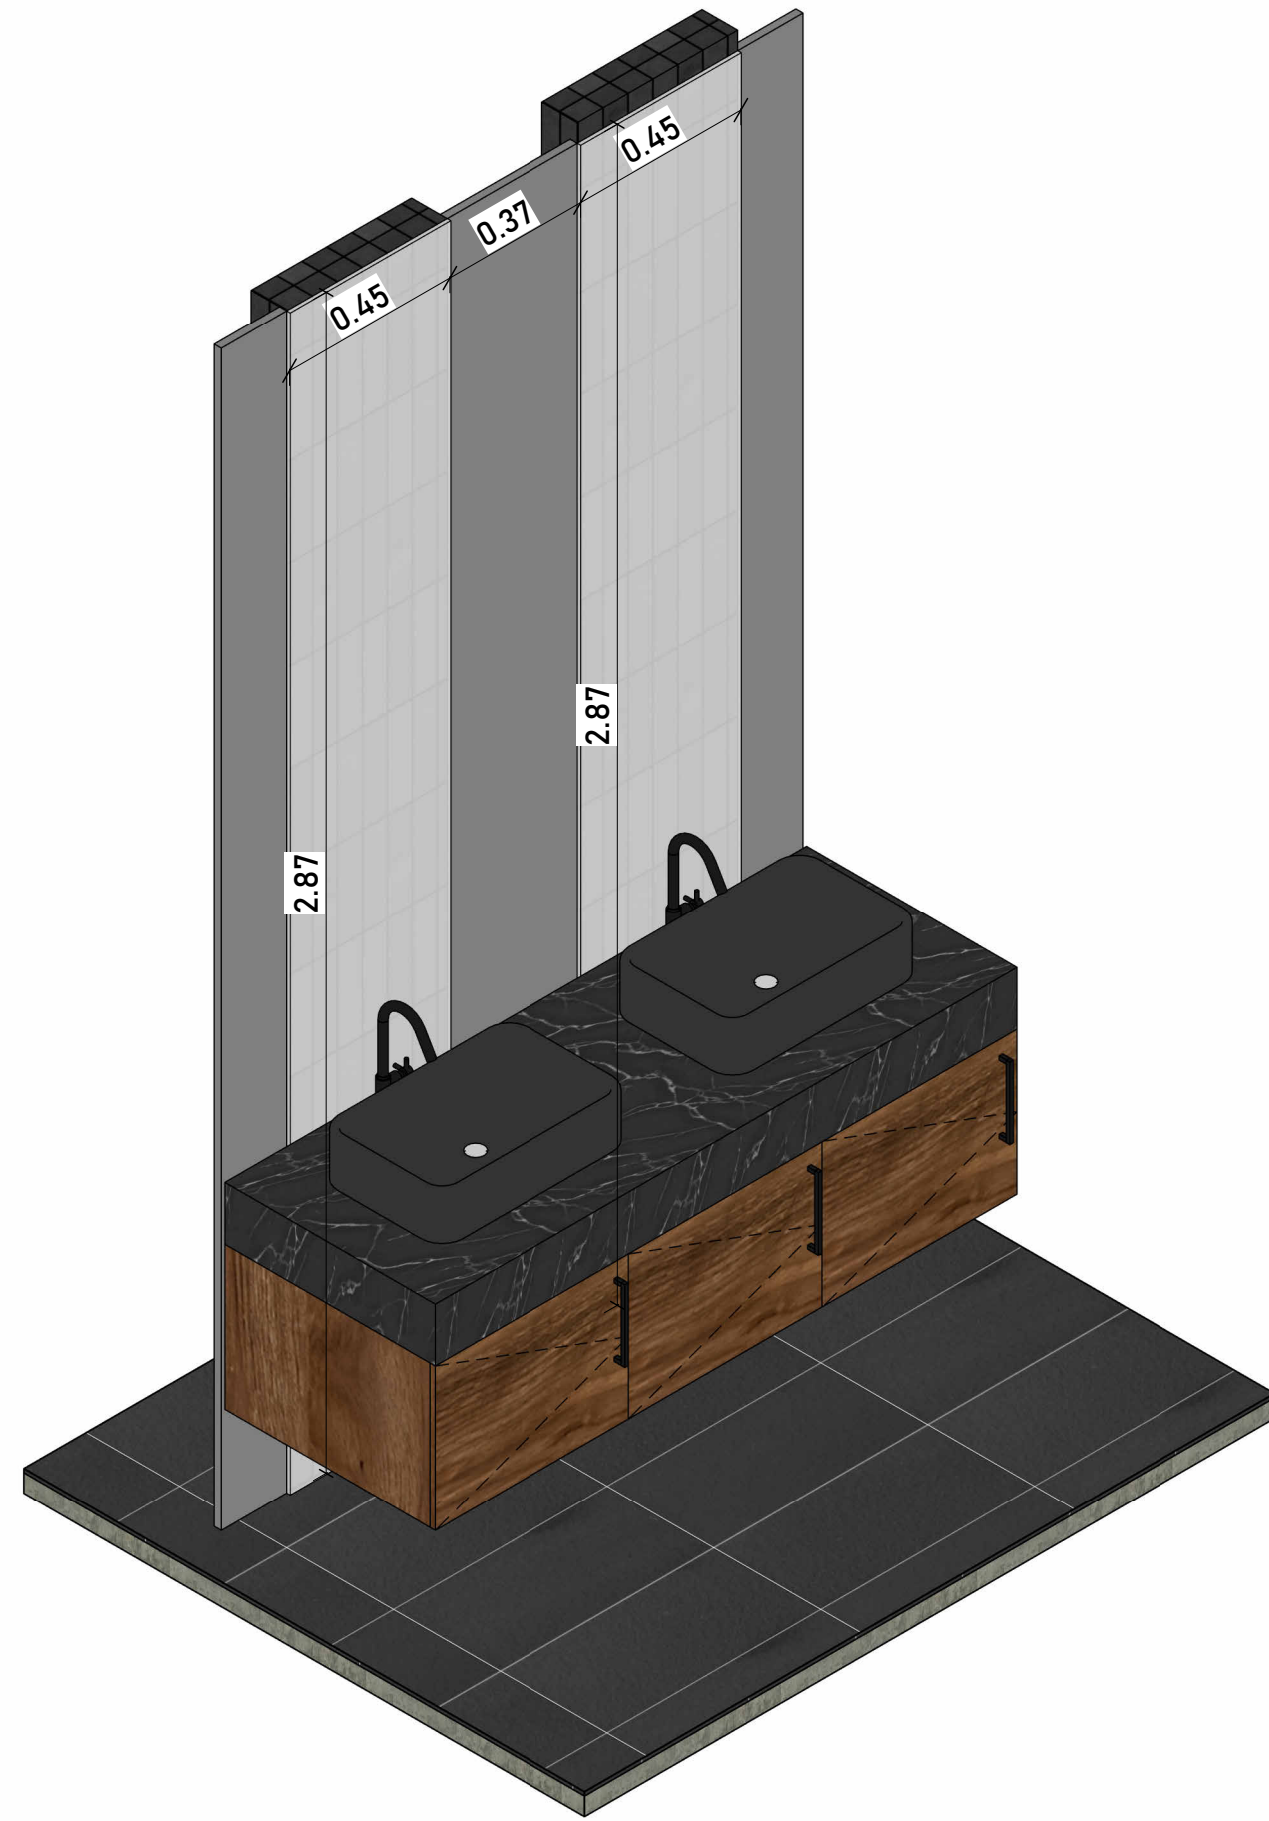


3 ESPEJO BAÑO HABITACIÓN PPAL
ESC 1:10

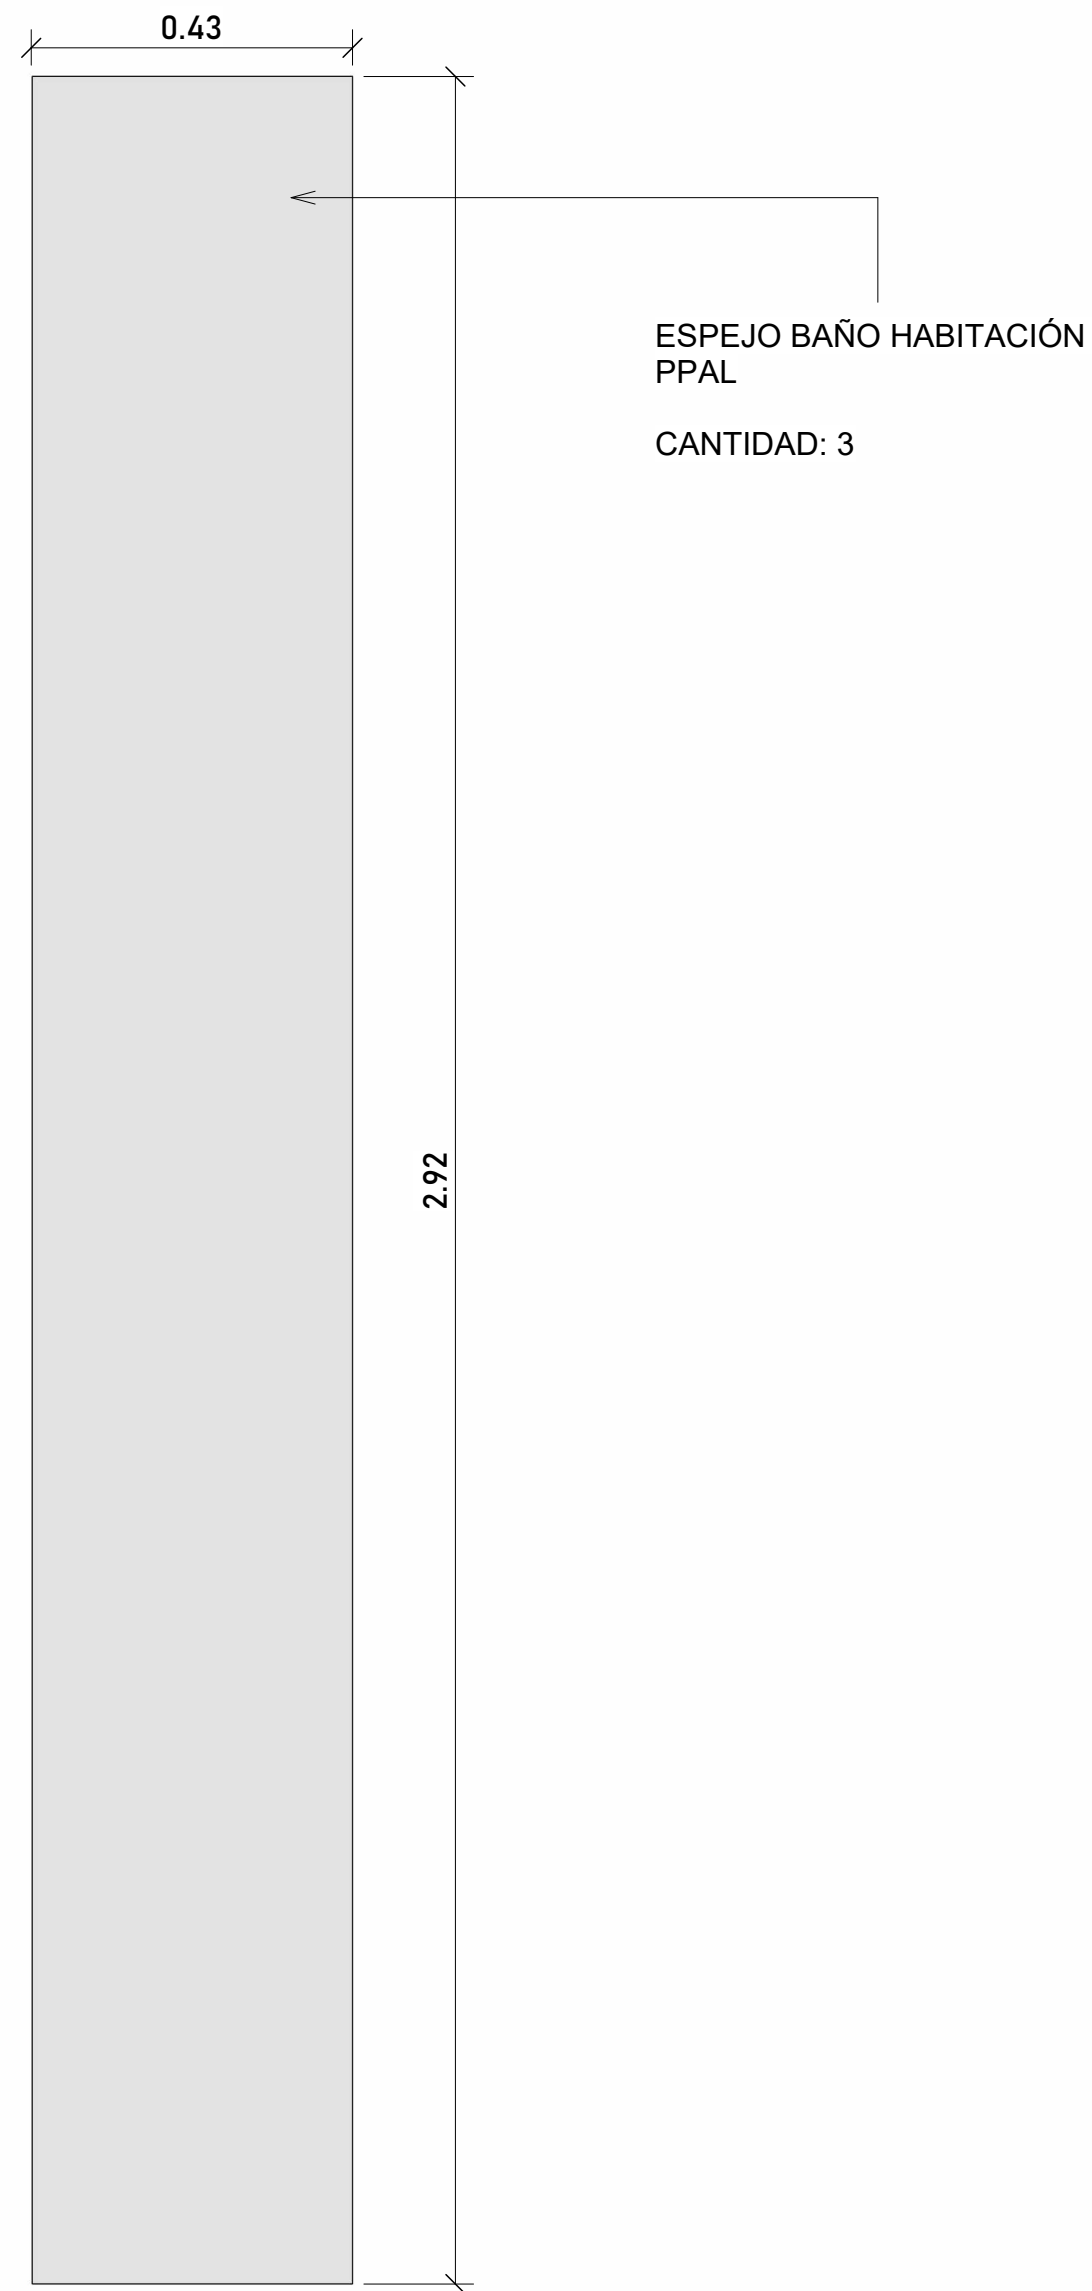

1 ESPEJO BAÑO SOCIAL
ESC 1:10

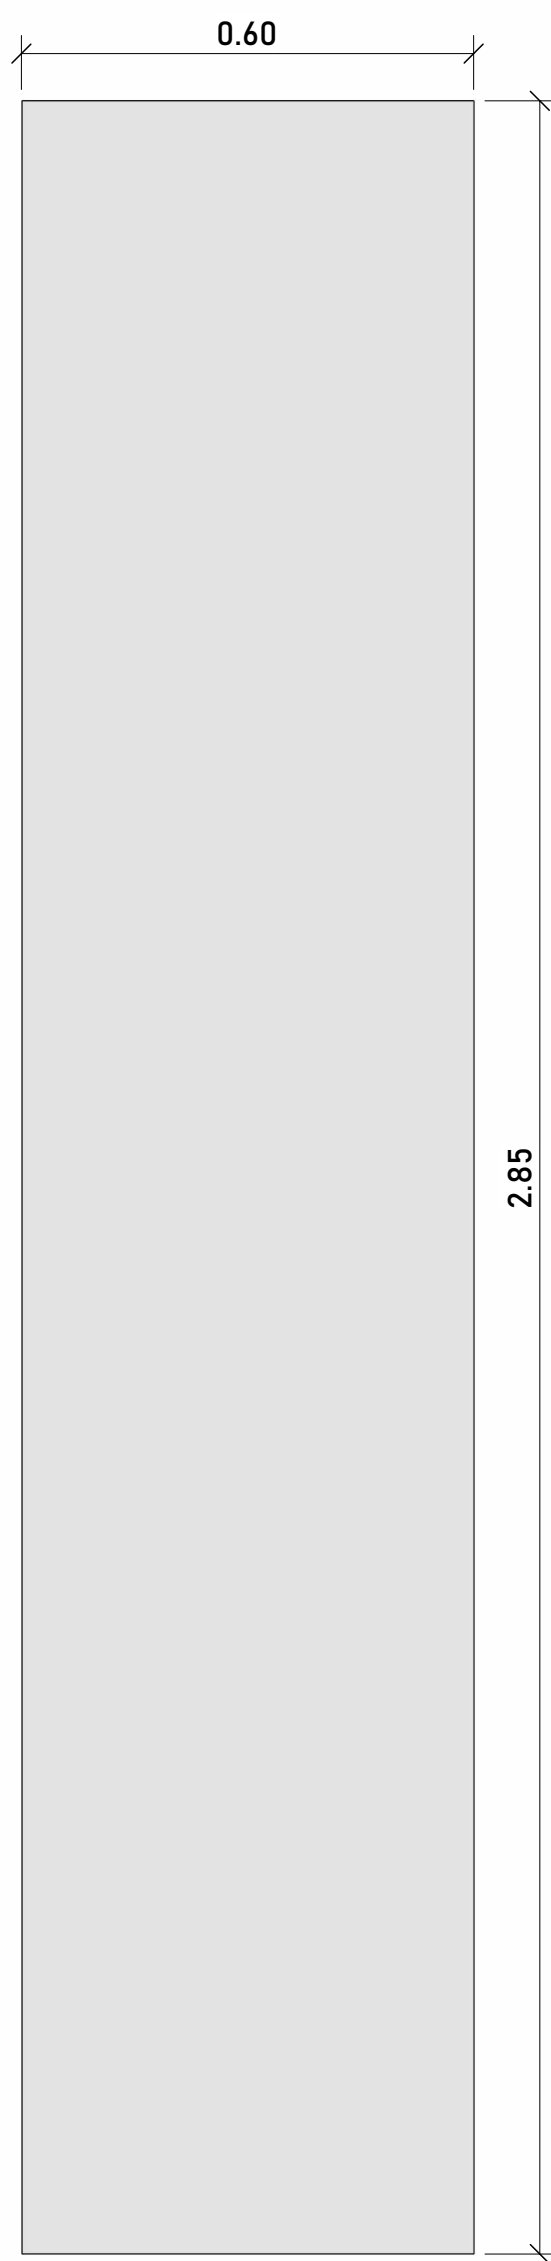

2 ESPEJO VESTIER HABITACIÓN PPAL
ESC 1:10

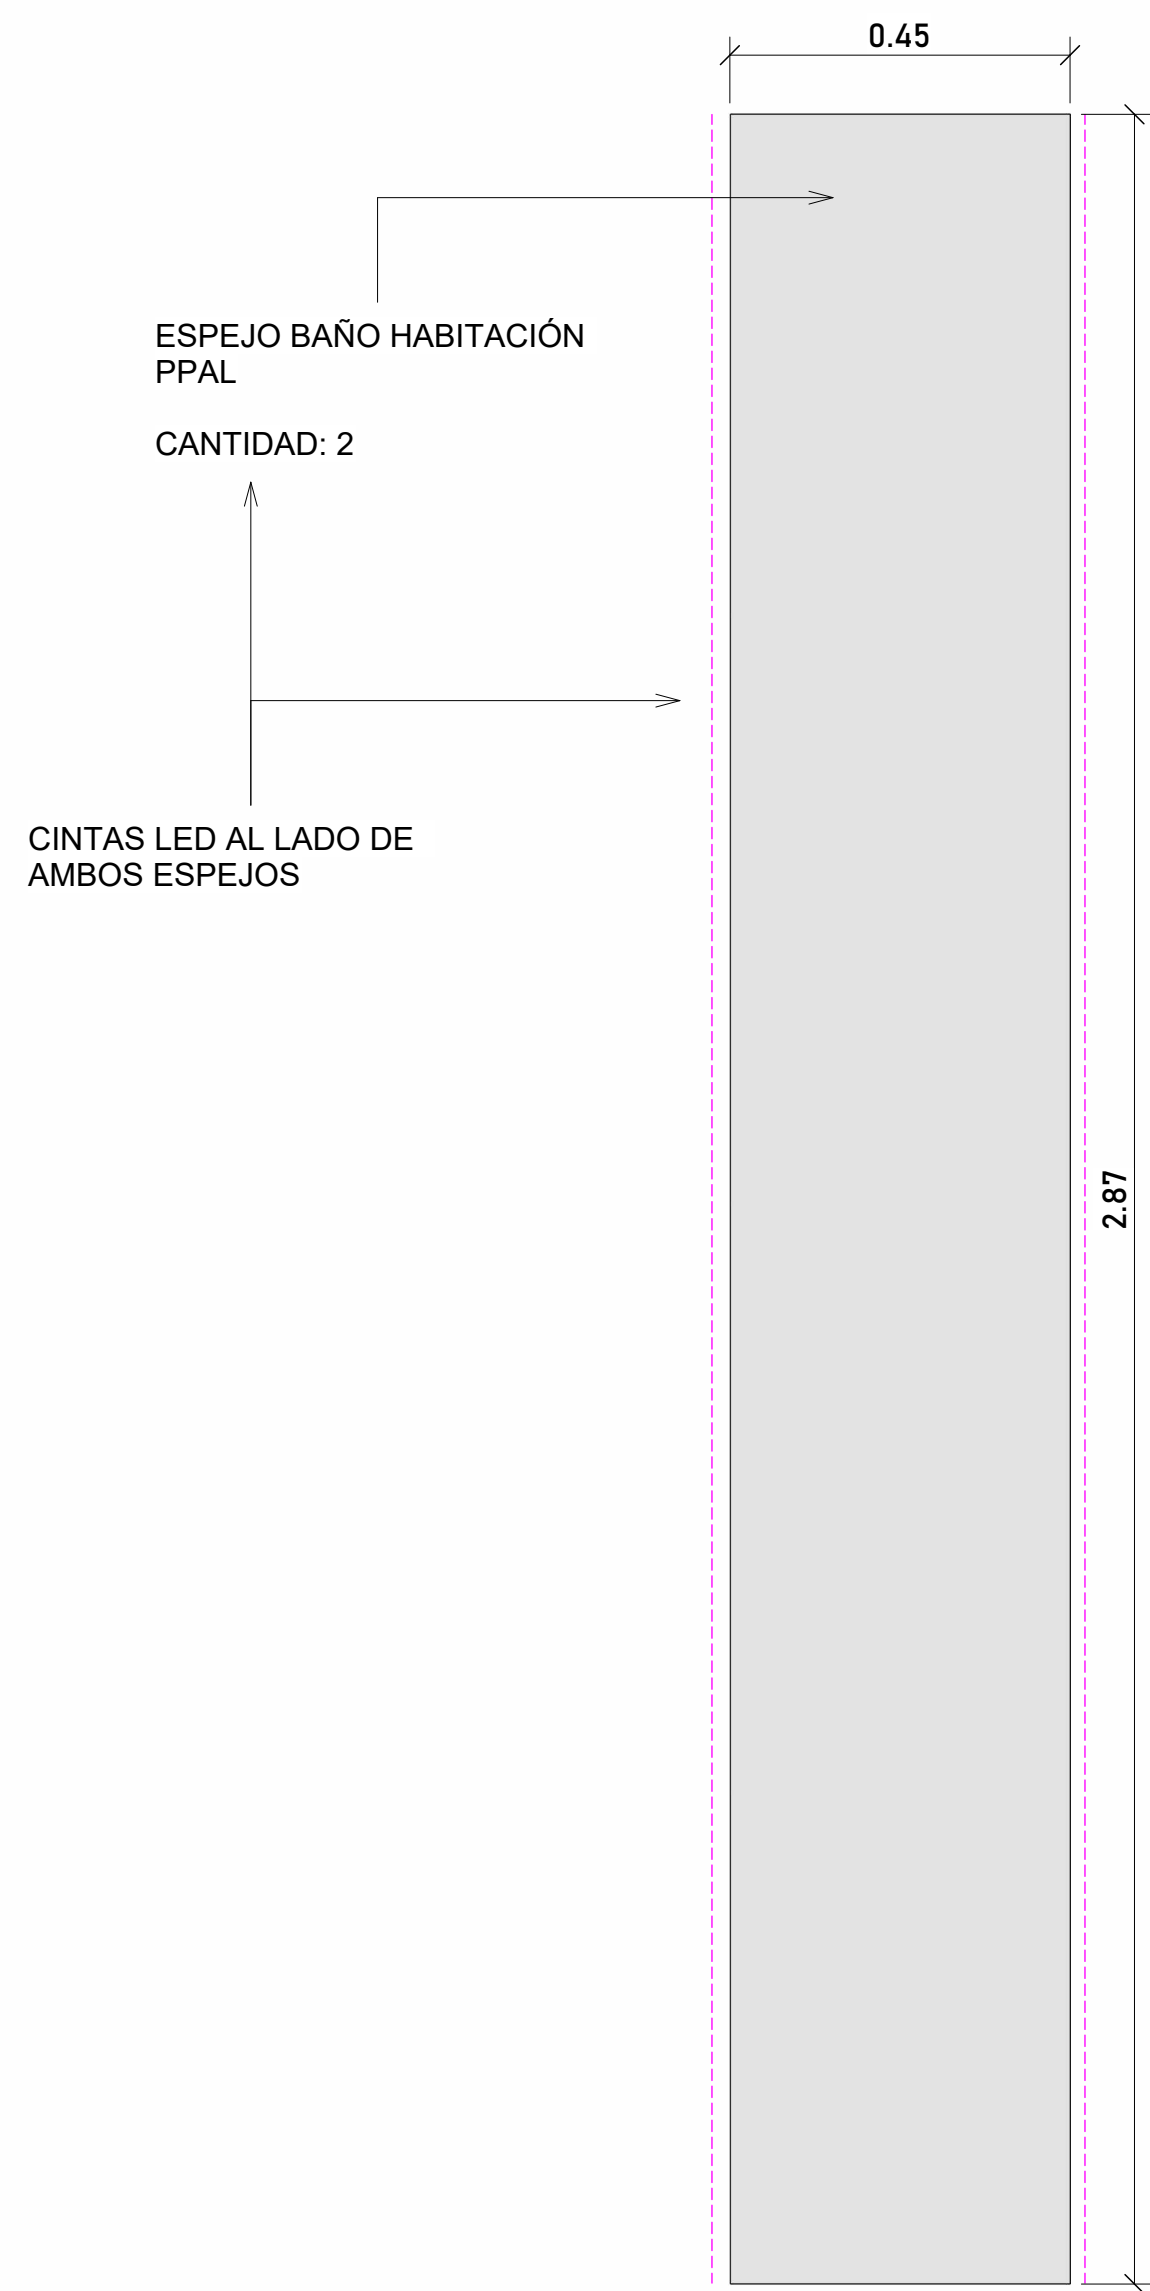

3 ESPEJO BAÑO HABITACIÓN PPAL
ESC 1:10

Proyecto:
HARAS

Matrícula inmobiliaria:
No 020-238645

Parcelación:
Parcelación Haras
Campestre – P.H.

Número de lote:
Lote No. 4 Llanogrande

Observaciones:
Según NSR-10 A 9.2.3, para el diseño de los elementos no estructurales se ha considerado GRUPO DE USO I y grado de desempeño BAJO

Revisa:
ANA SOFIA ROLDAN

Verifica:
DANIELA ARIZA RAMIREZ

Aprueba:
DANIELA ARIZA RAMIREZ

Ciente:
SANDRA MEJIA VELEZ Y
EDWIN ALFREDO ACOSTA

Diseño:
DANIELA ARIZA
RAMIREZ

Cálculos estructurales:
12/14/25

Archivo de Referencia:
20251017_DISEÑO
HARAS

Contiene:
DETALLE ESPEJO BAÑOS

Escala:
1:75

Fecha:
2025/22/01

Dibujo:
JORDY PINEDA BELLIDO

Plancha N°:
A9

De:
9

Firmas: